


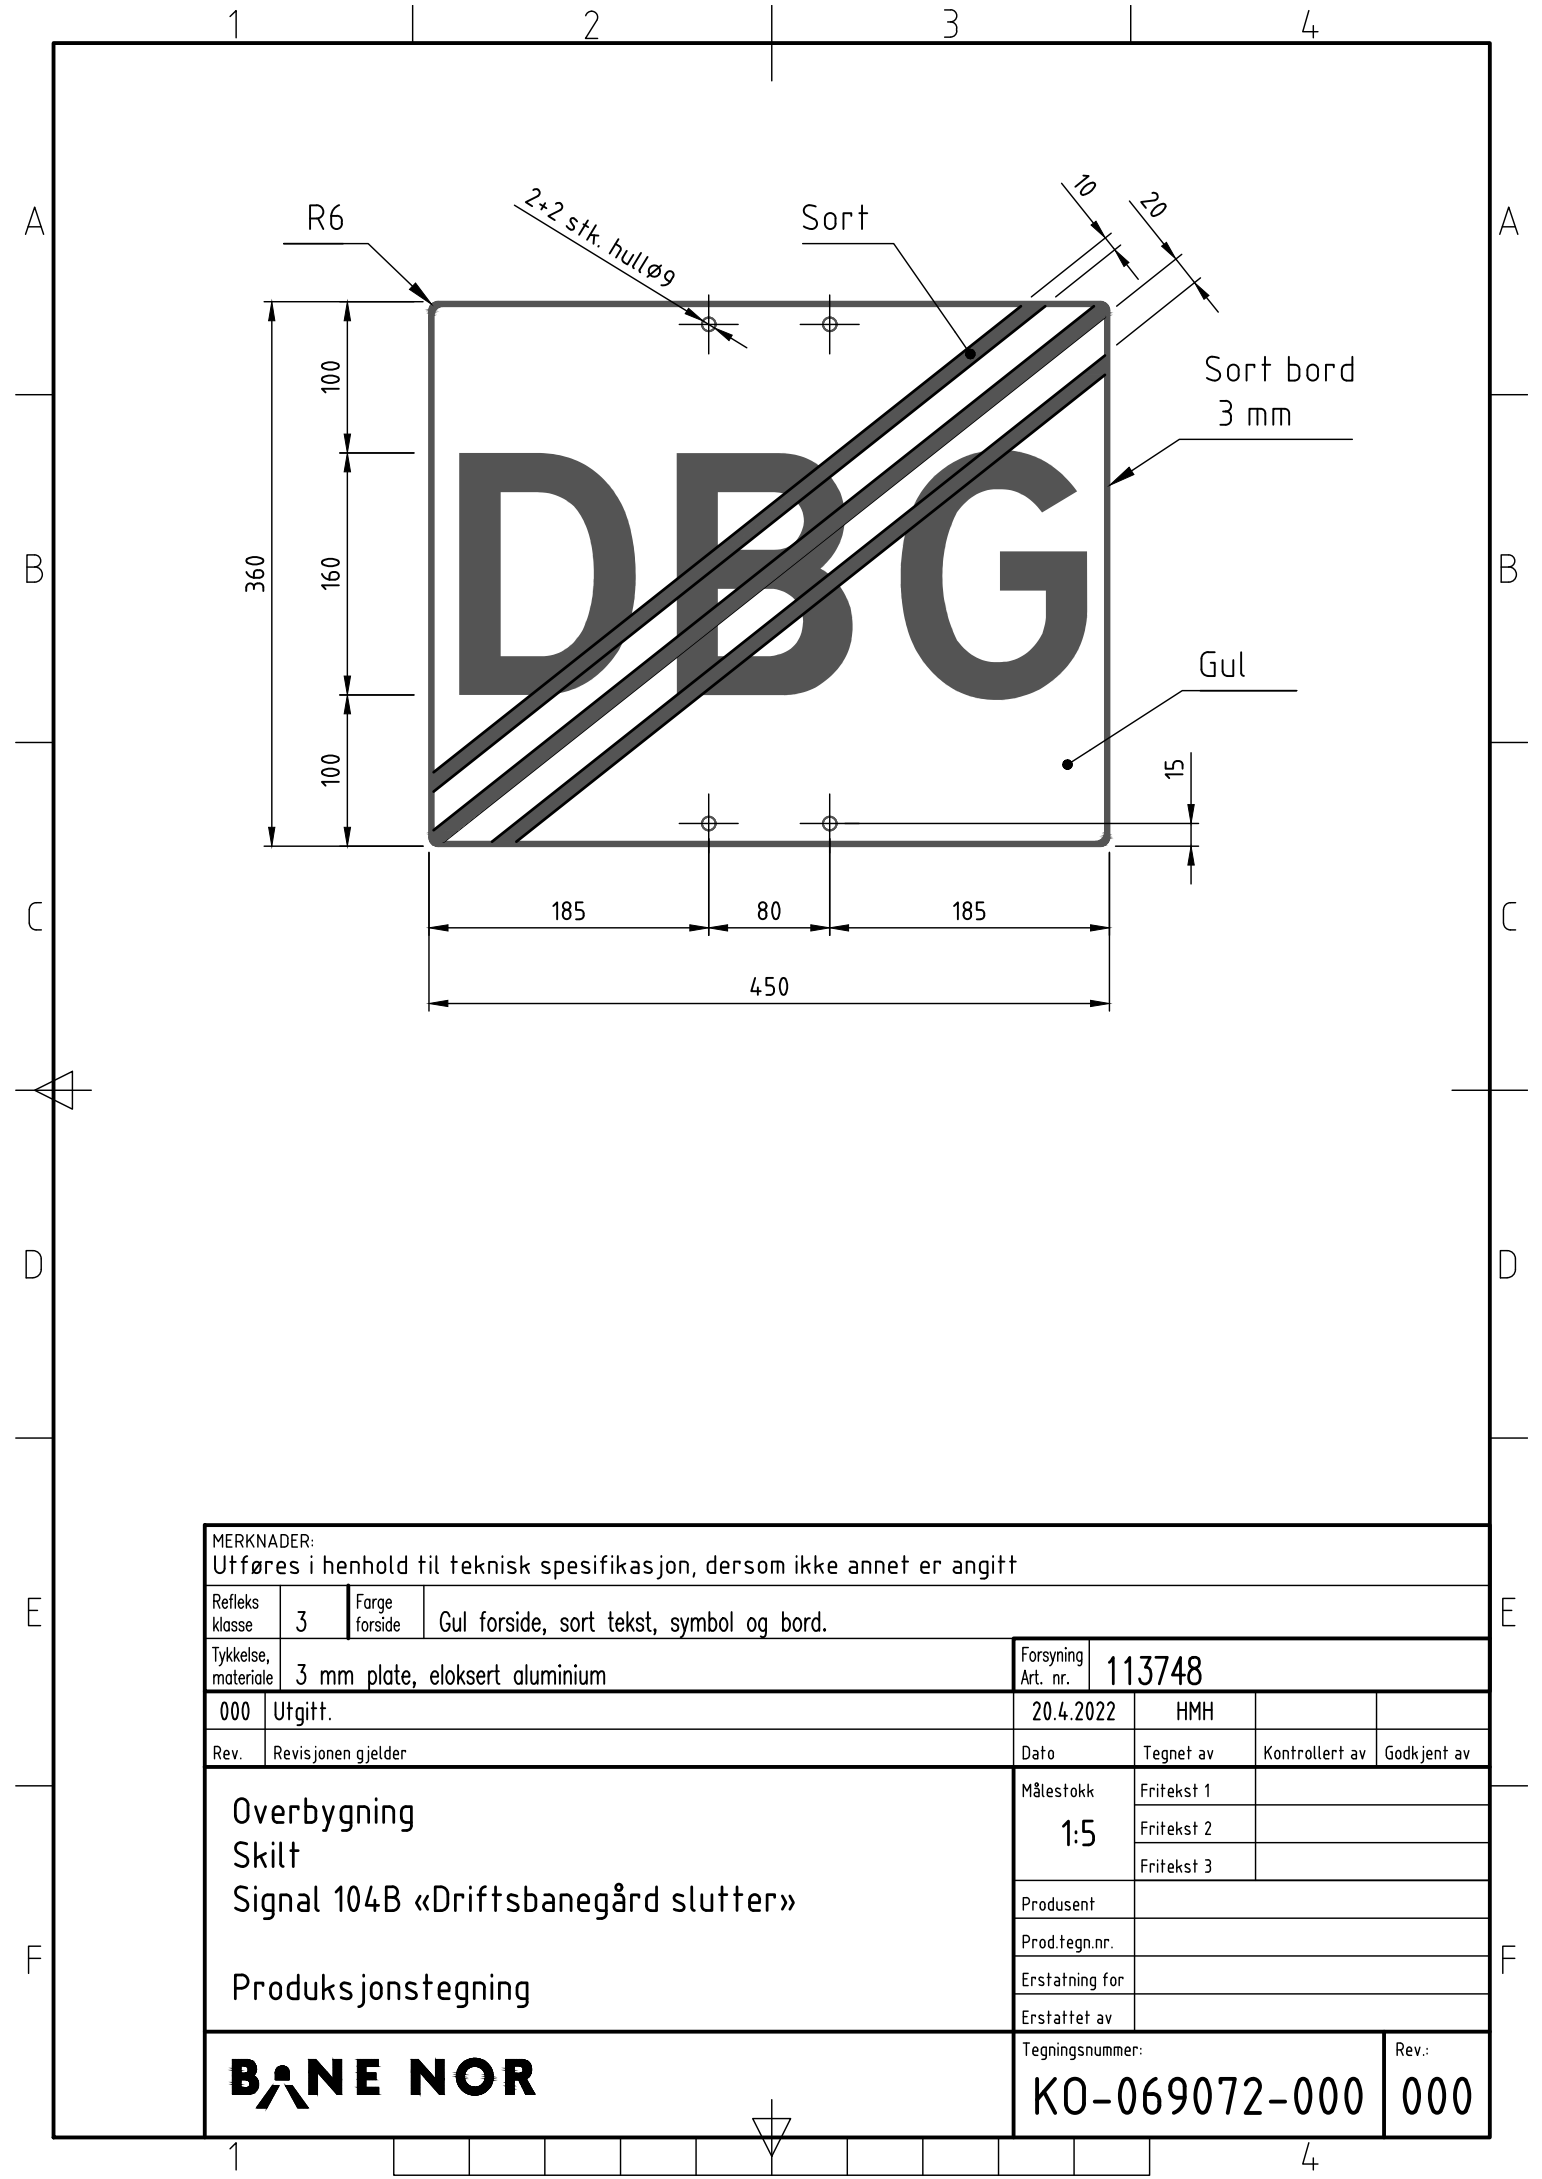

MERKNADER:

Utføres i henhold til teknisk spesifikasjon, dersom ikke annet er angitt

Refleks klasse	3	Farge forside	Gul forside, sort tekst, symbol og bord.					
Tykkelse, materiale	3 mm plate, eloksert aluminium				Forsyning Art. nr.	113748		
000	Utgitt.				20.4.2022	HMH		
Rev.	Revisjonen gjelder				Dato	Tegnet av	Kontrollert av	Godkjent av
Overbygning Skilt Signal 104B «Driftsbanegård slutter» Produksjonstegning					Målestokk	Fritekst 1		
					1:5	Fritekst 2		
						Fritekst 3		
					Produsent			
					Prod.tegn.nr.			
					Erstatning for			
					Erstattet av			
BANE NOR					Tegningsnummer:		Rev.:	
					KO-069072-000		000	