


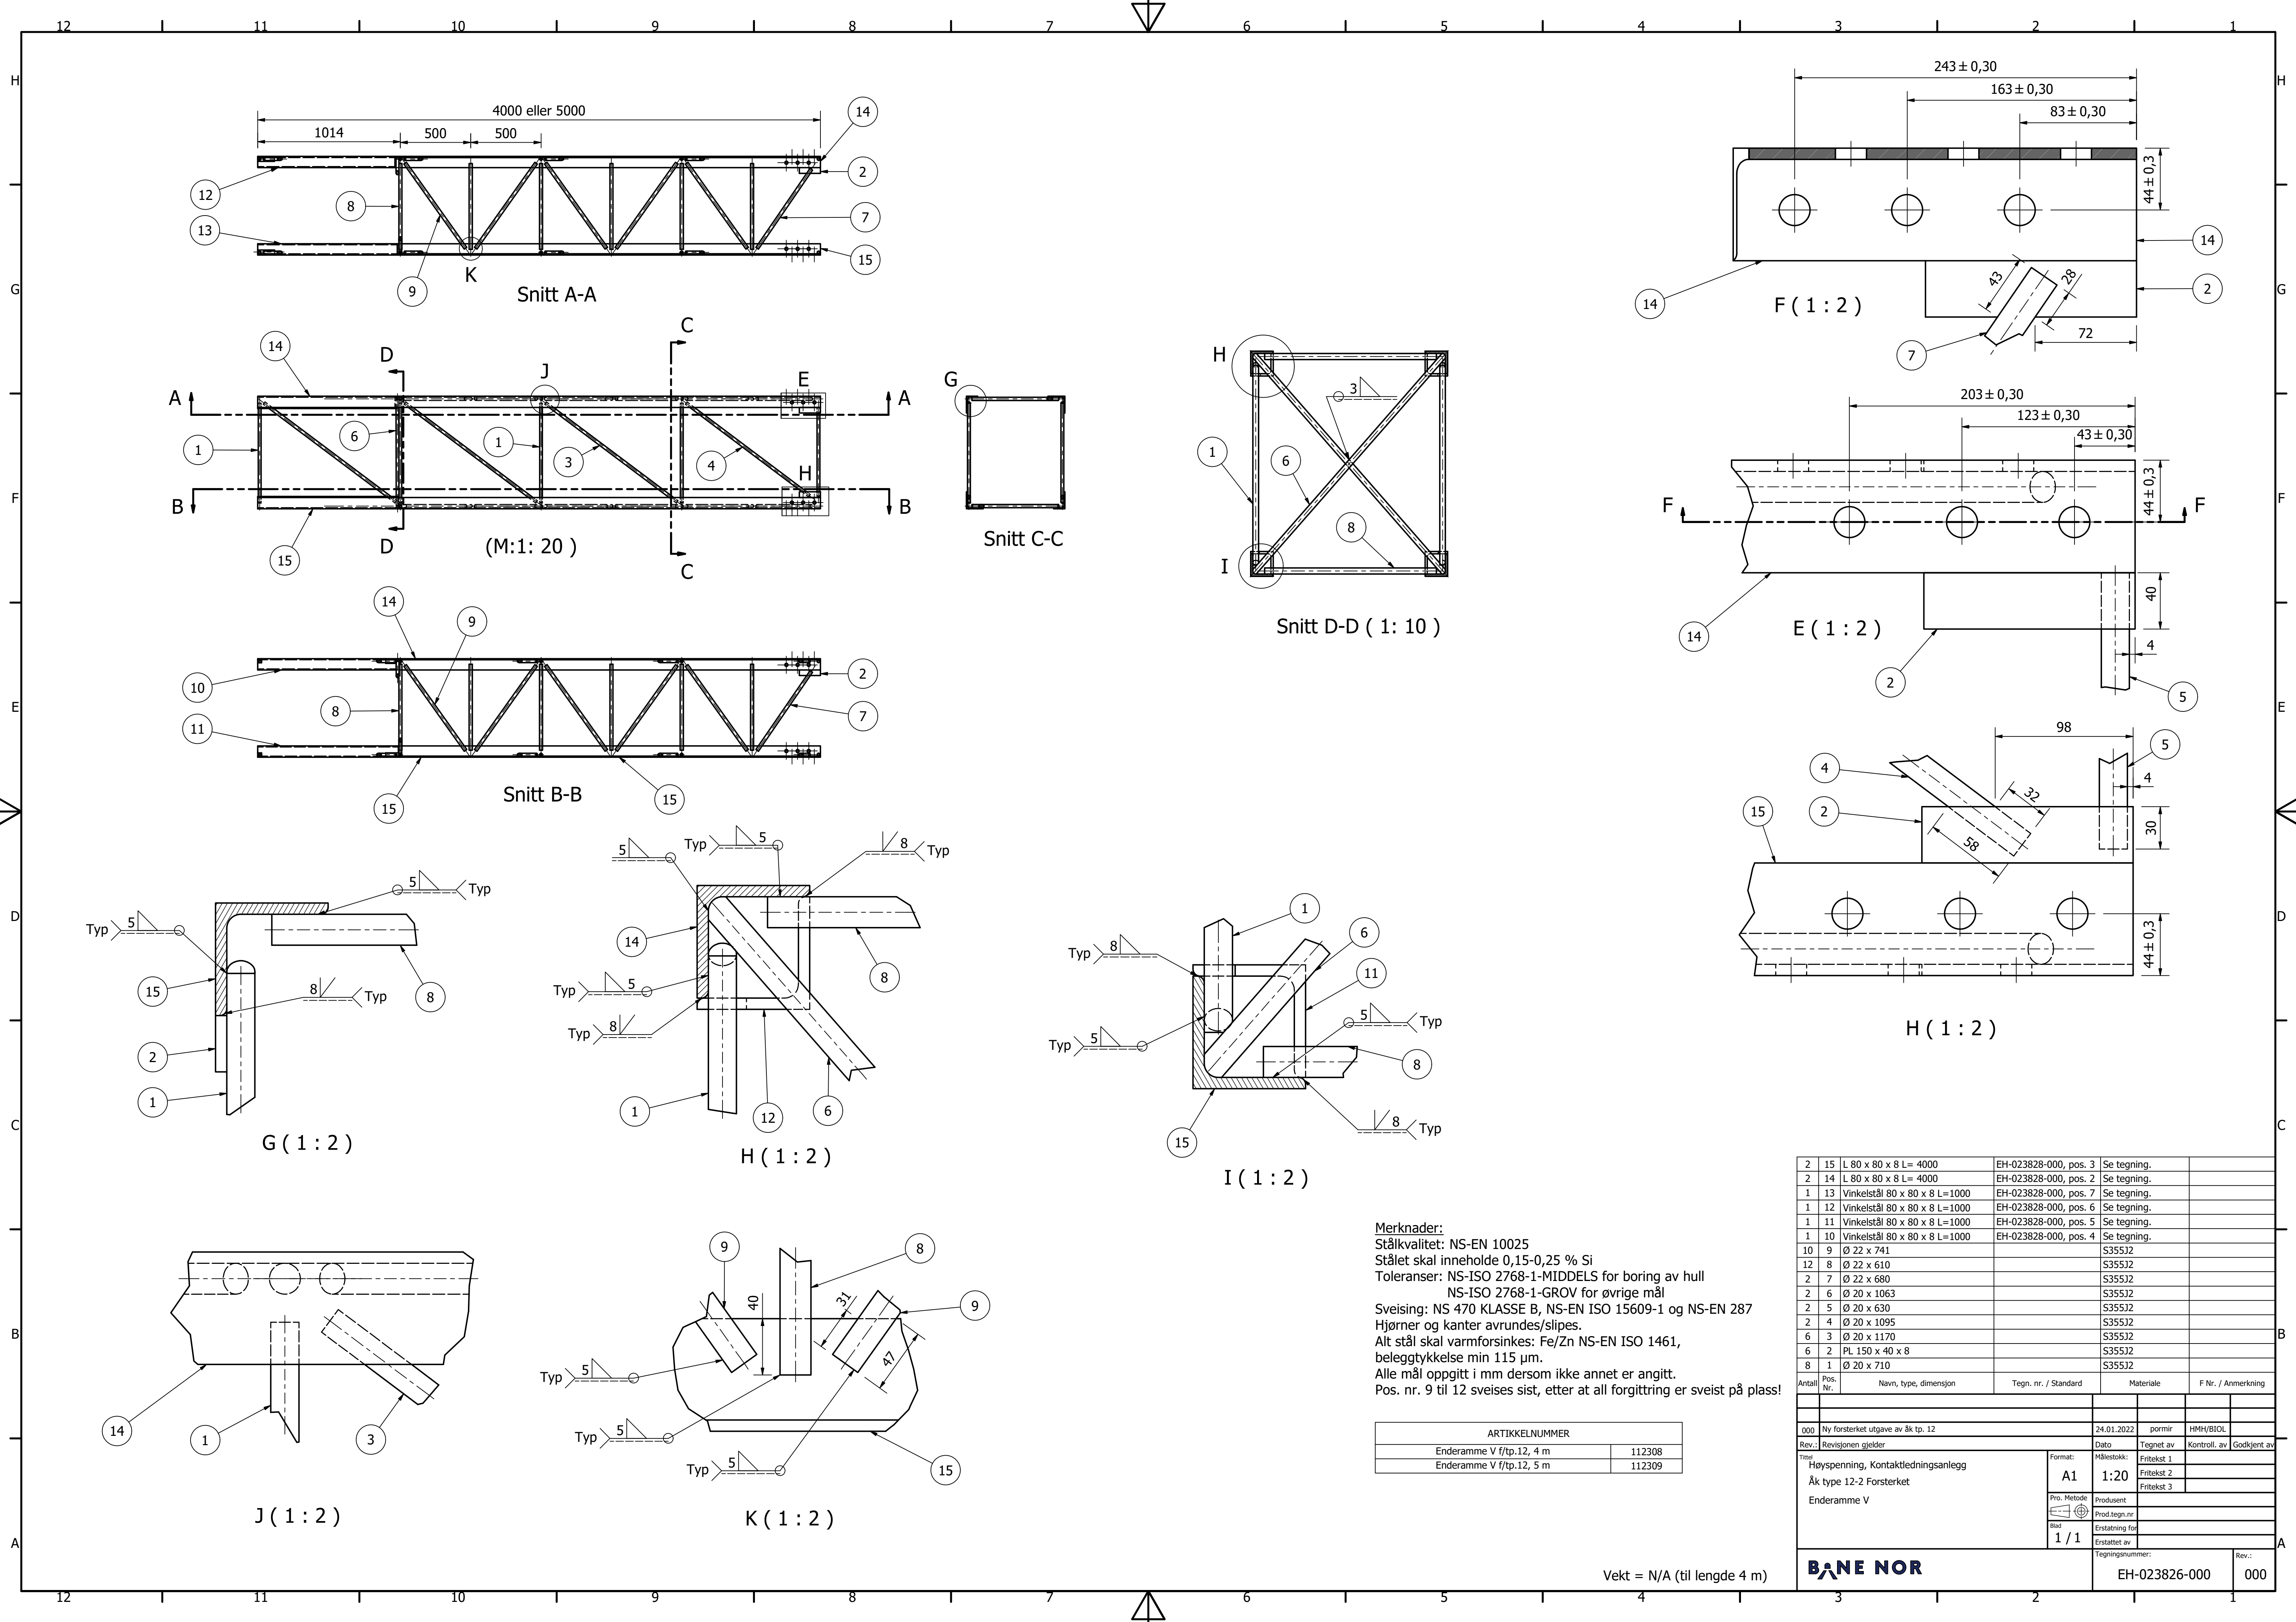

Merknader:
Stålkvalitet: NS-EN 10025
Stålet skal inneholde 0,15-0,25 % Si
Toleranser: NS-ISO 2768-1-MIDDELS for boring av hull
NS-ISO 2768-1-GROV for øvrige mål
Sveising: NS 470 KLASSE B, NS-EN ISO 15609-1 og NS-EN 287
Hjørner og kanter avrundes/slipes.
Alt stål skal varmforsinkes: Fe/Zn NS-EN ISO 1461,
beleggtykkelse min 115 µm.
Alle mål oppgitt i mm dersom ikke annet er angitt.
Pos. nr. 9 til 12 sveises sist, etter at all forgittring er sveist på plass!

ARTIKKELNUMMER	
Enderamme V f/tp.12, 4 m	112308
Enderamme V f/tp.12, 5 m	112309

2	15	L 80 x 80 x 8 L= 4000	EH-023828-000, pos. 3	Se tegning.		
2	14	L 80 x 80 x 8 L= 4000	EH-023828-000, pos. 2	Se tegning.		
1	13	Vinkelstål 80 x 80 x 8 L=1000	EH-023828-000, pos. 7	Se tegning.		
1	12	Vinkelstål 80 x 80 x 8 L=1000	EH-023828-000, pos. 6	Se tegning.		
1	11	Vinkelstål 80 x 80 x 8 L=1000	EH-023828-000, pos. 5	Se tegning.		
1	10	Vinkelstål 80 x 80 x 8 L=1000	EH-023828-000, pos. 4	Se tegning.		
10	9	Ø 22 x 741		S355J2		
12	8	Ø 22 x 610		S355J2		
2	7	Ø 22 x 680		S355J2		
2	6	Ø 20 x 1063		S355J2		
2	5	Ø 20 x 630		S355J2		
2	4	Ø 20 x 1095		S355J2		
6	3	Ø 20 x 1170		S355J2		
6	2	PL 150 x 40 x 8		S355J2		
8	1	Ø 20 x 710		S355J2		

000	Ny forsterket utgave av åk tp. 12			24.01.2022	pomir	HHH/BIOL		
Rev.:	Revisjonen gjelder			Dato	Tegnet av	Kontroll. av	Godkjent av	
Tegn. Nr.	Høyspenning, Kontaktledningsanlegg Åk type 12-2 Forsterket Enderamme V	Format: A1	Målestokk:	Fritekst 1				
				Fritekst 2				
				Fritekst 3				
			Pro. Metode	Produsent				
			Prod.tegn.nr					
Blad			Erstatning for					
		1 / 1	Erstattet av					
				Tegningsnummer:			Rev.:	
				EH-023826-000			000	

BANE NOR

Vekt = N/A (til lengde 4 m)