

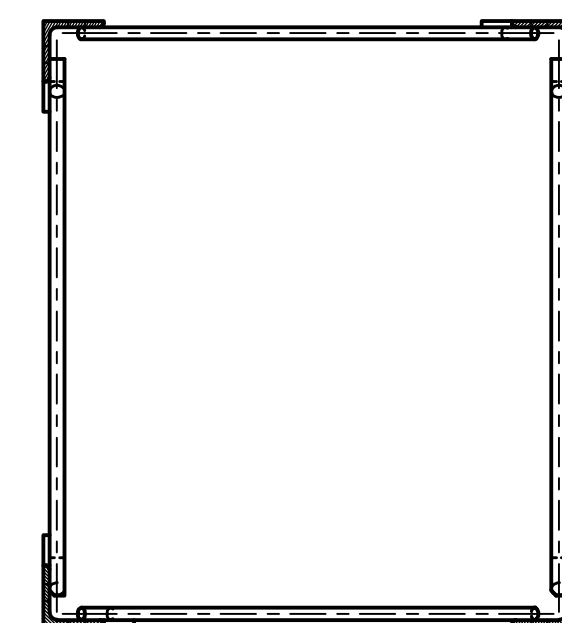
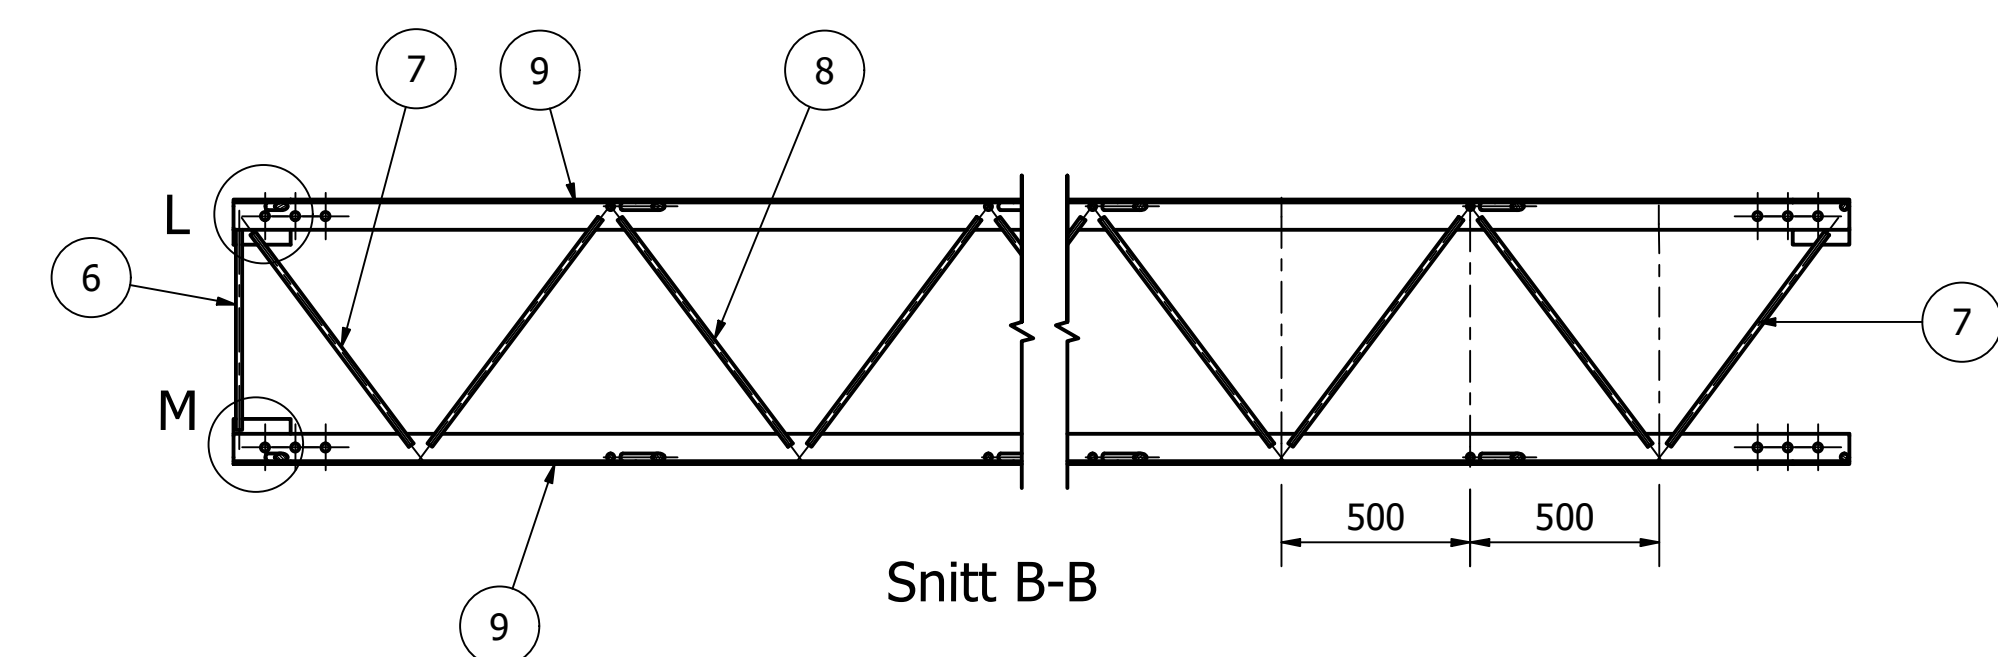
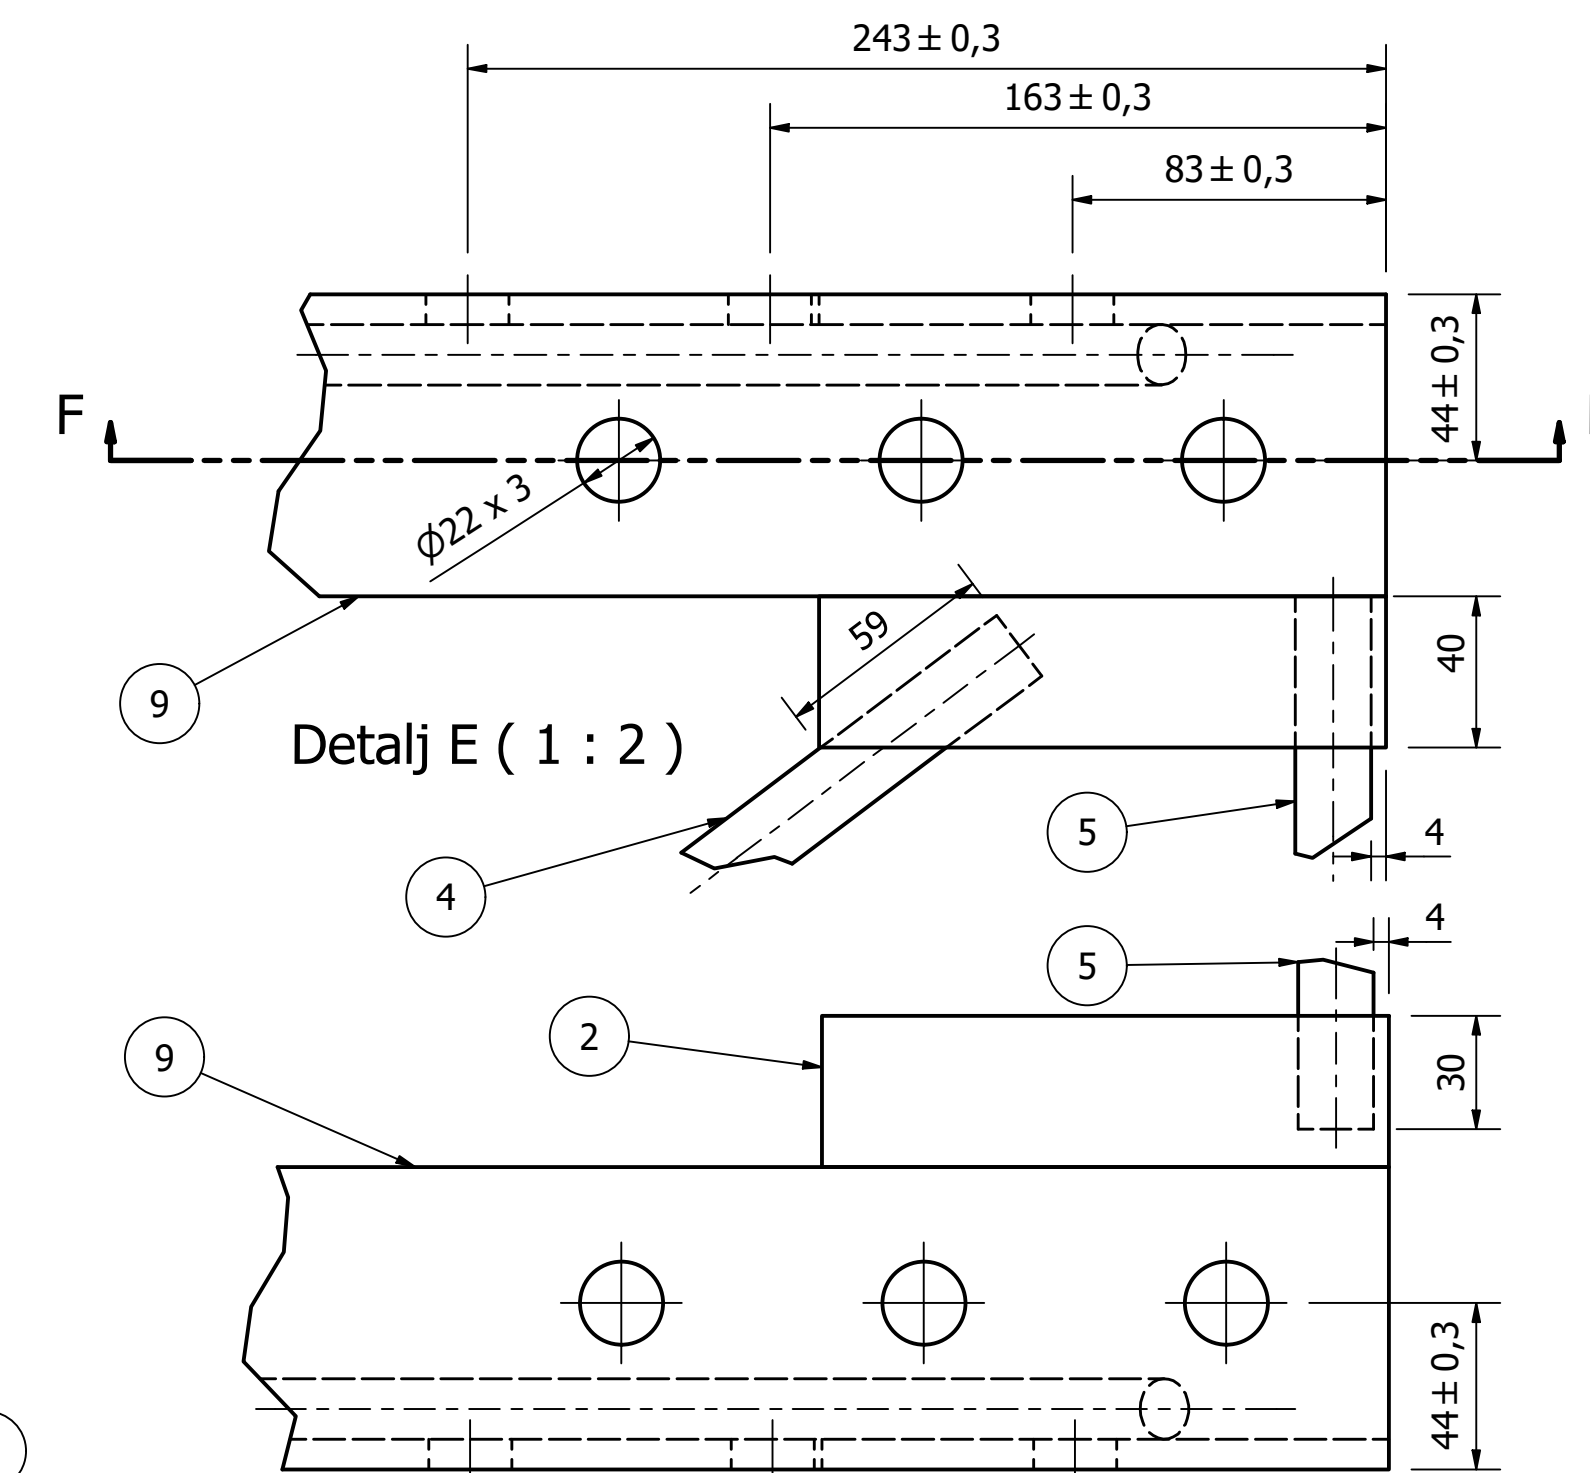
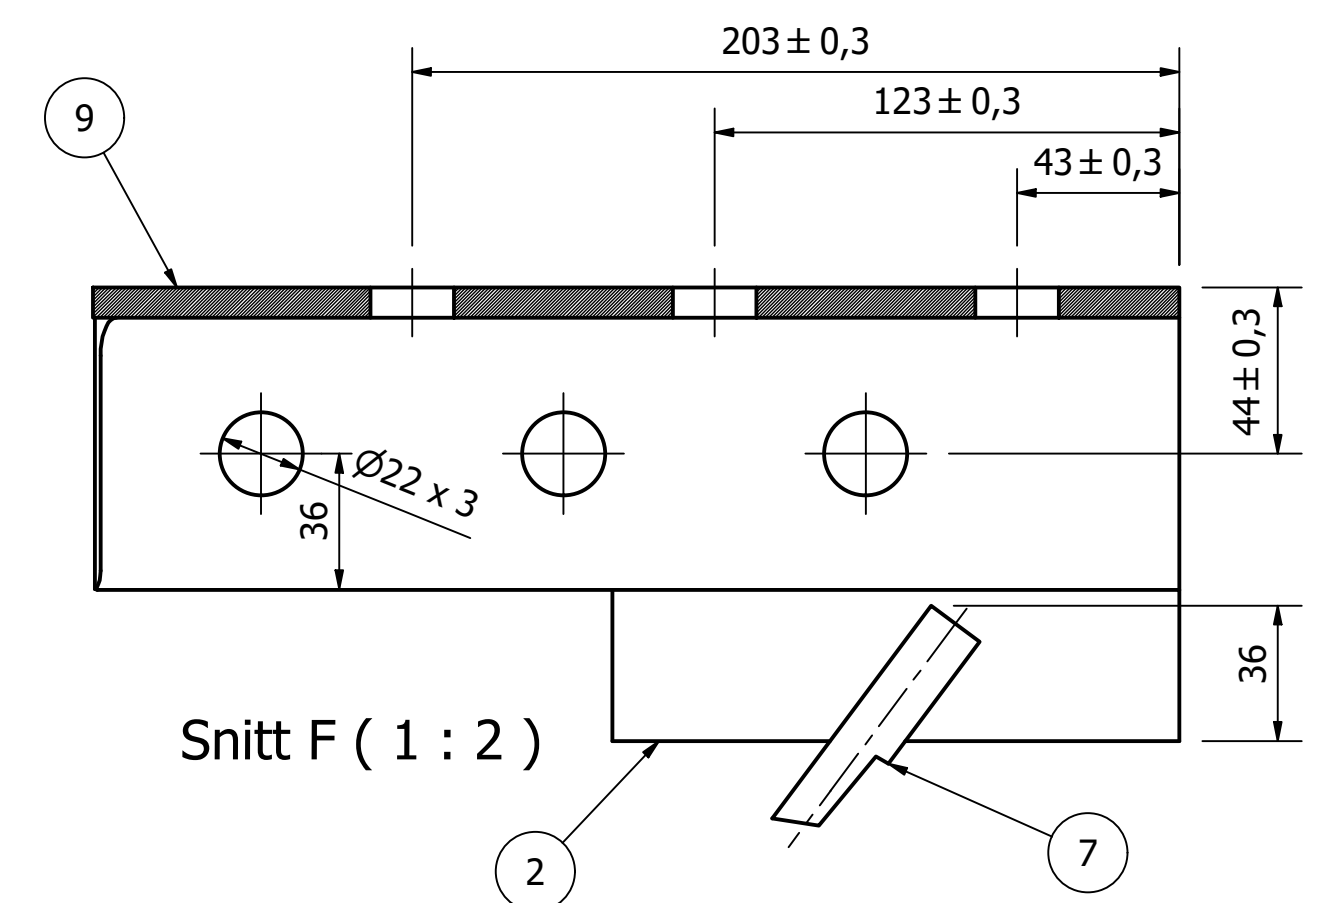
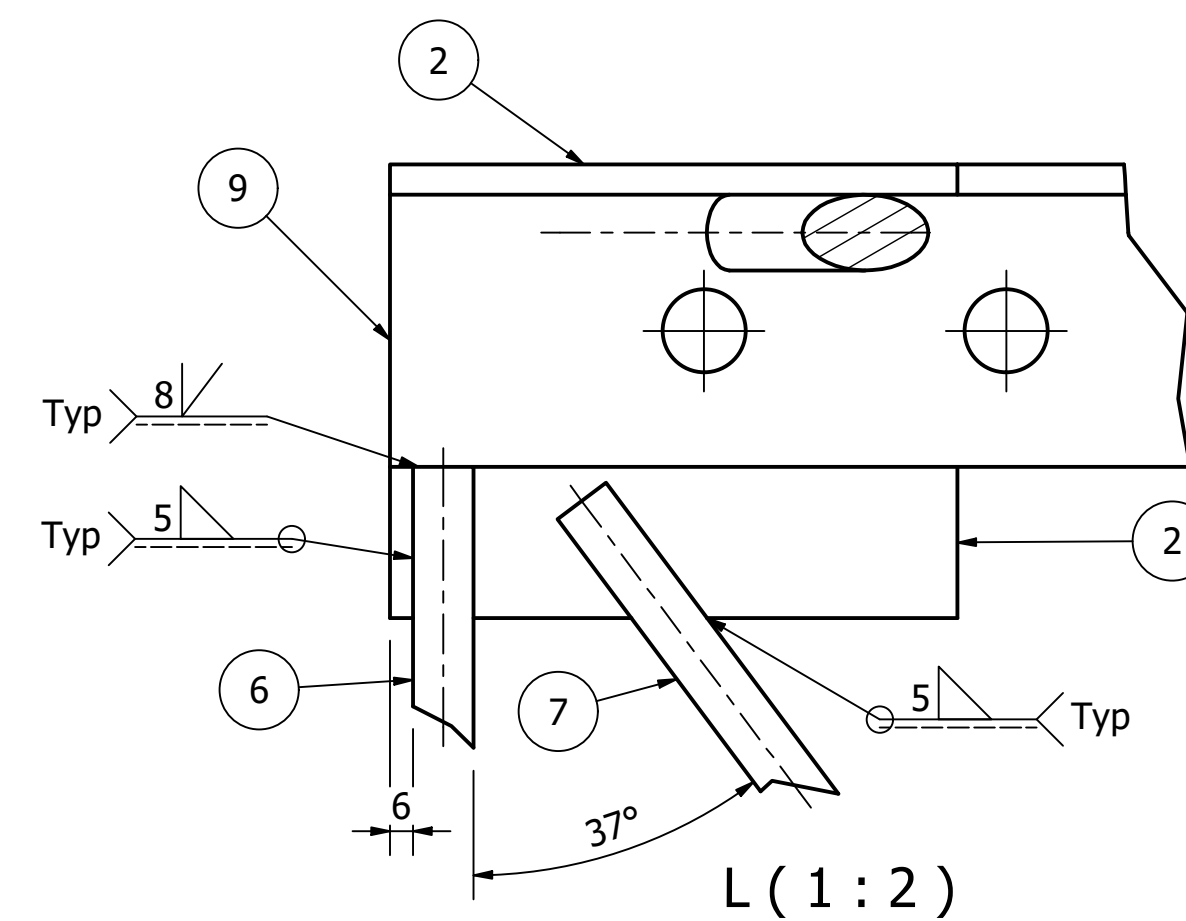
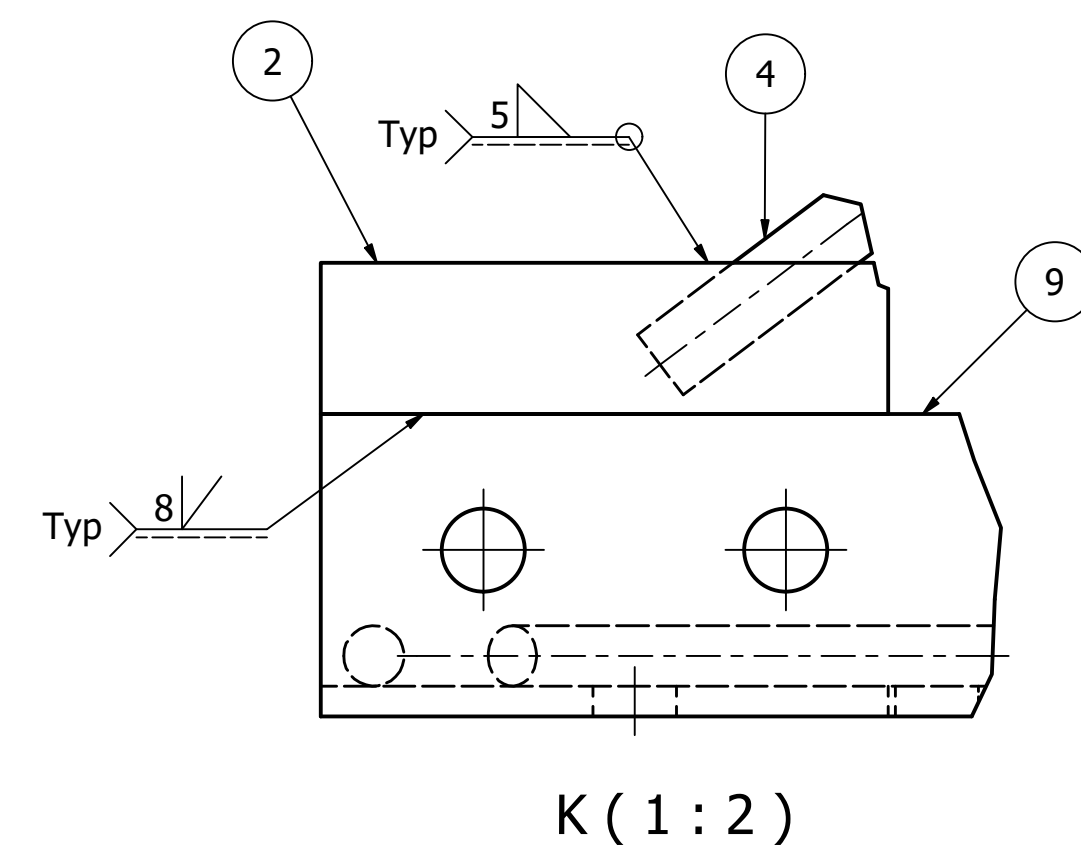
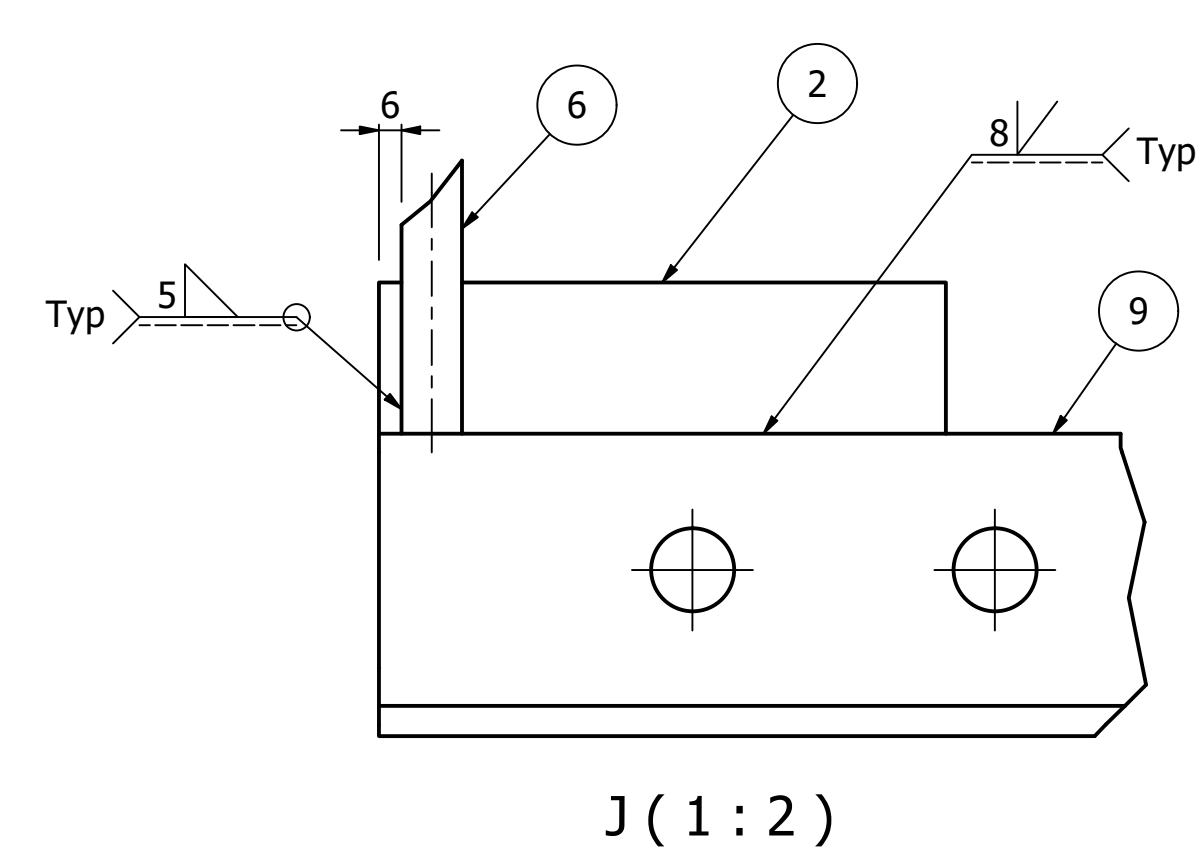


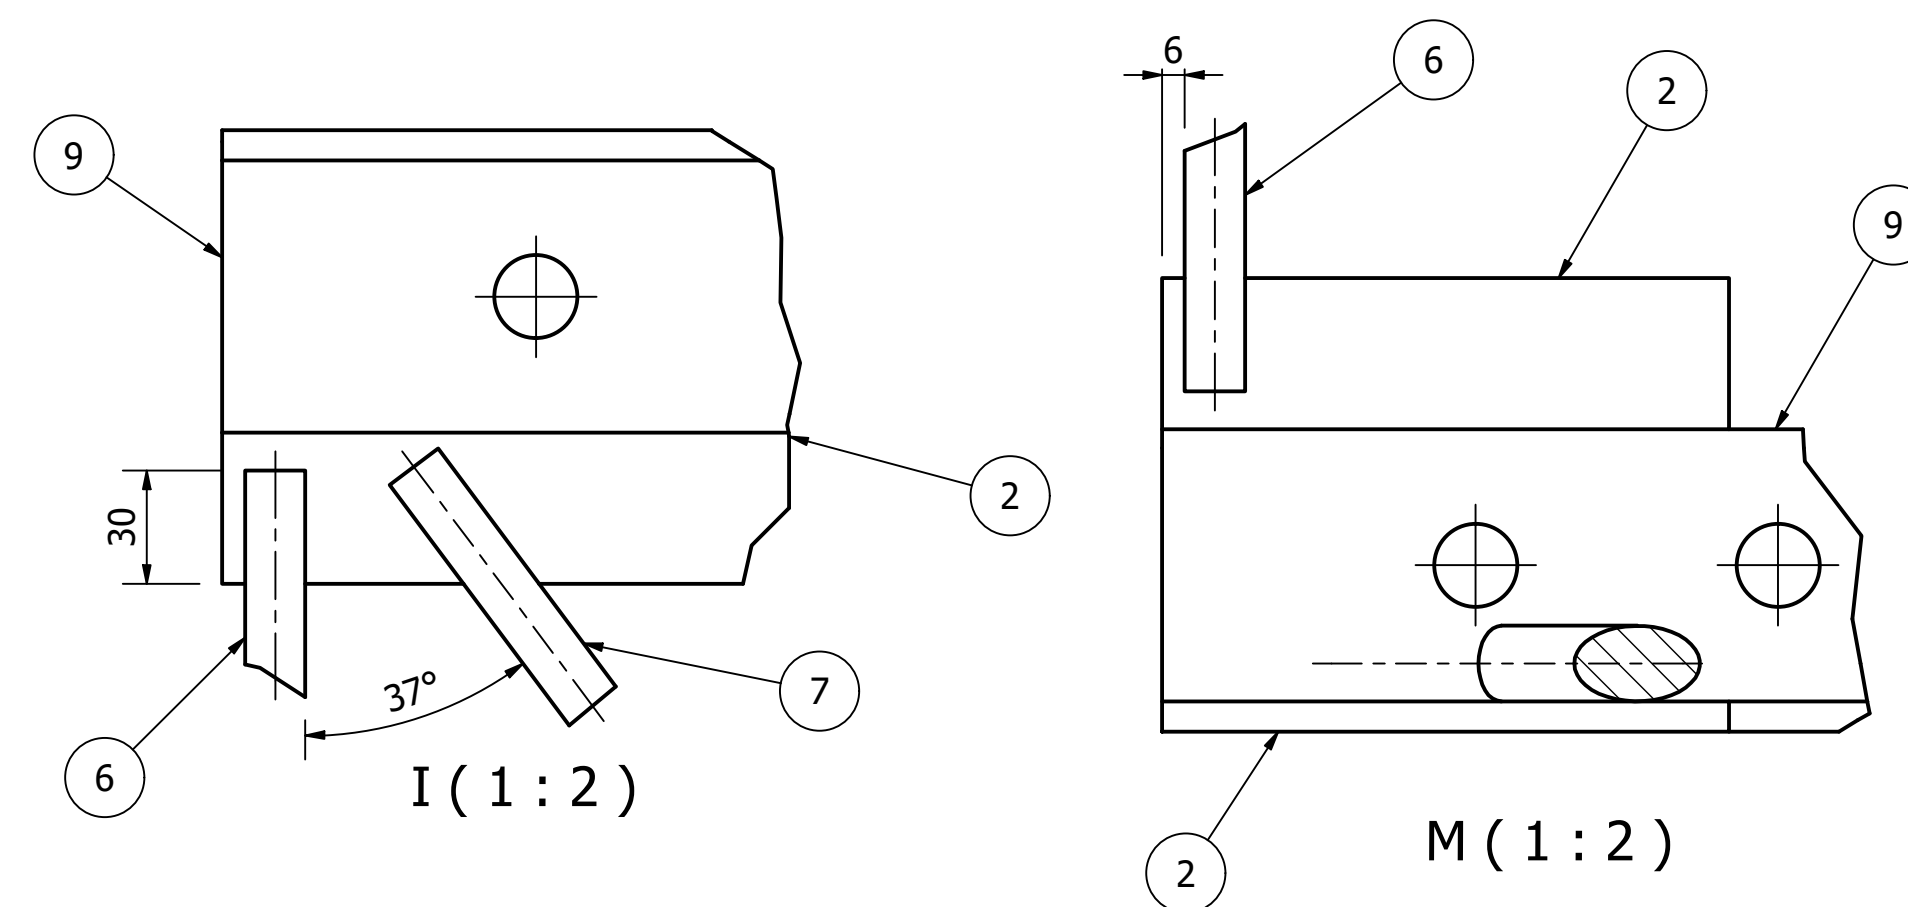

Typisk snitt C-C

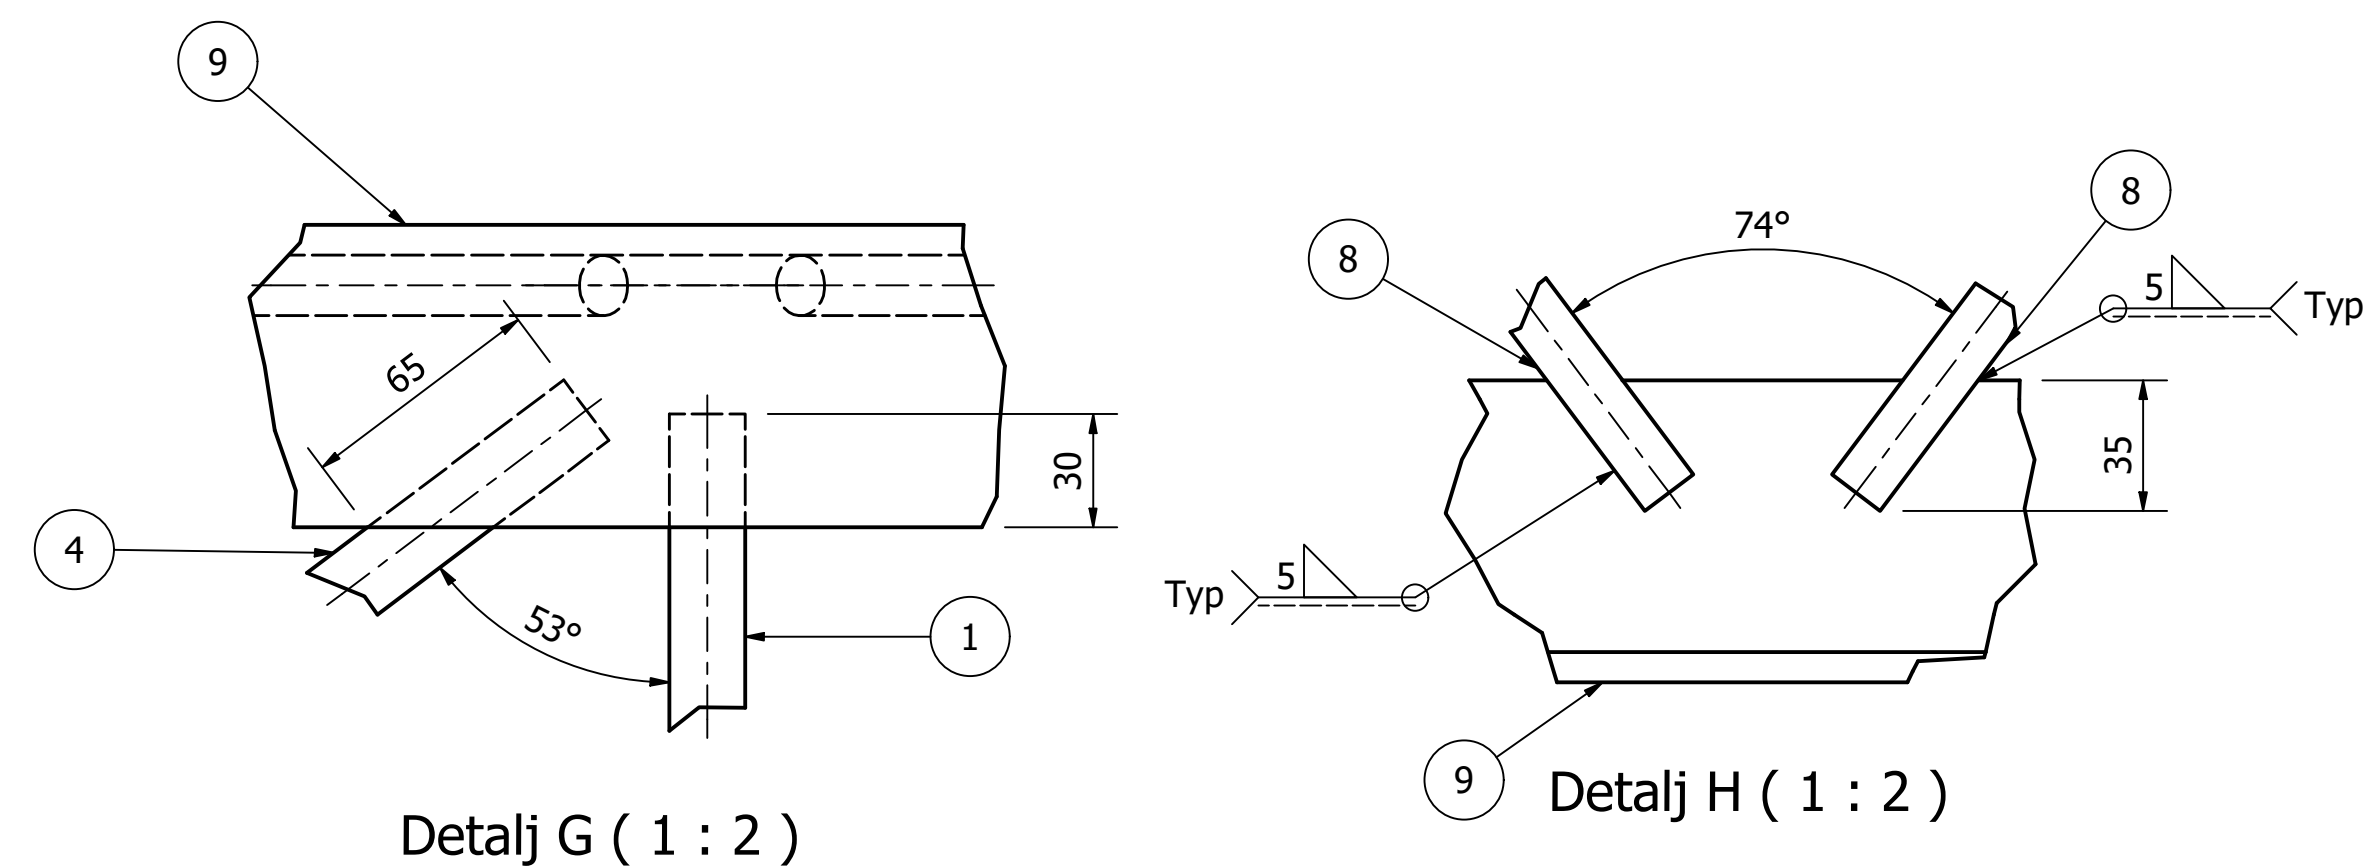

Detalj D (1 : 2)

Merknader:
Stålkvalitet: NS-EN 10025
Stålet skal inneholde 0,15-0,25 % Si
Toleranser: NS-ISO 2768-1-MIDDELS for boring av hull
NS-ISO 2768-1-GROV for øvrige mål
Sveising: NS 470 KLASSE B, NS-EN ISO 15609-1 og NS-EN 287
Hjørner og kanter avrundet/slipes.
Alt stål skal varmforsinkes: Fe/Zn NS-EN ISO 1461,
beleggtykkelse min 115 µm.
Alle mål oppgitt i mm dersom ikke annet er angitt.

ARTIKKELNUMMER	
Mellomramme f/tp.12-2, 3 m	112312
Mellomramme f/tp.12-2, 6 m	112313
Mellomramme f/tp.12-2, 9 m	112314

				L 80 x 80 x L = 3000, 6000 eller 9000		EH-023828-000, pos. 1	Se tegning.					
32	4	4	-	9	Ø 16 x 750		S355J2					
4	20	8	-	8	Ø 16 x 700		S355J2					
4	4	4	-	7	Ø 16 x 530		S355J2					
2	2	2	-	6	Ø 20 x 630		S355J2					
2	2	2	-	5	Ø 20 x 1095		S355J2					
4	4	4	-	4	Ø 20 x 1170		S355J2					
14	8	2	-	3	PL 150 x 40 x 8		S355J2					
12	12	12	-	2	Ø 20 x 710		S355J2					
16	10	4	-	1								
Antall	Antall	Antall	Antall	Pos. Nr.	Navn, type, dimensjon	Tegn. nr. / Standard	Materiale	F Nr. / Anmerkning				
L=9000	L=6000	L=3000		000	Nytt forsterket-åk tp. 12							
					Rev.: Revisjonen gjelder							
					Tittel: Høyspenning, Kontaktledningsanlegg							
					Åk type 12-2 Forsterket							
					Mellomramme LG 3000, LG 6000 og LG 9000							
					Tegning							
					Pro. Metode  Bild 1 / 1	Formst: A1			2:20		Målestokk: Fritekst 1 Fritekst 2 Fritekst 3	
						Produzent			Prod.tegn.nr		Erstatning for	
						Erstattet av						
						Tegningsnummer:			EH-023827-000		Rev.: 000	