


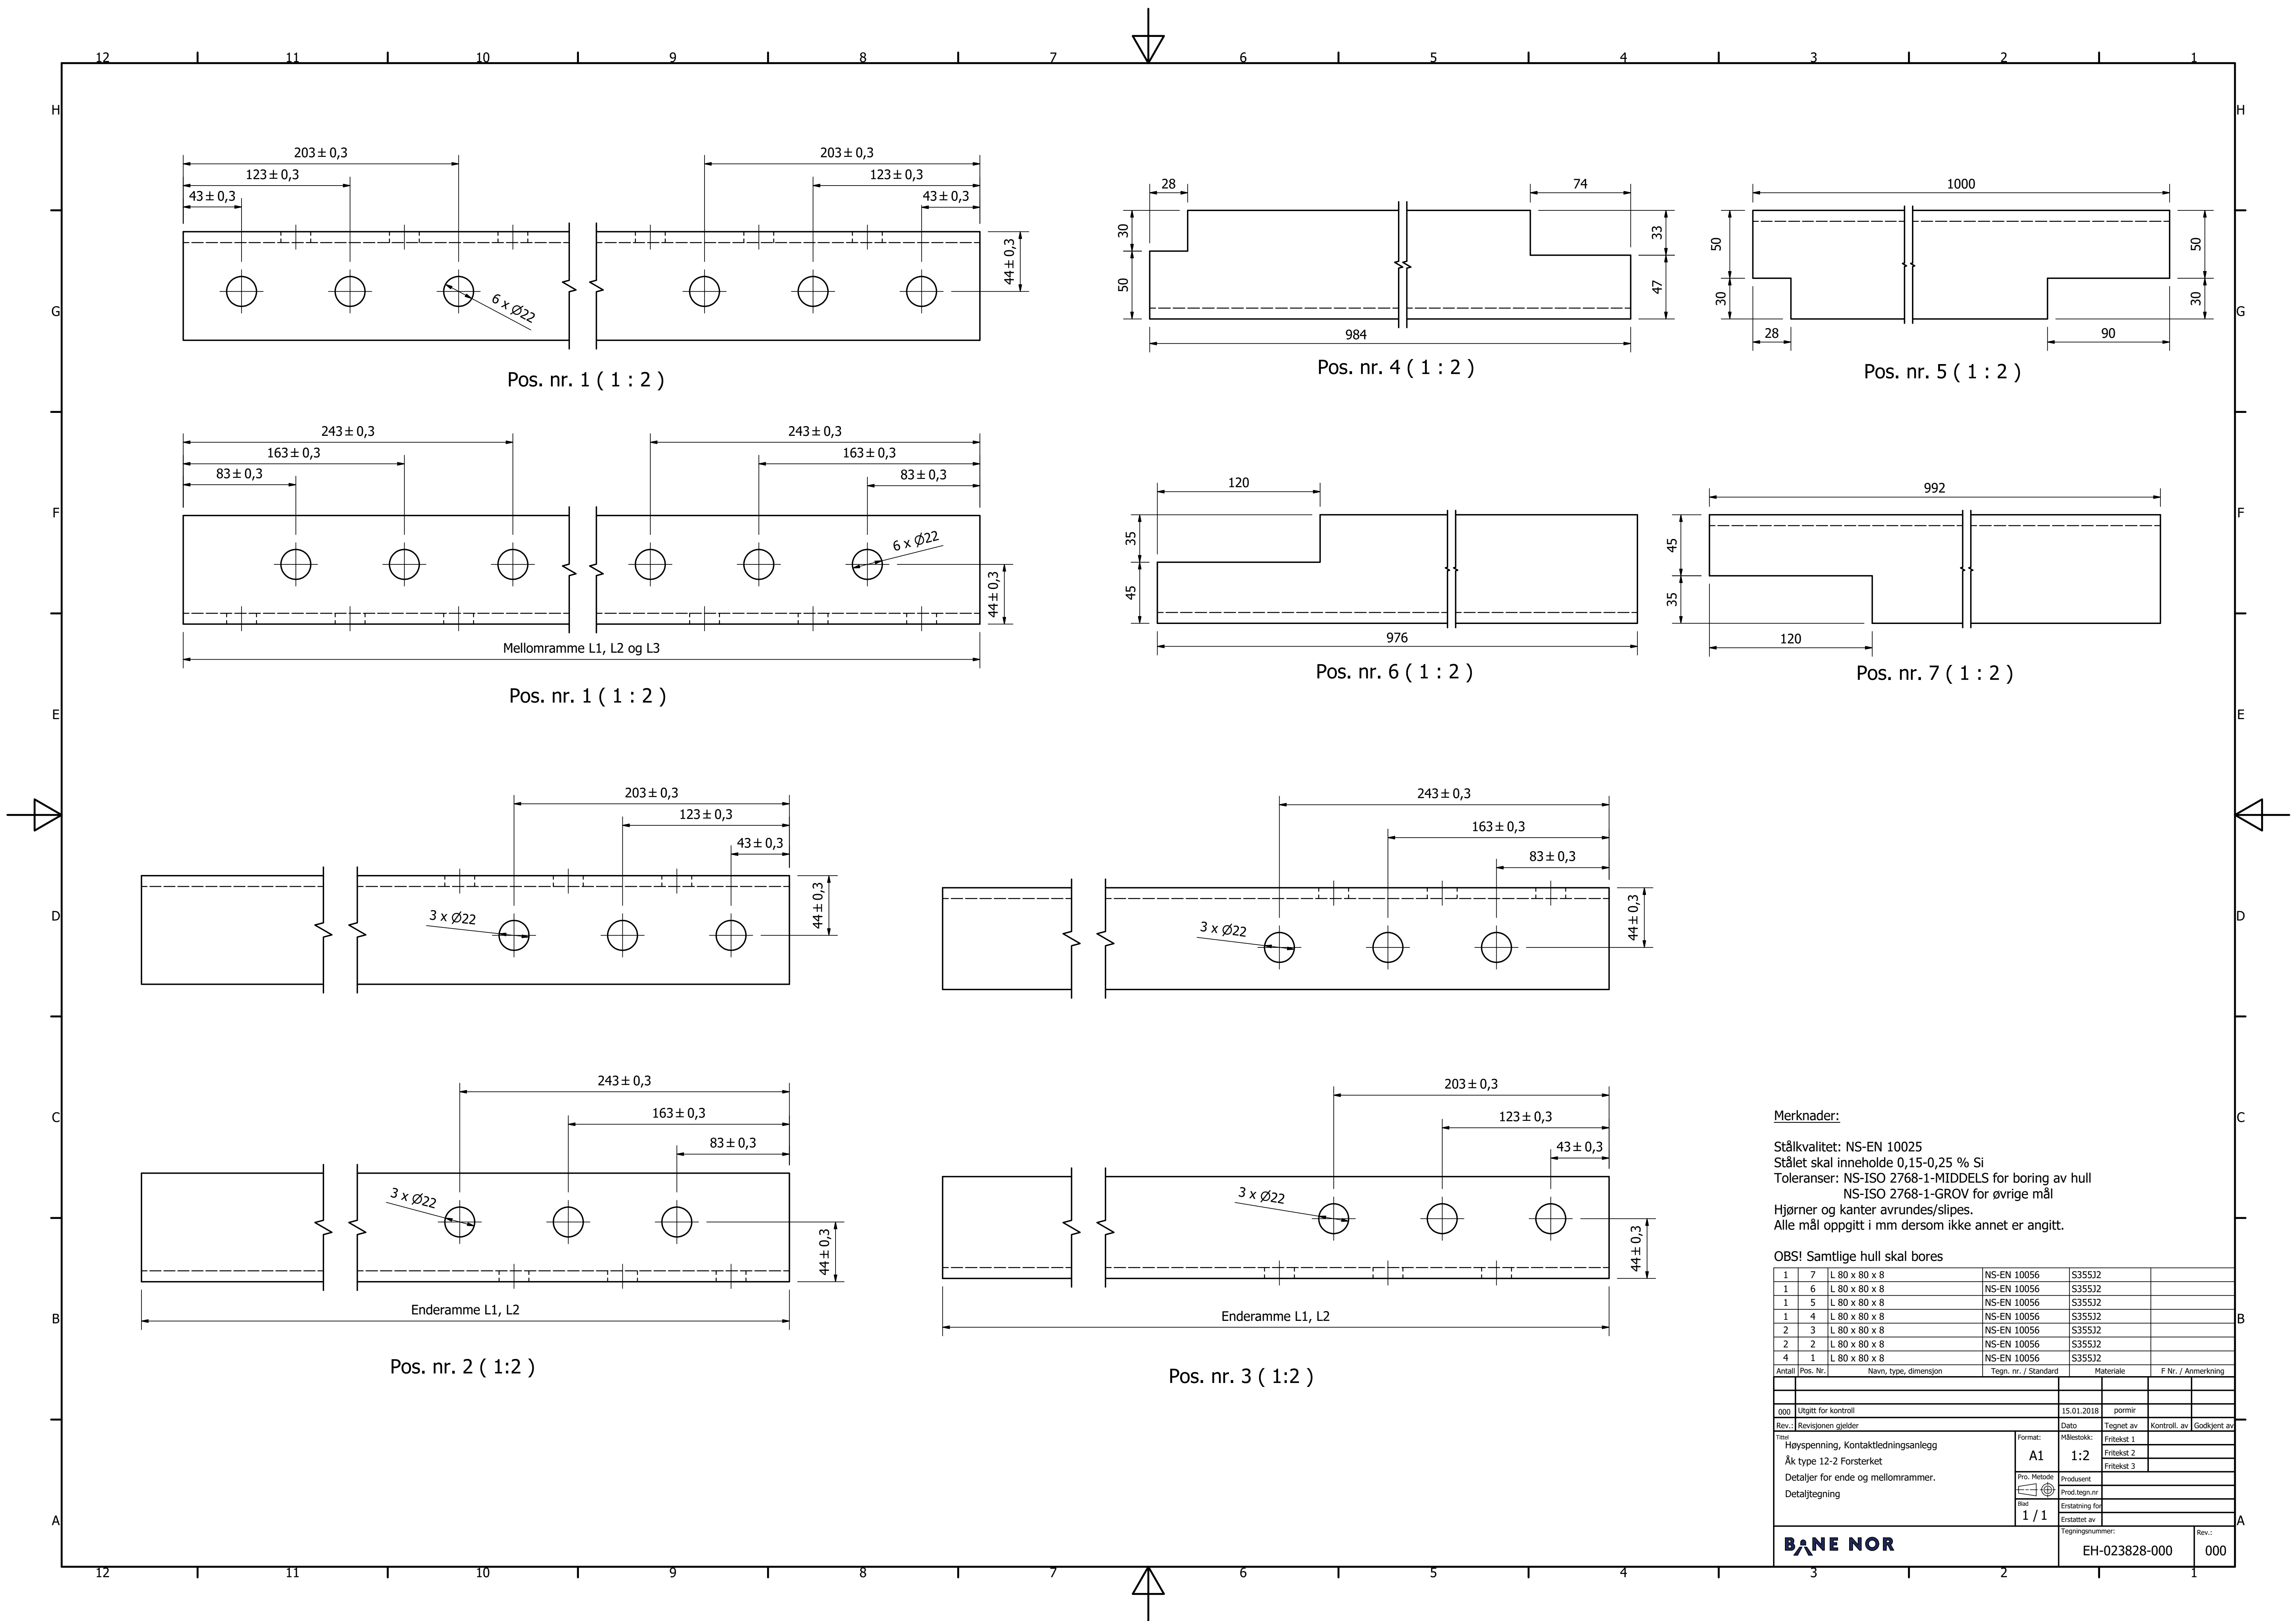

Merknader:

Stålkvalitet: NS-EN 10025
Stålet skal inneholde 0,15-0,25 % Si
Toleranser: NS-ISO 2768-1-MIDDELS for boring av hull
NS-ISO 2768-1-GROV for øvrige mål
Hjørner og kanter avrundes/slipes.
Alle mål oppgitt i mm dersom ikke annet er angitt.

OBS! Samtlige hull skal bores

1	7	L 80 x 80 x 8	NS-EN 10056	S355J2				
1	6	L 80 x 80 x 8	NS-EN 10056	S355J2				
1	5	L 80 x 80 x 8	NS-EN 10056	S355J2				
1	4	L 80 x 80 x 8	NS-EN 10056	S355J2				
2	3	L 80 x 80 x 8	NS-EN 10056	S355J2				
2	2	L 80 x 80 x 8	NS-EN 10056	S355J2				
4	1	L 80 x 80 x 8	NS-EN 10056	S355J2				
Antall	Pos. Nr.	Navn, type, dimensjon	Tegn. nr. / Standard	Materiale	F Nr. / Anmerknng			
000	Utgitt for kontroll			15.01.2018	pormir			
Rev.:	Revisjonen gjelder			Dato	Tegnet av	Kontroll. av		
Tittel Høyspenning, Kontaktledningsanlegg Åk type 12-2 Forsterket Detaljer for ende og mellomrammer. Detaljtegning				Format: A1	Målestokk: 1:2	Fritekst 1		
				Pro. Metode	Prod.tegn.nr	Fritekst 2		
				Bild	Ersättning for	Fritekst 3		
				1 / 1	Ersattlet av			
BANE NOR				Tegningsnummer: EH-023828-000		Rev.: 000		