


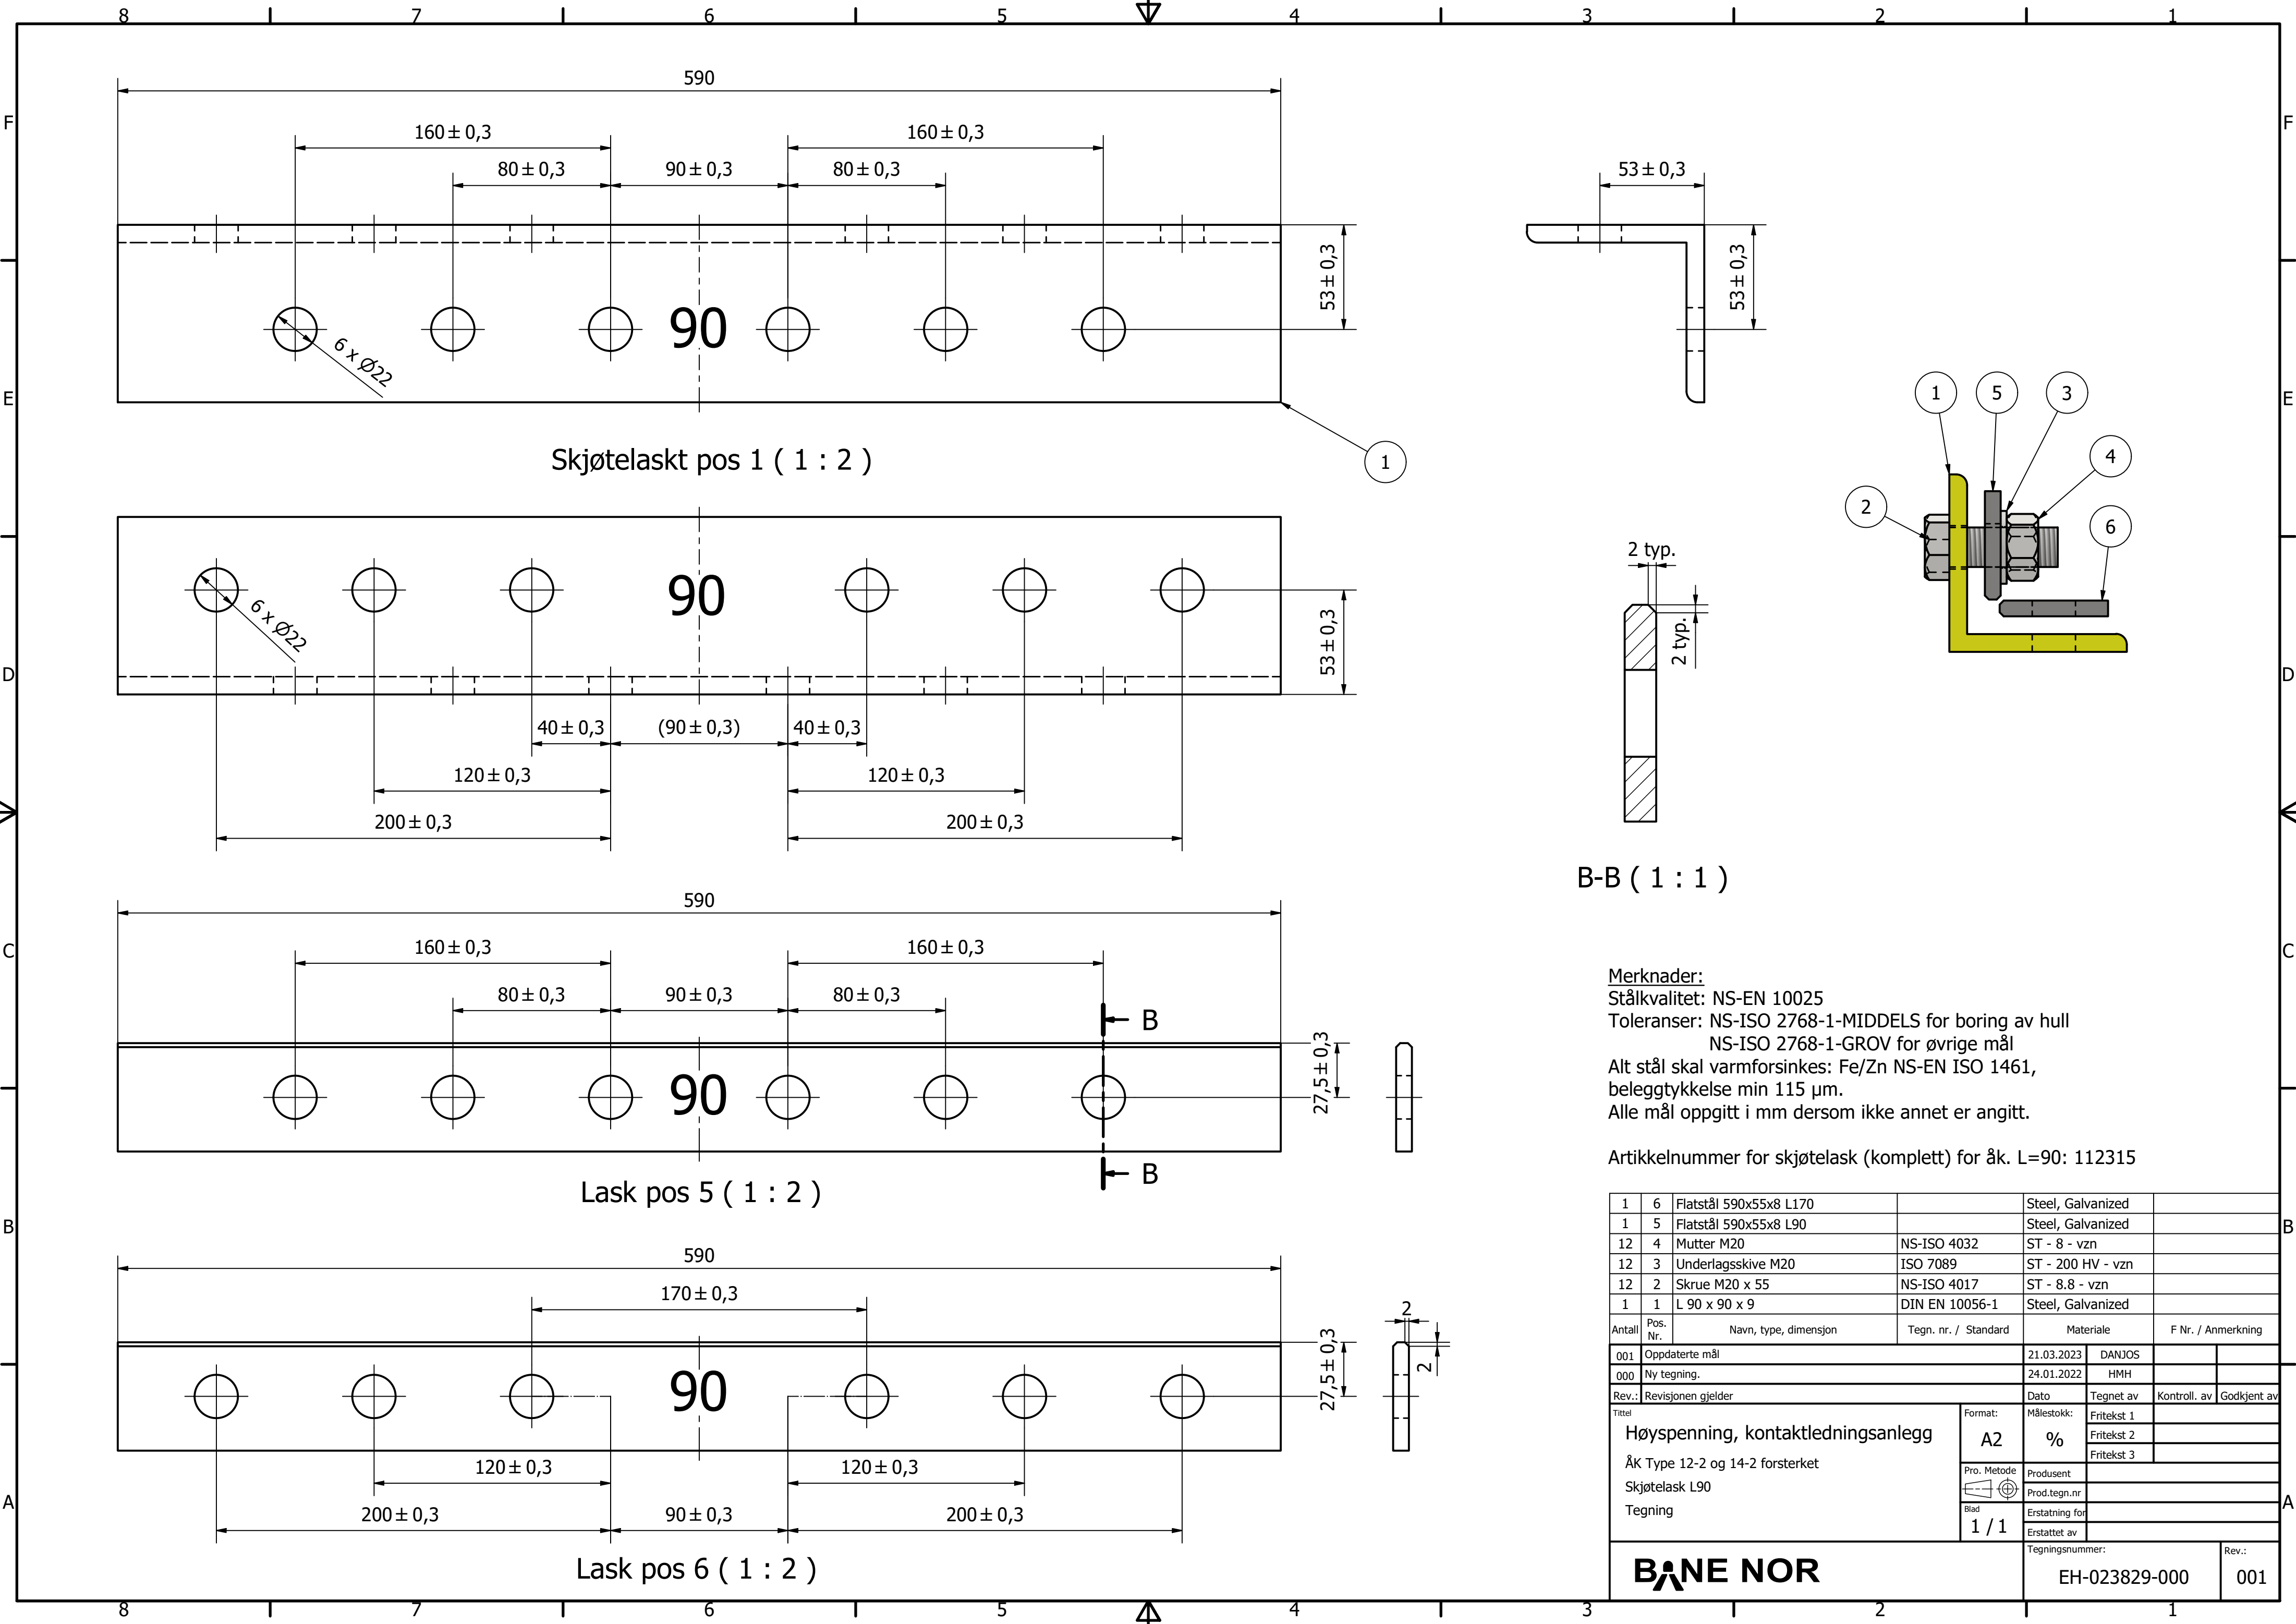

Skjøtelask pos 1 (1 : 2)


Lask pos 5 (1 : 2)

Lask pos 6 (1 : 2)

B-B (1 : 1)

Merknader:
Stålkvalitet: NS-EN 10025
Toleranser: NS-ISO 2768-1-MIDDELS for boring av hull
NS-ISO 2768-1-GROV for øvrige mål
Alt stål skal varmforsinkes: Fe/Zn NS-EN ISO 1461,
belegtykkelse min 115 µm.
Alle mål oppgitt i mm dersom ikke annet er angitt.

Artikkelnummer for skjøtelask (komplett) for åk. L=90: 112315

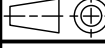1	6	Flatstål 590x55x8 L170		Steel, Galvanized			
1	5	Flatstål 590x55x8 L90		Steel, Galvanized			
12	4	Mutter M20	NS-ISO 4032	ST - 8 - vzn			
12	3	Underlagsskive M20	ISO 7089	ST - 200 HV - vzn			
12	2	Skrue M20 x 55	NS-ISO 4017	ST - 8.8 - vzn			
1	1	L 90 x 90 x 9	DIN EN 10056-1	Steel, Galvanized			
Antall	Pos. Nr.	Navn, type, dimensjon	Tegn. nr. / Standard	Materiale	F Nr. / Anmerkning		
001	Oppdaterte mål			21.03.2023	DANJOS		
000	Ny tegning.			24.01.2022	HMH		
Rev.: Revisjonen gjelder				Dato	Tegnet av	Kontroll. av	Godkjent av
Tittel Høyspenning, kontaktledningsanlegg Åk Type 12-2 og 14-2 forsterket Skjøtelask L90 Tegning				Format:	Målestokk:	Fritekst 1	
				A2	%	Fritekst 2	
						Fritekst 3	
					Pro. Metode	Produsent	
					Prod.tegn.nr		
				Blad	Erstatning for		
				1 / 1	Erstattet av		
BANE NOR				Tegningsnummer:		Rev.:	
				EH-023829-000		001	