


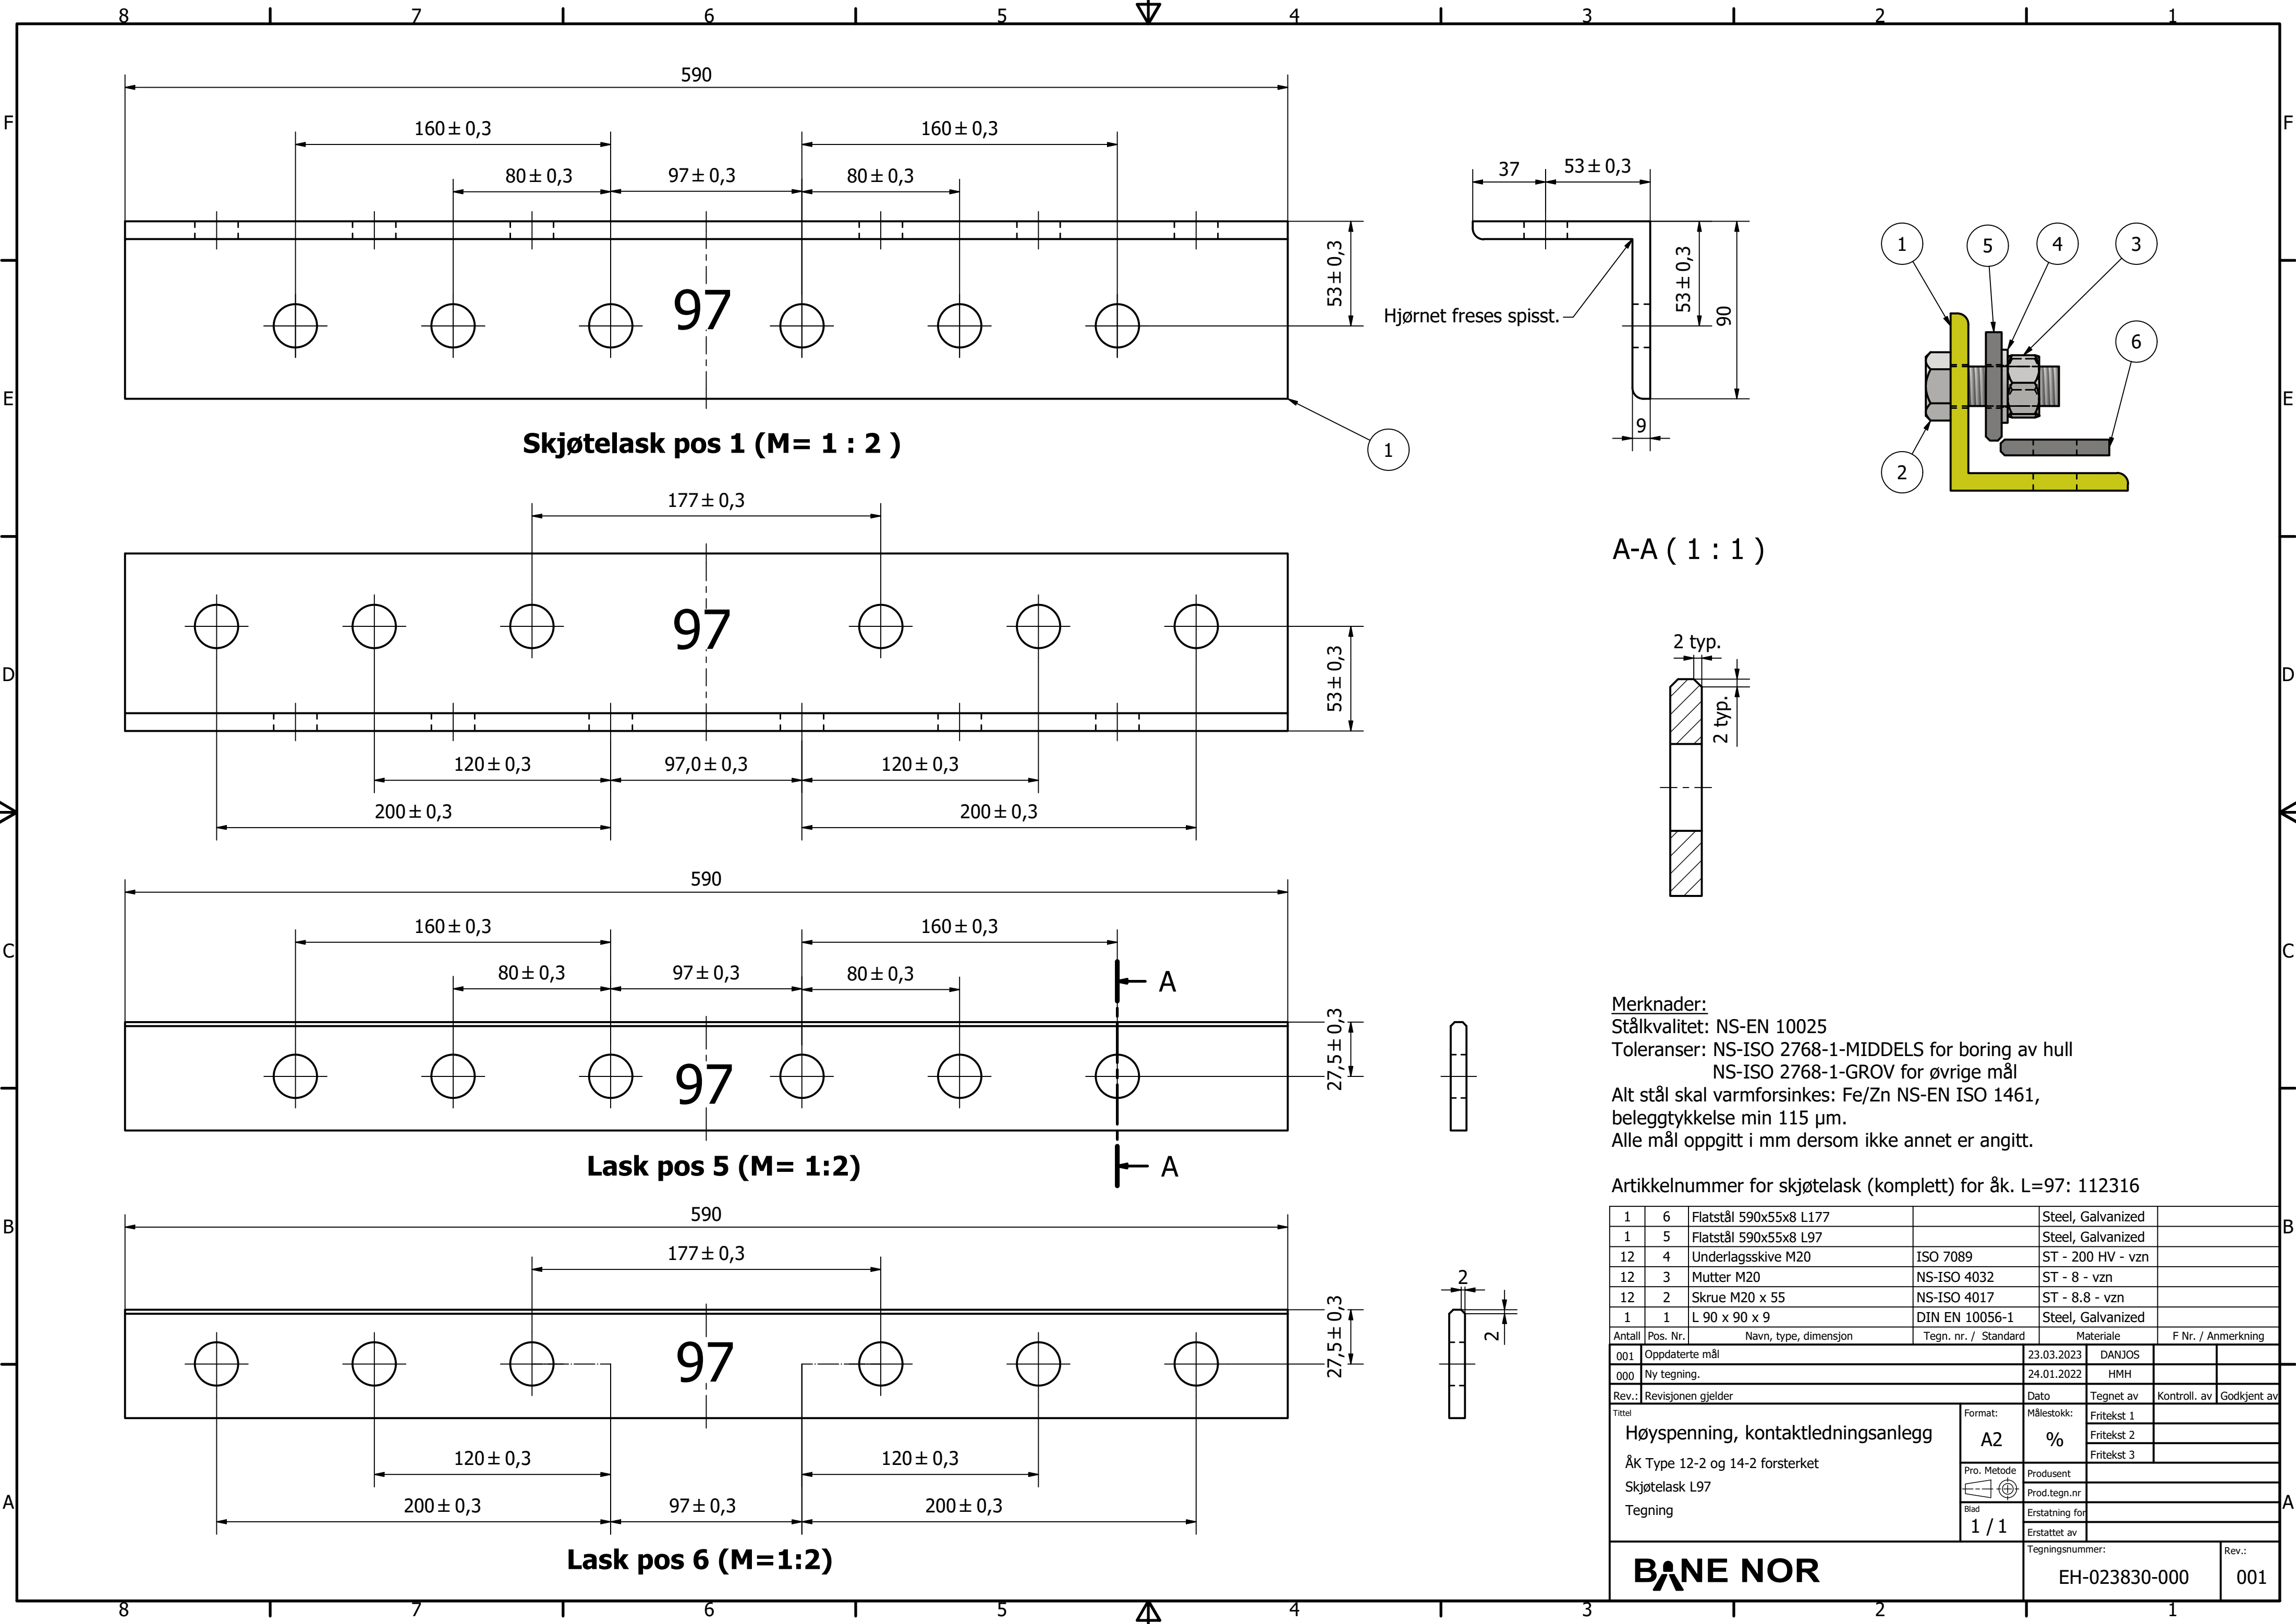

A-A (1 : 1)

Merknader:
Stålkvalitet: NS-EN 10025
Toleranser: NS-ISO 2768-1-MIDDELS for boring av hull
NS-ISO 2768-1-GROV for øvrige mål
Alt stål skal varmforzinks: Fe/Zn NS-EN ISO 1461,
beleggtykkelse min 115 µm.
Alle mål oppgitt i mm dersom ikke annet er angitt.

Artikkelnummer for skjøtelask (komplett) for åk. L=97: 112316

1	6	Flatstål 590x55x8 L177		Steel, Galvanized	
1	5	Flatstål 590x55x8 L97		Steel, Galvanized	
12	4	Underlagsskive M20	ISO 7089	ST - 200 HV - vzn	
12	3	Mutter M20	NS-ISO 4032	ST - 8 - vzn	
12	2	Skrue M20 x 55	NS-ISO 4017	ST - 8.8 - vzn	
1	1	L 90 x 90 x 9	DIN EN 10056-1	Steel, Galvanized	
Antall	Pos. Nr.	Navn, type, dimensjon	Tegn. nr. / Standard	Materiale	F Nr. / Anmerknning
001		Oppdaterte mål	23.03.2023	DANJOS	
000		Ny tegning.	24.01.2022	HMH	
Rev.:		Revisjonen gjelder	Dato	Tegnet av	Kontroll. av Godkjent av
Tittel Høyspenning, kontaktledningsanlegg Åk Type 12-2 og 14-2 forsterket Skjøtelask L97 Tegning			Format: A2	Målestokk: %	Fritekst 1
			Pro. Metode	Produsent	Fritekst 2
			Blad 1 / 1	Prod.tegn.nr	Fritekst 3
			Erstatning for	Erstattet av	
			Tegningsnummer:	Rev.:	
BANE NOR			EH-023830-000	001	