

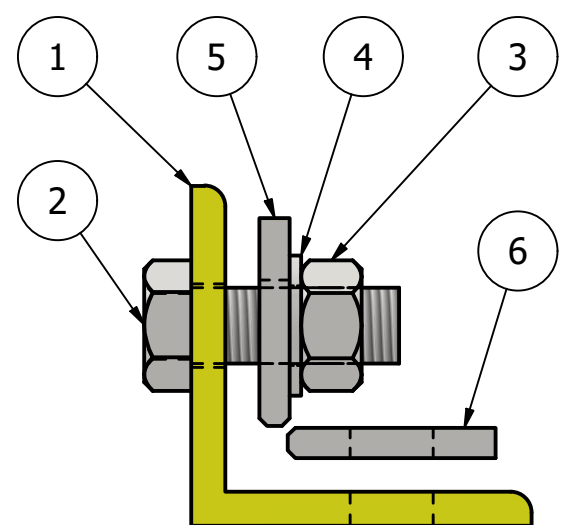
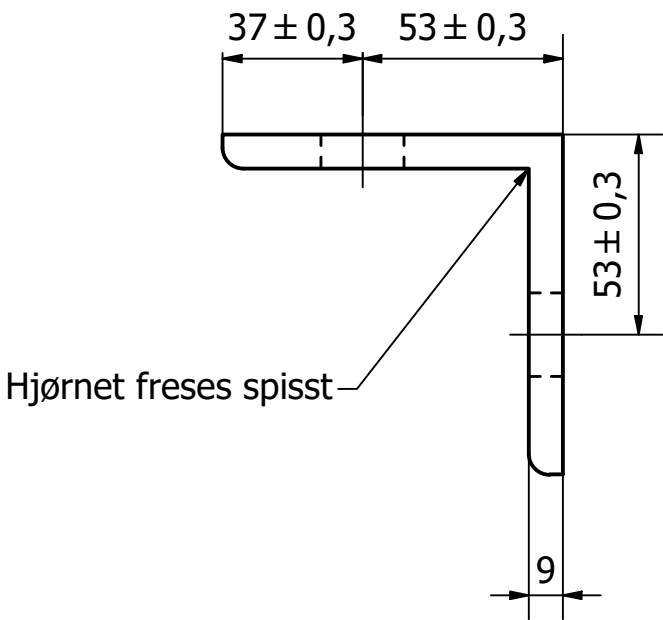


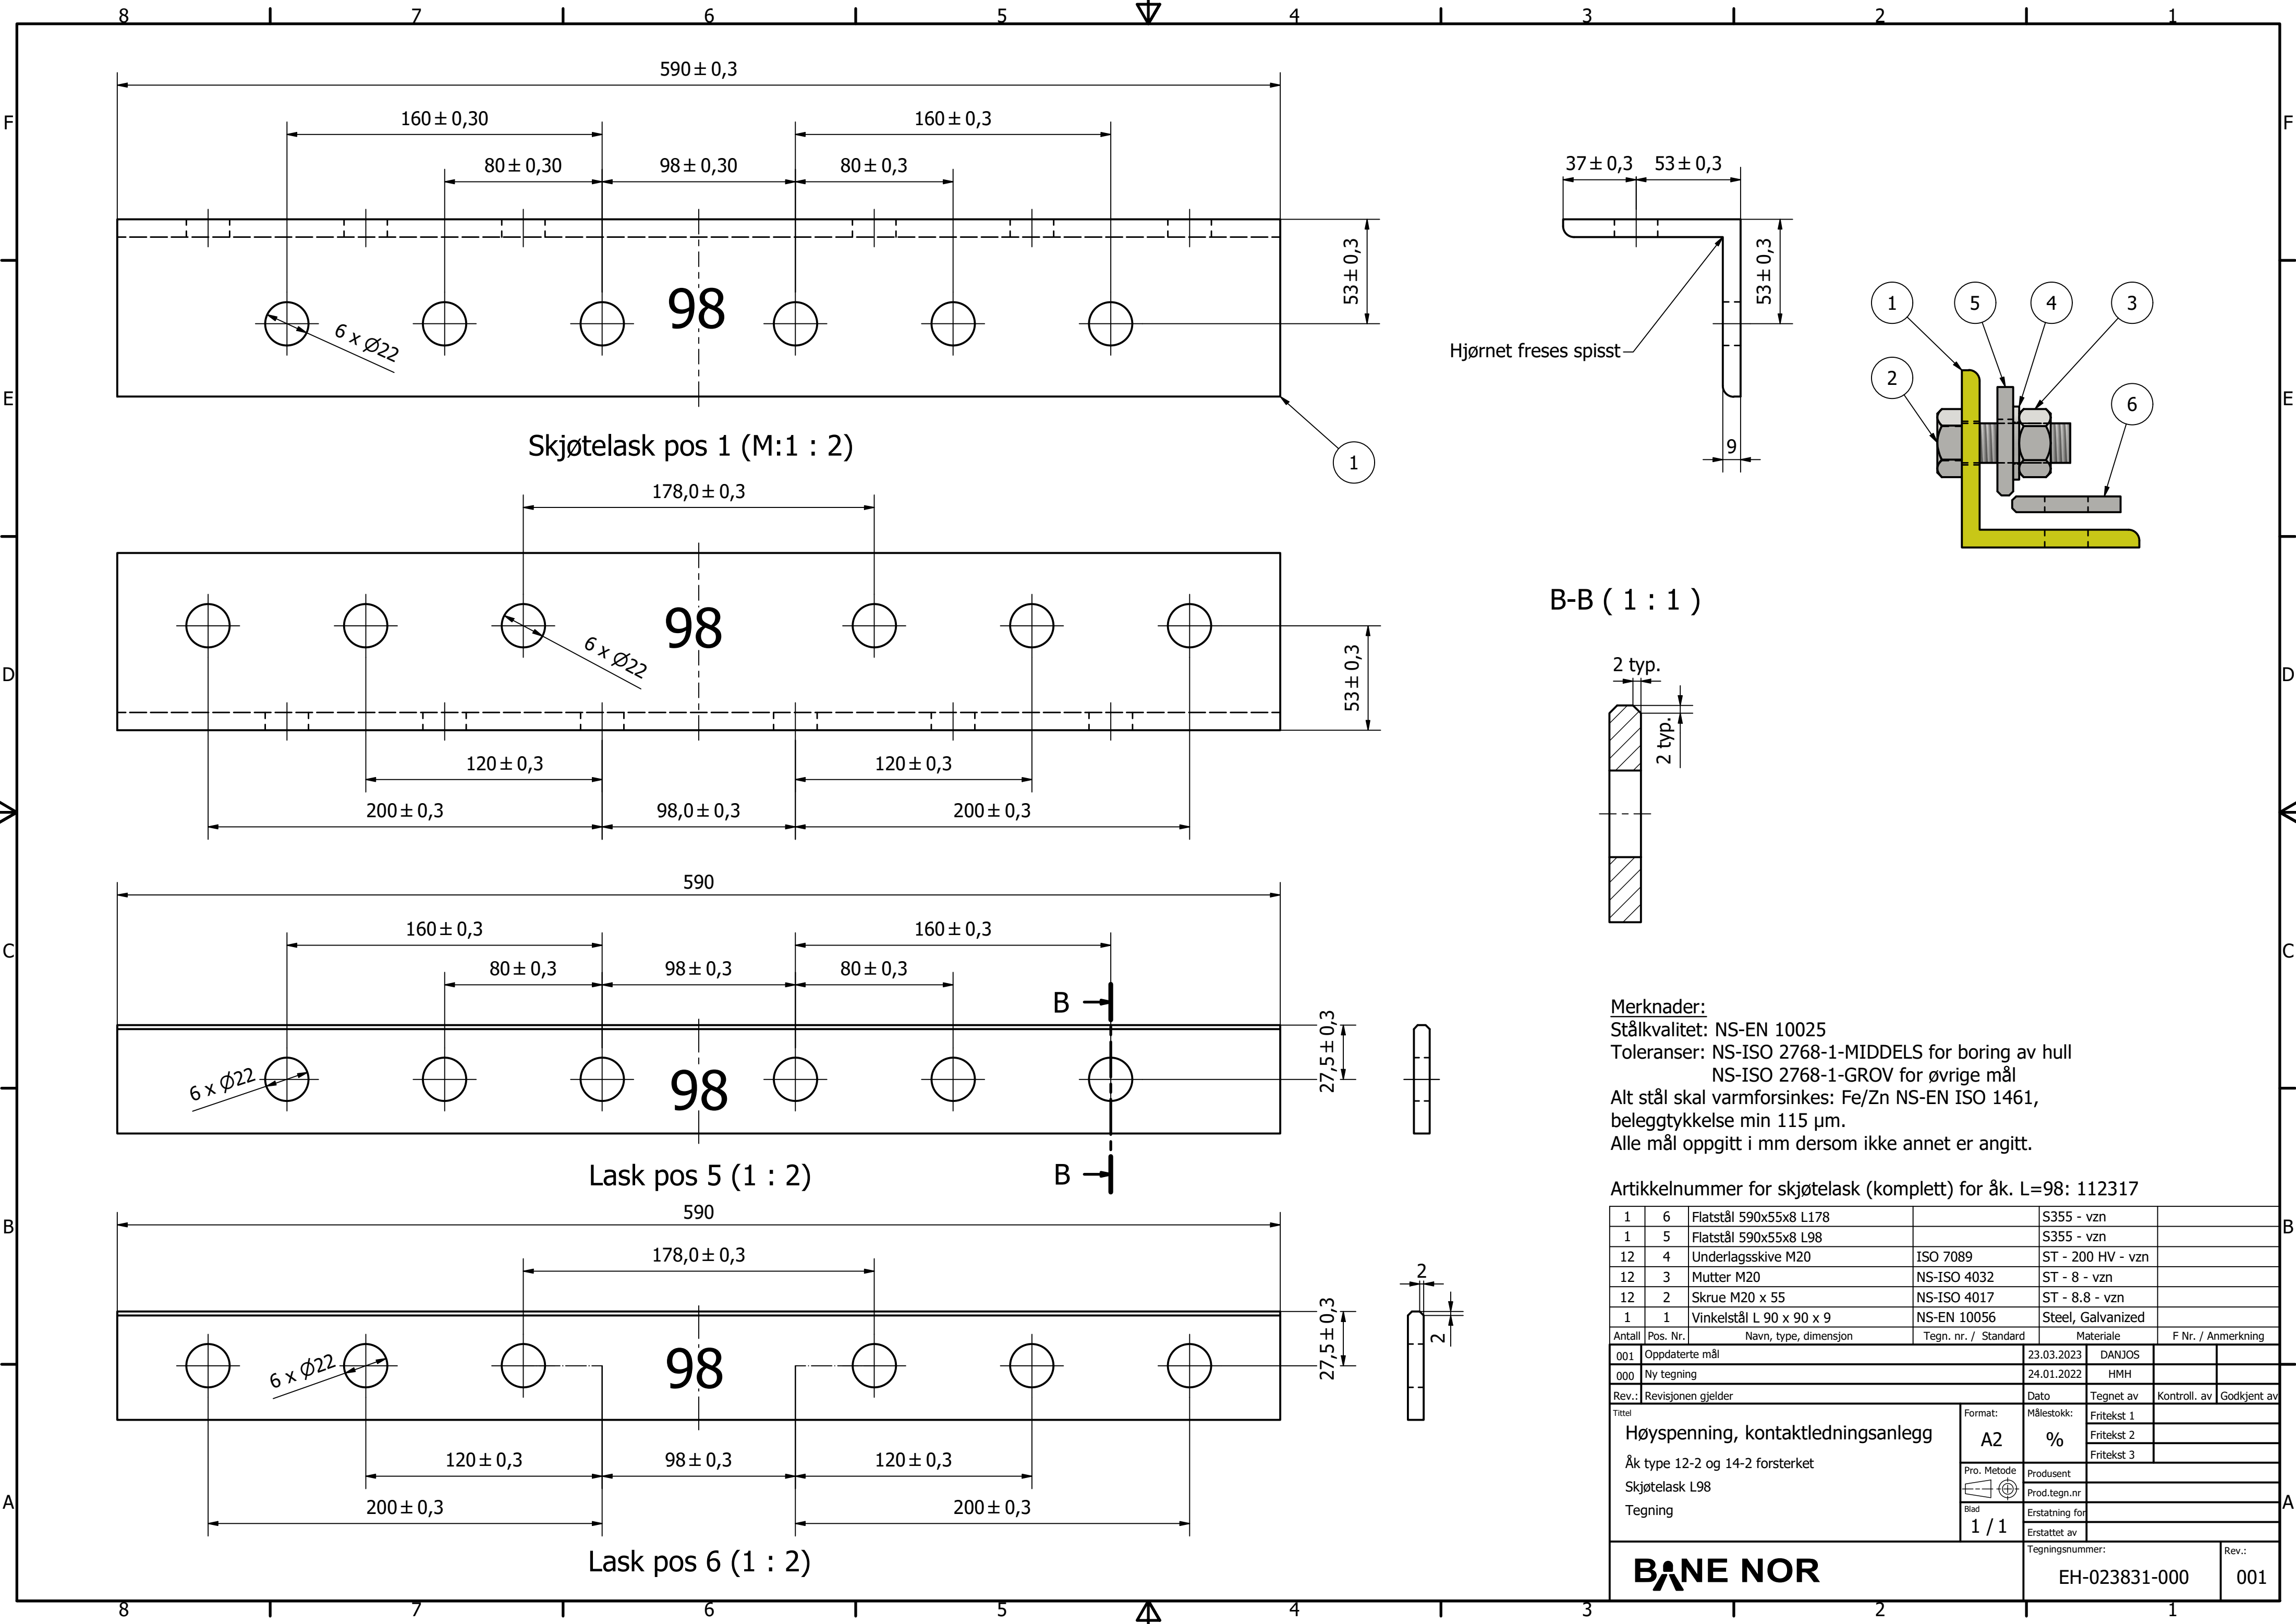


B-B (1 : 1)

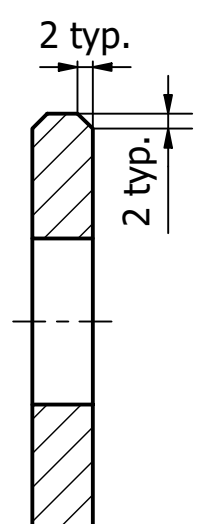

Merknader:
Stålkvalitet: NS-EN 10025
Toleranser: NS-ISO 2768-1-MIDDELS for boring av hull
NS-ISO 2768-1-GROV for øvrige mål
Alt stål skal varmforzinks: Fe/Zn NS-EN ISO 1461,
beleggtykkelse min 115 µm.
Alle mål oppgitt i mm dersom ikke annet er angitt.

Artikkelnummer for skjøtelask (komplett) for åk. L=98: 112317

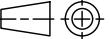1	6	Flatstål 590x55x8 L178		S355 - vzn				
1	5	Flatstål 590x55x8 L98		S355 - vzn				
12	4	Underlagsskive M20	ISO 7089	ST - 200 HV - vzn				
12	3	Mutter M20	NS-ISO 4032	ST - 8 - vzn				
12	2	Skrue M20 x 55	NS-ISO 4017	ST - 8.8 - vzn				
1	1	Vinkelstål L 90 x 90 x 9	NS-EN 10056	Steel, Galvanized				
Antall	Pos. Nr.	Navn, type, dimensjon	Tegn. nr. / Standard	Materiale	F Nr. / Anmerknning			
001	Oppdaterte mål			23.03.2023	DANJOS			
000	Ny tegning			24.01.2022	HMH			
Rev.:	Revisjonen gjelder			Dato	Tegnet av	Kontroll. av	Godkjent av	
Tittel Høyspenning, kontaktledningsanlegg Åk type 12-2 og 14-2 forsterket Skjøtelask L98 Tegning			Format:	Målestokk:	Fritekst 1			
			A2	%	Fritekst 2			
					Fritekst 3			
			Pro. Metode	Produsent				
				Prod.tegn.nr				
			Blad	Erstatning for				
			1 / 1					
			Erstattet av					
Tegningsnummer:				EH-023831-000		Rev.:		
						001		

BANE NOR