


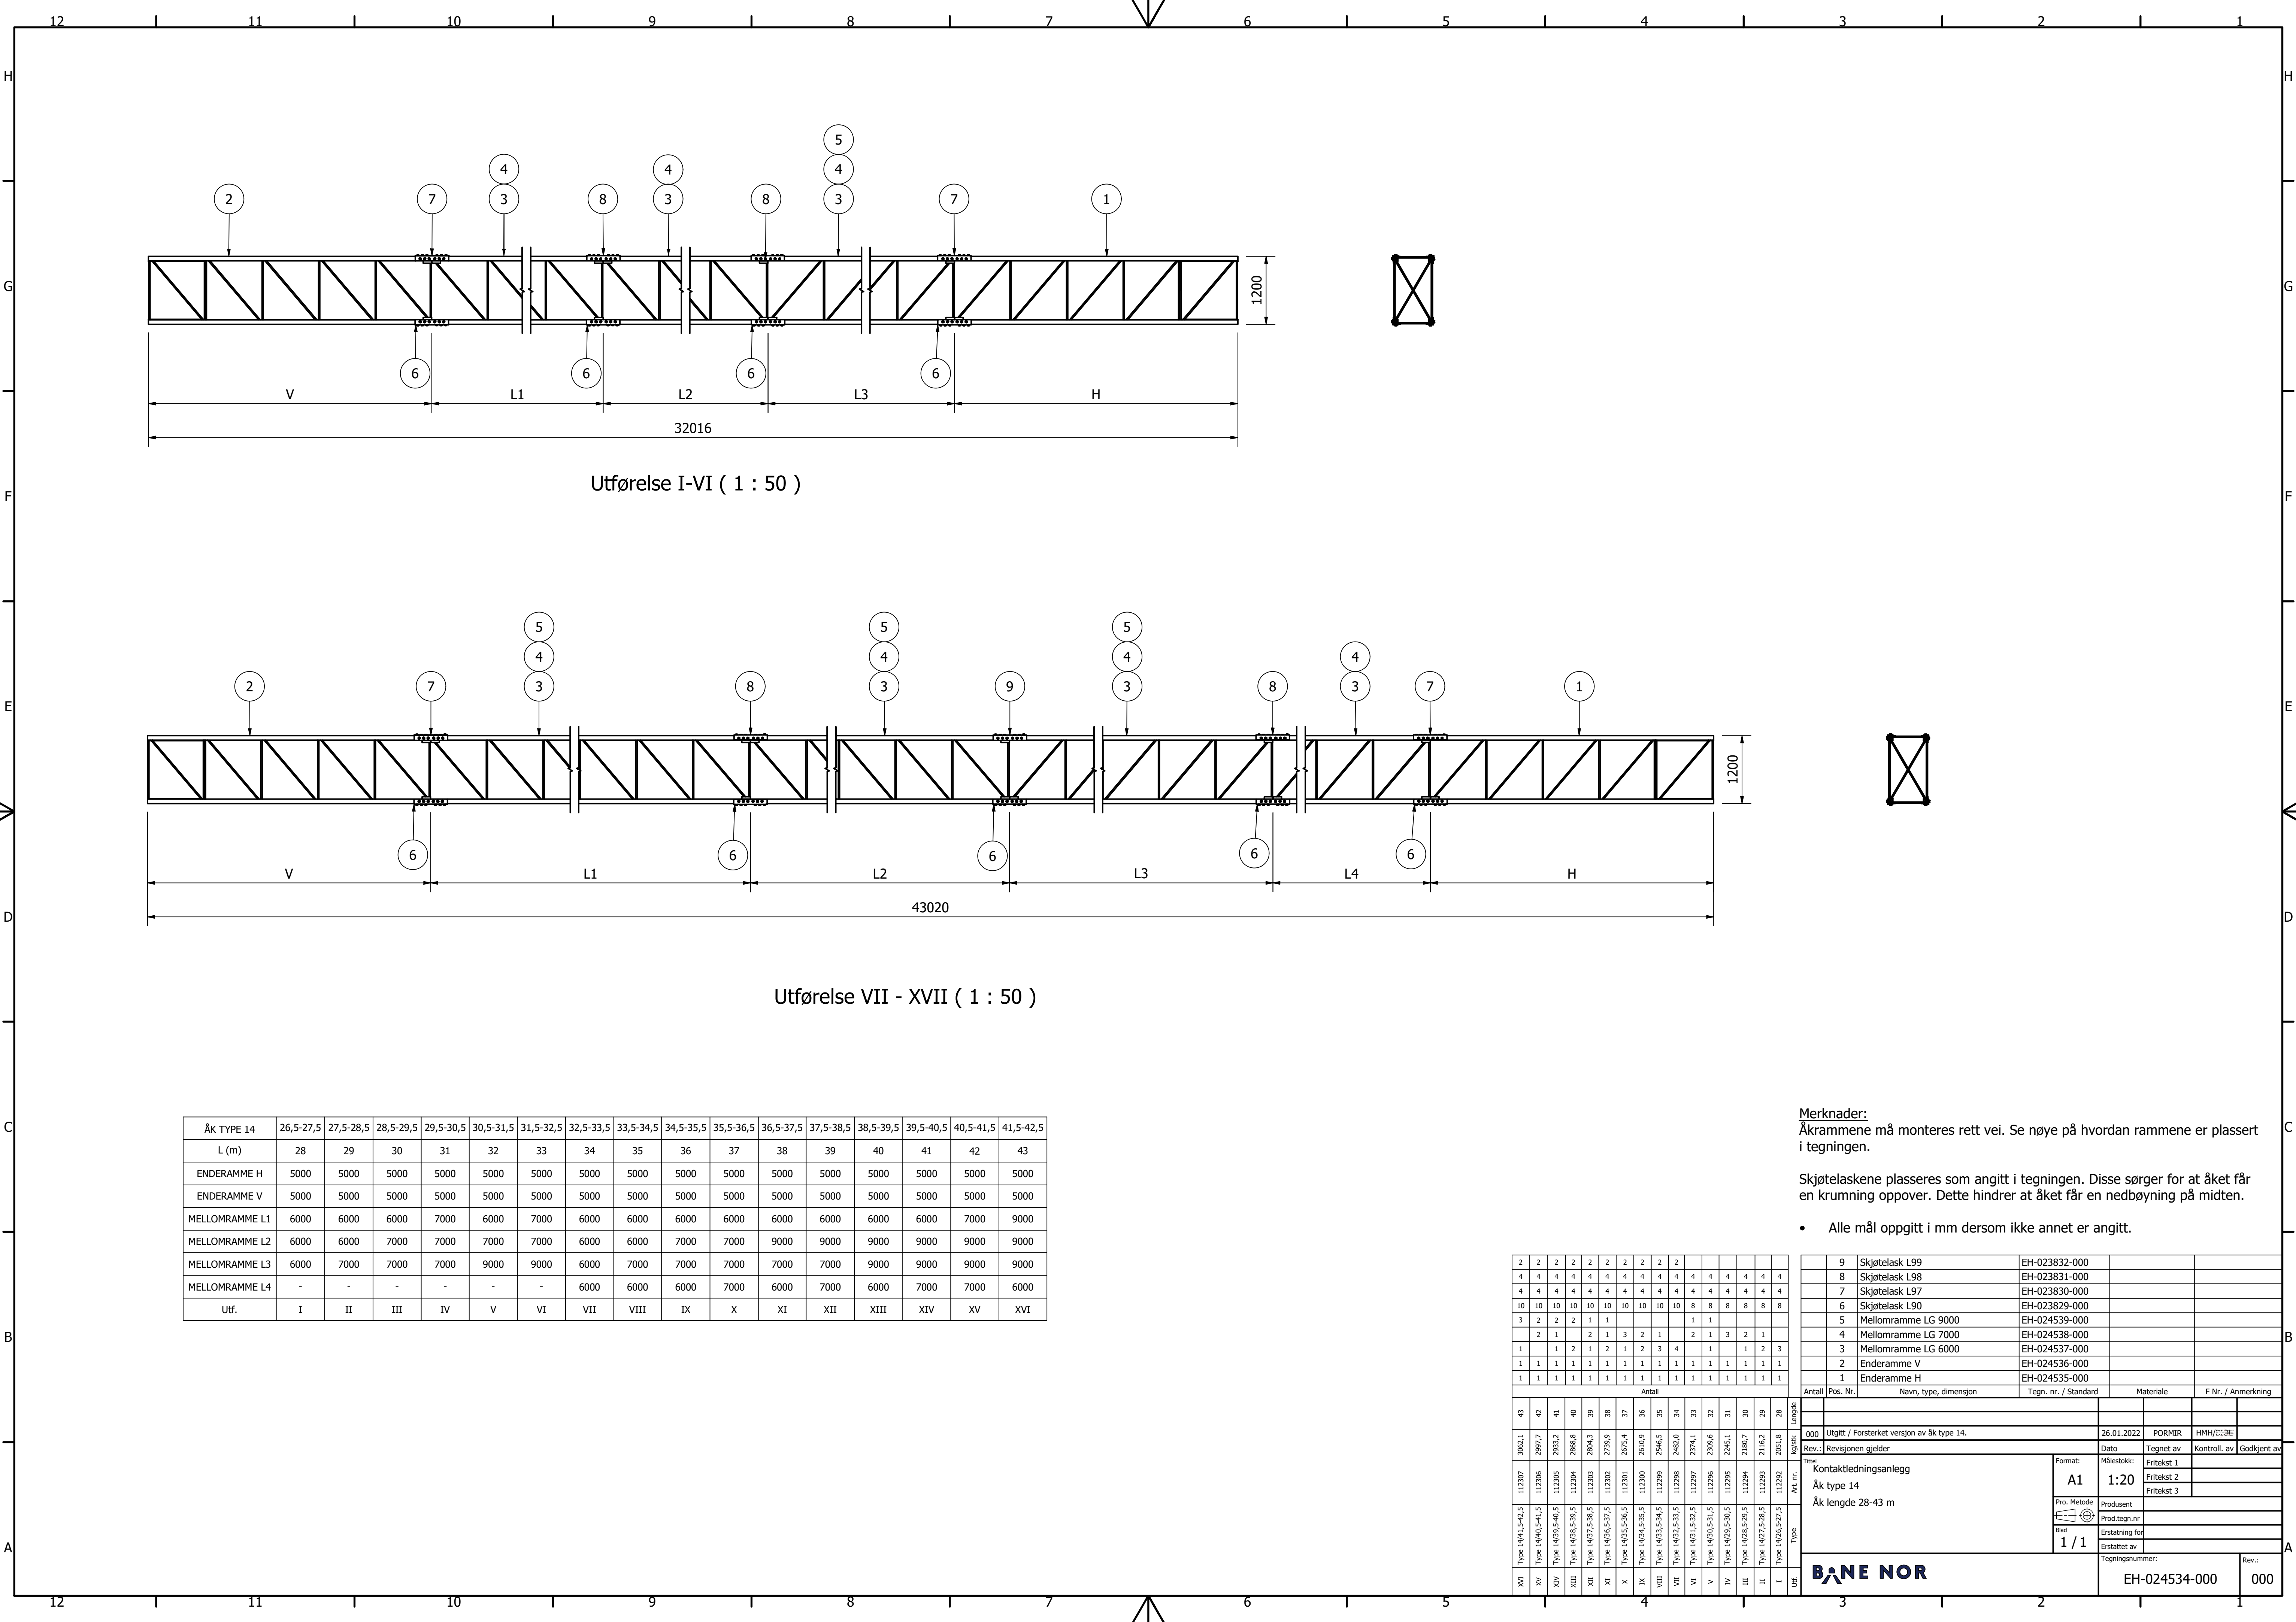

Merknader:
Åkrammene må monteres rett vei. Se nøye på hvordan rammene er plassert i tegningen.

Skjøtelaskene plasseres som angitt i tegningen. Disse sørger for at åket får en krumning oppover. Dette hindrer at åket får en nedbøyning på midten.

- Alle mål oppgitt i mm dersom ikke annet er angitt.

ÅK TYPE 14	26,5-27,5	27,5-28,5	28,5-29,5	29,5-30,5	30,5-31,5	31,5-32,5	32,5-33,5	33,5-34,5	34,5-35,5	35,5-36,5	36,5-37,5	37,5-38,5	38,5-39,5	39,5-40,5	40,5-41,5	41,5-42,5
L (m)	28	29	30	31	32	33	34	35	36	37	38	39	40	41	42	43
ENDERAMME H	5000	5000	5000	5000	5000	5000	5000	5000	5000	5000	5000	5000	5000	5000	5000	5000
ENDERAMME V	5000	5000	5000	5000	5000	5000	5000	5000	5000	5000	5000	5000	5000	5000	5000	5000
MELLOMRAMME L1	6000	6000	6000	7000	6000	7000	6000	6000	6000	6000	6000	6000	6000	6000	7000	9000
MELLOMRAMME L2	6000	6000	7000	7000	7000	7000	6000	6000	7000	7000	9000	9000	9000	9000	9000	9000
MELLOMRAMME L3	6000	7000	7000	7000	9000	9000	6000	7000	7000	7000	7000	9000	9000	9000	9000	9000
MELLOMRAMME L4	-	-	-	-	-	-	6000	6000	6000	7000	6000	7000	6000	7000	7000	6000
Utf.	I	II	III	IV	V	VI	VII	VIII	IX	X	XI	XII	XIII	XIV	XV	XVI

2	2	2	2	2	2	2	2	2	2								
4	4	4	4	4	4	4	4	4	4	4	4	4	4	4	4	4	
4	4	4	4	4	4	4	4	4	4	4	4	4	4	4	4	4	
10	10	10	10	10	10	10	10	10	10	8	8	8	8	8	8	8	
3	2	2	2	1	1	1	1	1	1	1	1	1	1	1	1	1	
2	1	1	2	1	3	2	1	2	1	3	2	1	3	2	1	1	
1	1	1	2	1	2	1	2	3	4	1	1	1	1	1	2	3	
1	1	1	1	1	1	1	1	1	1	1	1	1	1	1	1	1	
1	1	1	1	1	1	1	1	1	1	1	1	1	1	1	1	1	
Antall																	
Lengde																	
43	3062,1	11207	3062,1	43	2997,7	42	2997,7	41	2997,7	40	2997,7	39	2997,7	38	2997,7	37	2997,7
XVI	Type 14/41,5-42,5	11207	Type 14/40,5-41,5	11206	Type 14/39,5-40,5	11205	Type 14/38,5-39,5	11204	Type 14/37,5-38,5	11203	Type 14/36,5-37,5	11202	Type 14/35,5-36,5	11201	Type 14/34,5-35,5	11200	Type 14/33,5-34,5
XV	Type 14/32,5-33,5	11199	Type 14/31,5-32,5	11198	Type 14/30,5-31,5	11197	Type 14/29,5-30,5	11196	Type 14/28,5-29,5	11195	Type 14/27,5-28,5	11194	Type 14/26,5-27,5	11193	Type 14/25,5-26,5	11192	Type 14/24,5-25,5
XIV	Type 14/23,5-24,5	11191	Type 14/22,5-23,5	11190	Type 14/21,5-22,5	11189	Type 14/20,5-21,5	11188	Type 14/19,5-20,5	11187	Type 14/18,5-19,5	11186	Type 14/17,5-18,5	11185	Type 14/16,5-17,5	11184	Type 14/15,5-16,5
XIII	Type 14/14,5-15,5	11183	Type 14/13,5-14,5	11182	Type 14/12,5-13,5	11181	Type 14/11,5-12,5	11180	Type 14/10,5-11,5	11179	Type 14/9,5-10,5	11178	Type 14/8,5-9,5	11177	Type 14/7,5-8,5	11176	Type 14/6,5-7,5
XII	Type 14/5,5-6,5	11175	Type 14/4,5-5,5	11174	Type 14/3,5-4,5	11173	Type 14/2,5-3,5	11172	Type 14/1,5-2,5	11171	Type 14/0,5-1,5	11170	Type 14/0,5-1,5	11169	Type 14/0,5-1,5	11168	Type 14/0,5-1,5
XI	Type 14/0,5-1,5	11167	Type 14/0,5-1,5	11166	Type 14/0,5-1,5	11165	Type 14/0,5-1,5	11164	Type 14/0,5-1,5	11163	Type 14/0,5-1,5	11162	Type 14/0,5-1,5	11161	Type 14/0,5-1,5	11160	Type 14/0,5-1,5
X	Type 14/0,5-1,5	11159	Type 14/0,5-1,5	11158	Type 14/0,5-1,5	11157	Type 14/0,5-1,5	11156	Type 14/0,5-1,5	11155	Type 14/0,5-1,5	11154	Type 14/0,5-1,5	11153	Type 14/0,5-1,5	11152	Type 14/0,5-1,5
IX	Type 14/0,5-1,5	11151	Type 14/0,5-1,5	11150	Type 14/0,5-1,5	11149	Type 14/0,5-1,5	11148	Type 14/0,5-1,5	11147	Type 14/0,5-1,5	11146	Type 14/0,5-1,5	11145	Type 14/0,5-1,5	11144	Type 14/0,5-1,5
VIII	Type 14/0,5-1,5	11143	Type 14/0,5-1,5	11142	Type 14/0,5-1,5	11141	Type 14/0,5-1,5	11140	Type 14/0,5-1,5	11139	Type 14/0,5-1,5	11138	Type 14/0,5-1,5	11137	Type 14/0,5-1,5	11136	Type 14/0,5-1,5
VII	Type 14/0,5-1,5	11135	Type 14/0,5-1,5	11134	Type 14/0,5-1,5	11133	Type 14/0,5-1,5	11132	Type 14/0,5-1,5	11131	Type 14/0,5-1,5	11130	Type 14/0,5-1,5	11129	Type 14/0,5-1,5	11128	Type 14/0,5-1,5
VI	Type 14/0,5-1,5	11127	Type 14/0,5-1,5	11126	Type 14/0,5-1,5	11125	Type 14/0,5-1,5	11124	Type 14/0,5-1,5	11123	Type 14/0,5-1,5	11122	Type 14/0,5-1,5	11121	Type 14/0,5-1,5	11120	Type 14/0,5-1,5
V	Type 14/0,5-1,5	11119	Type 14/0,5-1,5	11118	Type 14/0,5-1,5	11117	Type 14/0,5-1,5	11116	Type 14/0,5-1,5	11115	Type 14/0,5-1,5	11114	Type 14/0,5-1,5	11113	Type 14/0,5-1,5	11112	Type 14/0,5-1,5
IV	Type 14/0,5-1,5	11111	Type 14/0,5-1,5	11110	Type 14/0,5-1,5	11109	Type 14/0,5-1,5	11108	Type 14/0,5-1,5	11107	Type 14/0,5-1,5	11106	Type 14/0,5-1,5	11105	Type 14/0,5-1,5	11104	Type 14/0,5-1,5
III	Type 14/0,5-1,5	11103	Type 14/0,5-1,5	11102	Type 14/0,5-1,5	11101	Type 14/0,5-1,5	11100	Type 14/0,5-1,5	11099	Type 14/0,5-1,5	11098	Type 14/0,5-1,5	11097	Type 14/0,5-1,5	11096	Type 14/0,5-1,5
II	Type 14/0,5-1,5	11095	Type 14/0,5-1,5	11094	Type 14/0,5-1,5	11093	Type 14/0,5-1,5	11092	Type 14/0,5-1,5	11091	Type 14/0,5-1,5	11090	Type 14/0,5-1,5	11089	Type 14/0,5-1,5	11088	Type 14/0,5-1,5
I	Type 14/0,5-1,5	11087	Type 14/0,5-1,5	11086	Type 14/0,5-1,5	11085	Type 14/0,5-1,5	11084	Type 14/0,5-1,5	11083	Type 14/0,5-1,5	11082	Type 14/0,5-1,5	11081	Type 14/0,5-1,5	11080	Type 14/0,5-1,5
Antall																	
Lengde																	
43	3062,1	11207	3062,1	43	2997,7	42	2997,7	41	2997,7	40	2997,7	39	2997,7	38	2997,7	37	2997,7
XVI	Type 14/41,5-42,5	11207	Type 14/40,5-41,5	11206	Type 14/39,5-40,5	11205	Type 14/38,5-39,5	11204	Type 14/37,5-38,5	11203	Type 14/36,5-37,5	11202	Type 14/35,5-36,5	11201	Type 14/34,5-35,5	11200	Type 14/33,5-34,5
XV	Type 14/32,5-33,5	11199	Type 14/31,5-32,5	11198	Type 14/30,5-31,5	11197	Type 14/29,5-30,5	11196	Type 14/28,5-29,5	11195	Type 14/27,5-28,5	11194	Type 14/26,5-27,5	11193	Type 14/25,5-26,5	11192	Type 14/24,5-25,5
XIV	Type 14/23,5-24,5	11191	Type 14/22,5-23,5	11190	Type 14/21,5-22,5	11189	Type 14/20,5-21,5	11188	Type 14/19,5-20,5	11187	Type 14/18,5-19,5	11186	Type 14/17,5-18,5	11185	Type 14/16,5-17,5	11184	Type 14/15,5-16,5
XIII	Type 14/14,5-15,5	11183	Type 14/13,5-14,5	11182	Type 14/12,5-13,5	11181	Type 14/11,5-12,5	11180	Type 14/10,5-11,5	11179	Type 14/9,5-10,5	11178	Type 14/8,5-9,5	11177	Type 14/7,5-8,5	11176	Type 14/6,5-7,5
XII	Type 14/5,5-6,5	11175	Type 14/4,5-5,5	11174	Type 14/3,5-4,5	11173	Type 14/2,5-3,5	11172	Type 14/1,5-2,5	11171	Type 14/0,5-1,5	11170	Type 14/0,5-1,5	11169	Type 14/0,5-1,5	11168	Type 14/0,5-1,5
XI	Type 14/0,5-1,5	11167	Type 14/0,5-1,5	11166	Type 14/0,5-1,5	11165	Type 14/0,5-1,5	11164	Type 14/0,5-1,5	11163	Type 14/0,5-1,5	11162	Type 14/0,5-1,5	11161	Type 14/0,5-1,5	11160	Type 14/0,5-1,5
X	Type 14/0,5-1,5	11159	Type 14/0,5-1,5	11158	Type 14/0,5-1,5	11157	Type 14/0,5-1,5	11156	Type 14/0,5-1,5	11155	Type 14/0,5-1,5	11154	Type 14/0,5-1,5	11153	Type 14/0,5-1,5	11152	Type 14/0,5-1,5
IX	Type 14/0,5-1,5	11151	Type 14/0,5-1,5	11150	Type 14/0,5-1,5	11149	Type 14/0,5-1,5	11148	Type 14/0,5-1,5	11147	Type 14/0,5-1,5	11146	Type 14/0,5-1,5	11145	Type 14/0,5-1,5	11144	Type 14/0,5-1,5
VIII	Type 14/0,5-1,5	11143	Type 14/0,5-1,5	11142	Type 14/0,5-1,5	11141	Type 14/0,5-1,5	11140	Type 14/0,5-1,5	11139	Type 14/0,5-1,5	11138	Type 14/0,5-1,5	11137	Type 14/0,5-1,5	11136	Type 14/0,5-1,5
VII	Type 14/0,5-1,5	11135	Type 14/0,5-1,5	11134	Type 14/0,5-1,5	11133	Type 14/0,5-1,5	11132	Type 14/0,5-1,5	11131	Type 14/0,5-1,5	11130	Type 14/0,5-1,5	11129	Type 14/0,5-1,5	11128	Type 14/0,5-1,5
VI	Type 14/0,5-1,5	11127	Type 14/0,5-1,5	11126	Type 14/0,5-1,5	11125	Type 14/0,5-1,5	11124	Type 14/0,5-1,5	11123	Type 14/0,5-1,5	11122	Type 14/0,5-1,5	11121	Type 14/0,5-1,5	11120	Type 14/0,5-1,5
V	Type 14/0,5-1,5	11119	Type 14/0,5-1,5	11118	Type 14/0,5-1,5	11117	Type 14/0,5-1,5	11116	Type 14/0,5-1,5	11115	Type 14/0,5-1,5	11114	Type 14/0,5-1,5	11113	Type 14/0,5-1,5	11112	Type 14/0,5-1,5
IV	Type 14/0,5-1,5	11111	Type 14/0,5-1,5	11110	Type 14/0,5-1,5	11109	Type 14/0,5-1,5	11108	Type 14/0,5-1,5	11107	Type 14/0,5-1,5	11106	Type 14/0,5-1,5	11105	Type 14/0,5-1,5	11104	Type 14/0,5-1,5
III	Type 14/0,5-1,5	11103	Type 14/0,5-1,5	11102	Type 14/0,5-1,5	11101	Type 14/0,5-1,5	11100	Type 14/0,5-1,5	11099	Type 14/0,5-1,5	11098	Type 14/0,5-1,5	11097	Type 14/0,5-1,5	11096	Type 14/0,5-1,5
II	Type 14/0,5-1,5	11095	Type 14/0,5-1,5	11094	Type 14/0,5-1,5	11093	Type 14/0,5-1,5	11092	Type 14/0,5-1,5	11091	Type 14/0,5-1,5	11090	Type 14/0,5-1,5	11089	Type 14/0,5-1,5	11088	Type 14/0,5-1,5
I	Type 14/0,5-1,5	11087	Type 14/0,5-1,5	11086	Type 14/0,5-1,5	11085	Type 14/0,5-1,5	11084	Type 14/0,5-1,5	11083	Type 14/0,5-1,5	11082	Type 14/0,5-1,5	11081	Type 14/0,5-1,5	11080	Type 14/0,5-1,5
Antall																	
Lengde																	
43	3062,1	11207	3062,1	43	2997,7	42	2997,7	41	2997,7	40	2997,7	39	2997,7	38	2997,7	37	2997,7
XVI	Type 14/41,5-42,5	11207	Type 14/40,5-41,5	11206	Type 14/39,5-40,5	11205	Type 14/38,5-39,5	11204	Type 14/37,5-38,5	11203	Type 14/36,5-37,5	11202	Type 14/35,5-36,5	11201	Type 14/34,5-35,5	11200	Type 14/33,5-34,5
XV	Type 14/32,5-33,5	11199	Type 14/31,5-32,5	11198	Type 14/30,5-31,5	11197	Type 14/29,5-30,5	11196	Type 14/28,5-29,5	11195	Type 14/27,5-28,5	11194	Type 14/26,5-27,5	11193	Type 14/25,5-26,5	11192	Type 14/24,5-25,5
XIV	Type 14/23,5-24,5	11191	Type 14/22,5-23,5	11190	Type 14/21,5-22,5	11189	Type 14/20,5-21,5	11188	Type 14/19,5-20,5	11187	Type 14/18,5-19,5	11186					