


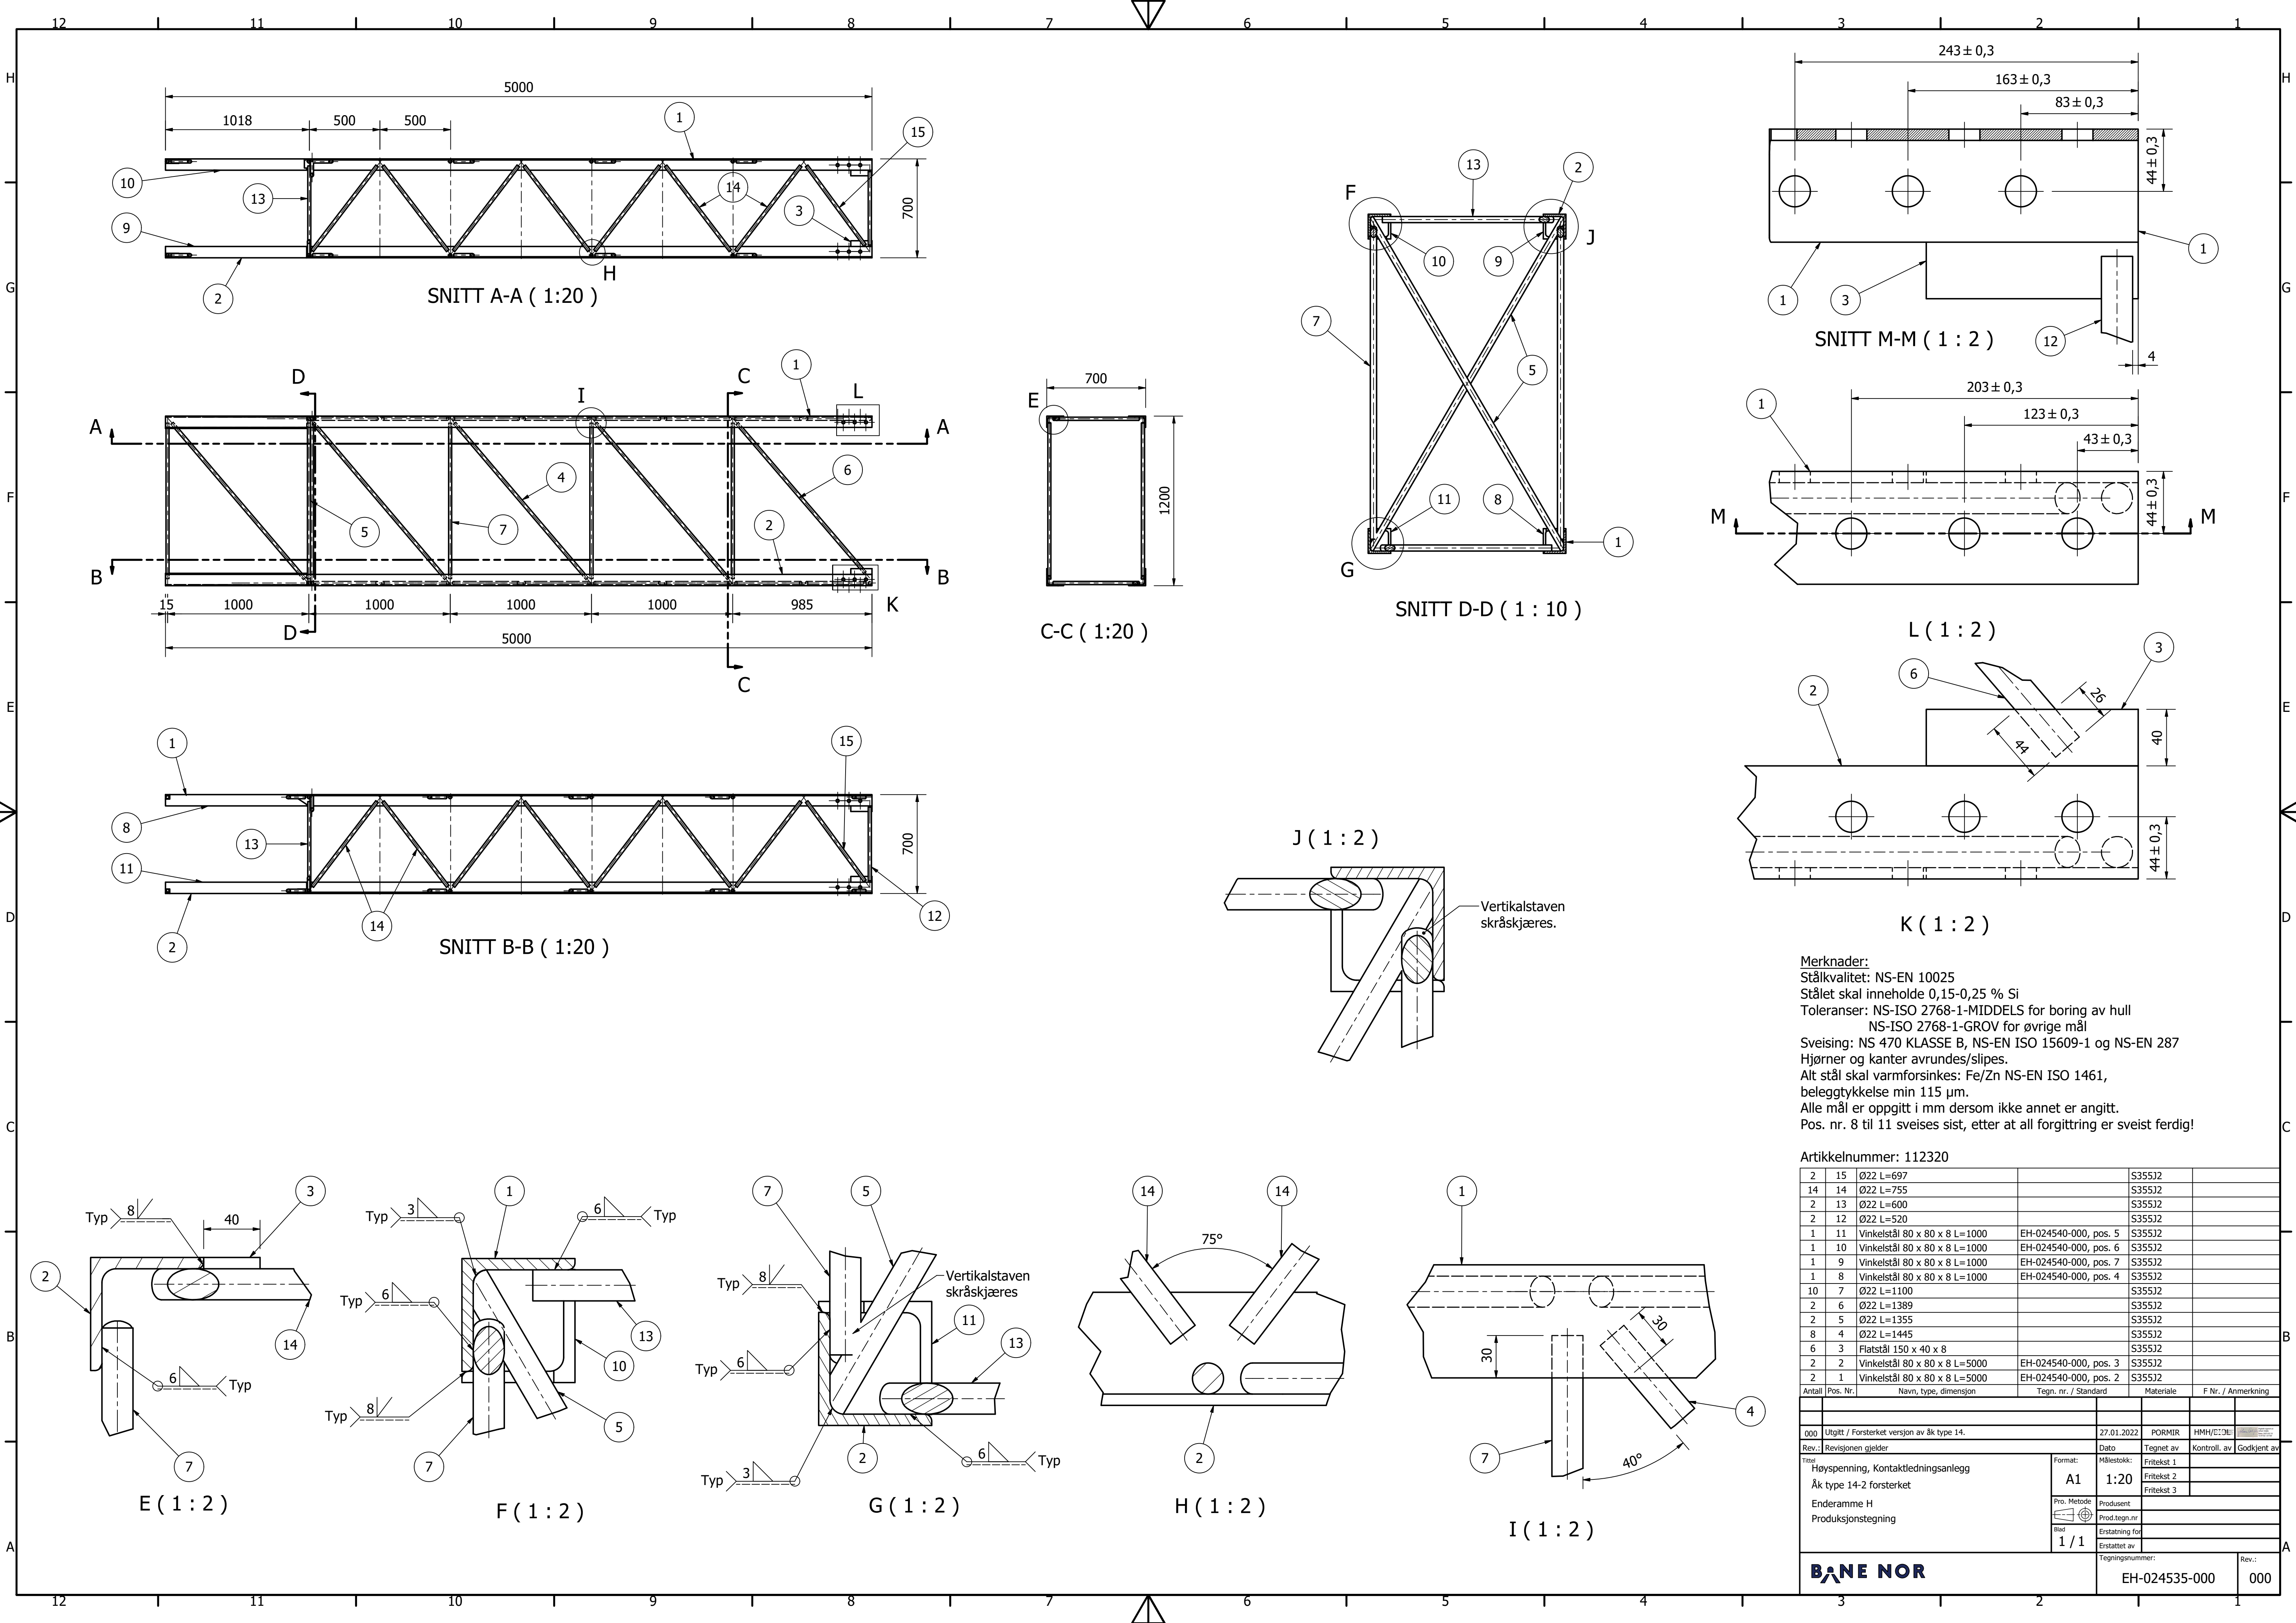

Merknader:
Stålkvalitet: NS-EN 10025
Stålet skal inneholde 0,15-0,25 % Si
Toleranser: NS-ISO 2768-1-MIDDELS for boring av hull
NS-ISO 2768-1-GROV for øvrige mål
Sveising: NS 470 KLASSE B, NS-EN ISO 15609-1 og NS-EN 287
Hjørner og kanter avrundes/slipes.
Alt stål skal varmforsinkes: Fe/Zn NS-EN ISO 1461,
beleggtykkelse min 115 µm.
Alle mål er oppgitt i mm dersom ikke annet er angitt.
Pos. nr. 8 til 11 sveises sist, etter at all forgittning er sveist ferdig!

Artikkelnummer: 112320									
2	15	Ø22 L=697					S355J2		
14	14	Ø22 L=755					S355J2		
2	13	Ø22 L=600					S355J2		
2	12	Ø22 L=520					S355J2		
1	11	Vinkelstål 80 x 80 x 8 L=1000			EH-024540-000, pos. 5		S355J2		
1	10	Vinkelstål 80 x 80 x 8 L=1000			EH-024540-000, pos. 6		S355J2		
1	9	Vinkelstål 80 x 80 x 8 L=1000			EH-024540-000, pos. 7		S355J2		
1	8	Vinkelstål 80 x 80 x 8 L=1000			EH-024540-000, pos. 4		S355J2		
10	7	Ø22 L=1100					S355J2		
2	6	Ø22 L=1389					S355J2		
2	5	Ø22 L=1355					S355J2		
8	4	Ø22 L=1445					S355J2		
6	3	Flatstål 150 x 40 x 8					S355J2		
2	2	Vinkelstål 80 x 80 x 8 L=5000			EH-024540-000, pos. 3		S355J2		
2	1	Vinkelstål 80 x 80 x 8 L=5000			EH-024540-000, pos. 2		S355J2		
Antall	Pos. Nr.	Navn, type, dimensjon			Tegn. nr. / Standard		Materiale	F. Nr. / Anmerkning	
000 Utgitt / Forsterket versjon av Åk type 14.						27.01.2022	PORMIR	HMH/ETD	
Rev.: Revisjonen gjelder						Dato	Tegnet av	Kontroll. av	Godkjent av
Tegn.: Høyspenning, Kontaktledningsanlegg Åk type 14-2 forsterket Enderamme H Produksjonstegning						Format: A1	Målestokk:	Fritekst 1	
								Fritekst 2	
								Fritekst 3	
Pro. Metode						Prod.tegn.nr	Produzent		
Blad						1 / 1	Erstatning for		
BANE NOR						Tegningsnummer:		EH-024535-000	
								Rev.:	