

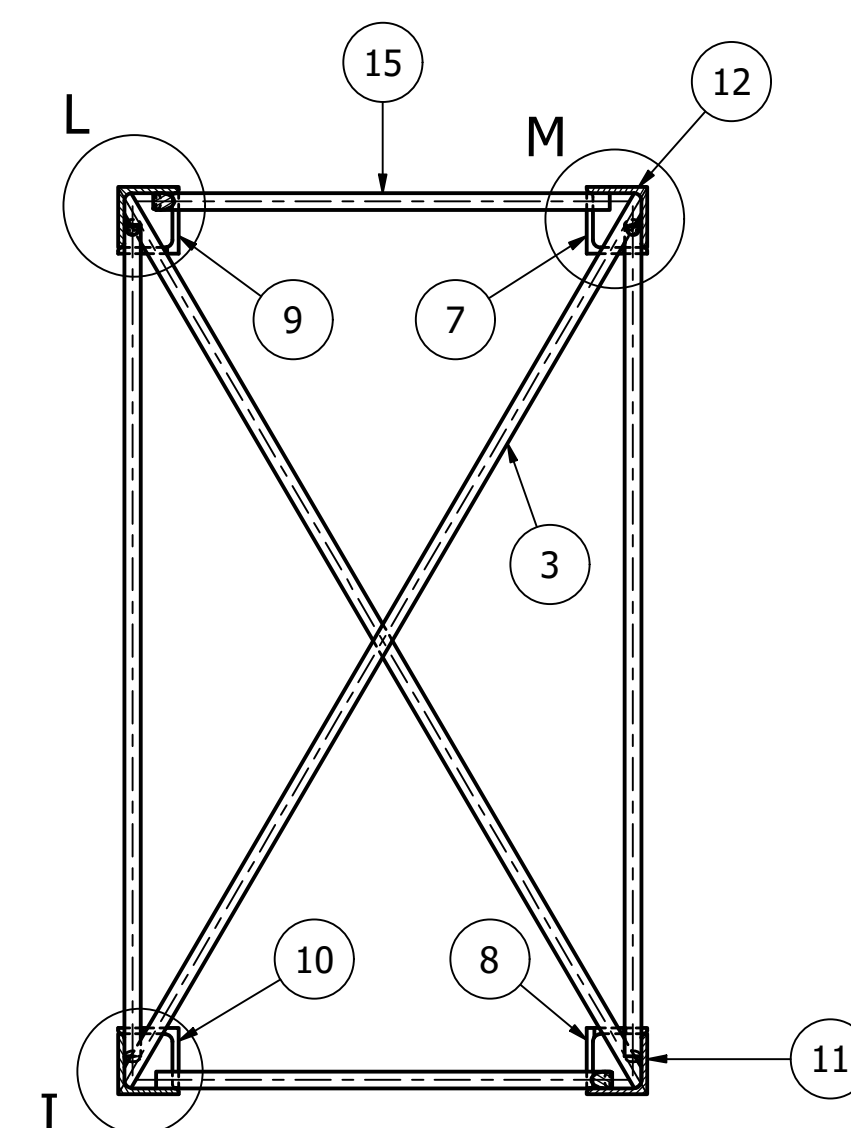
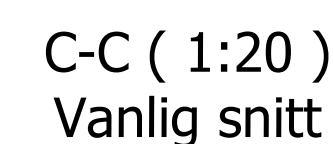
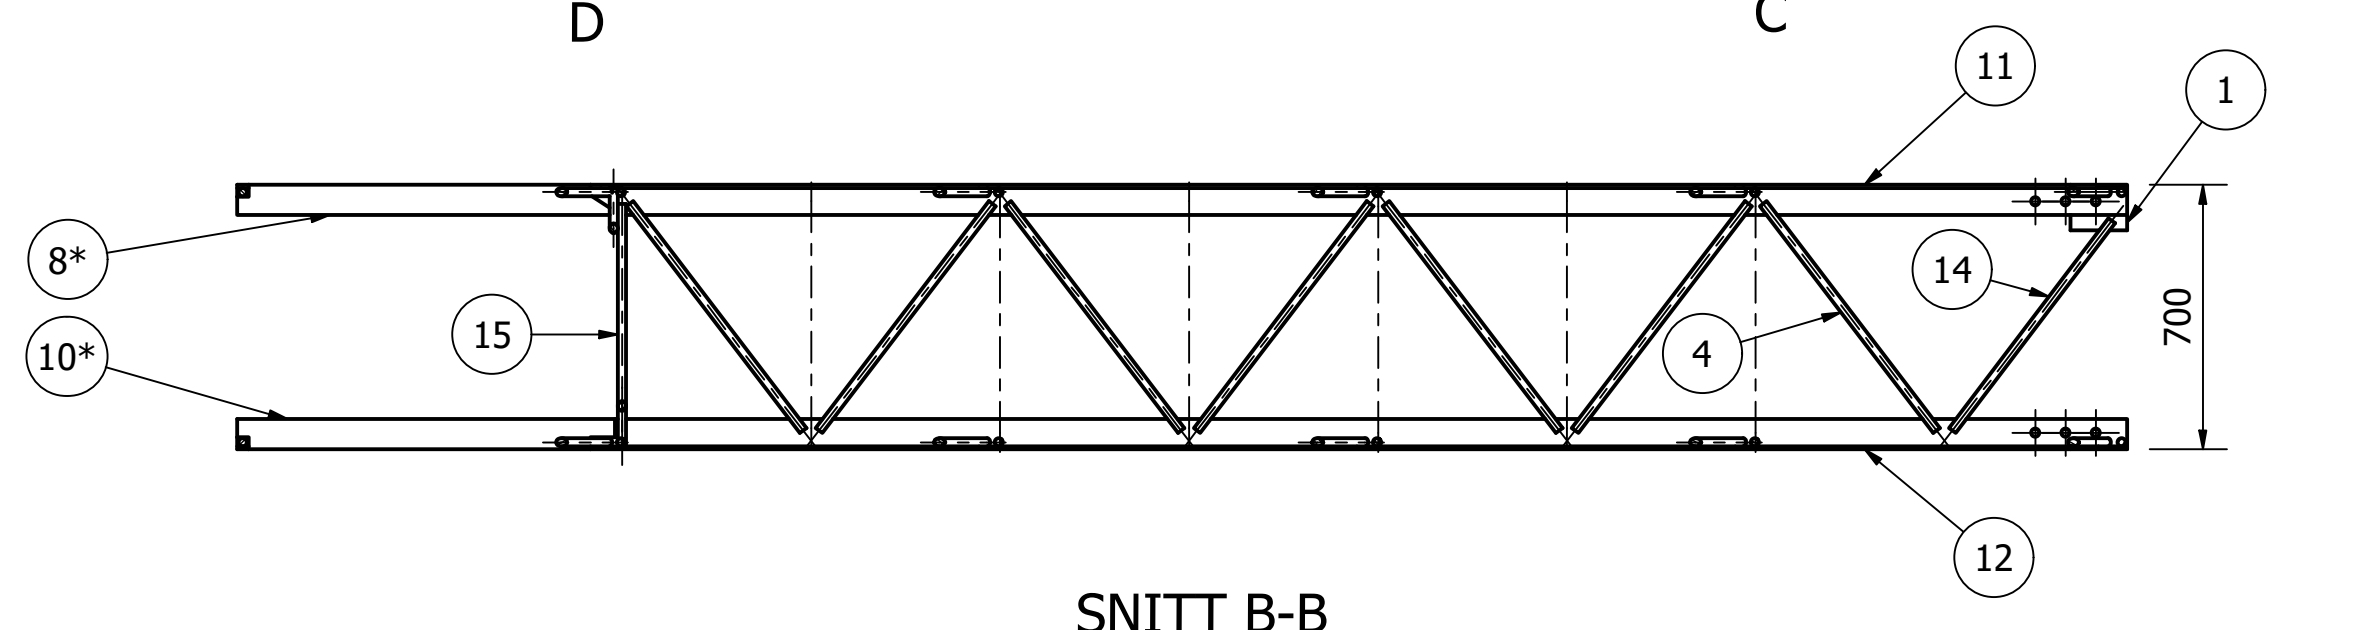
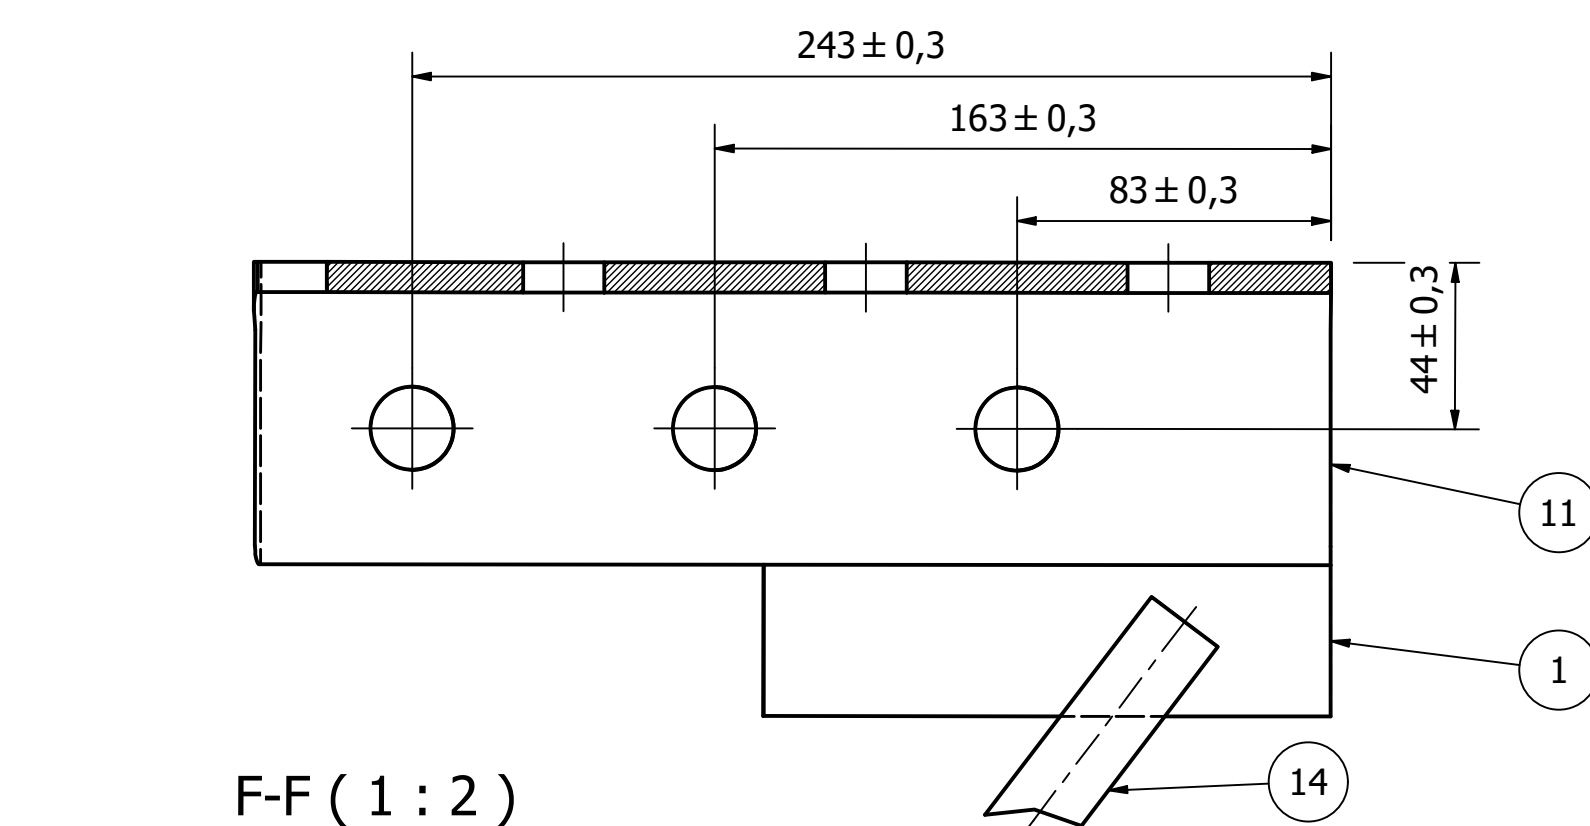
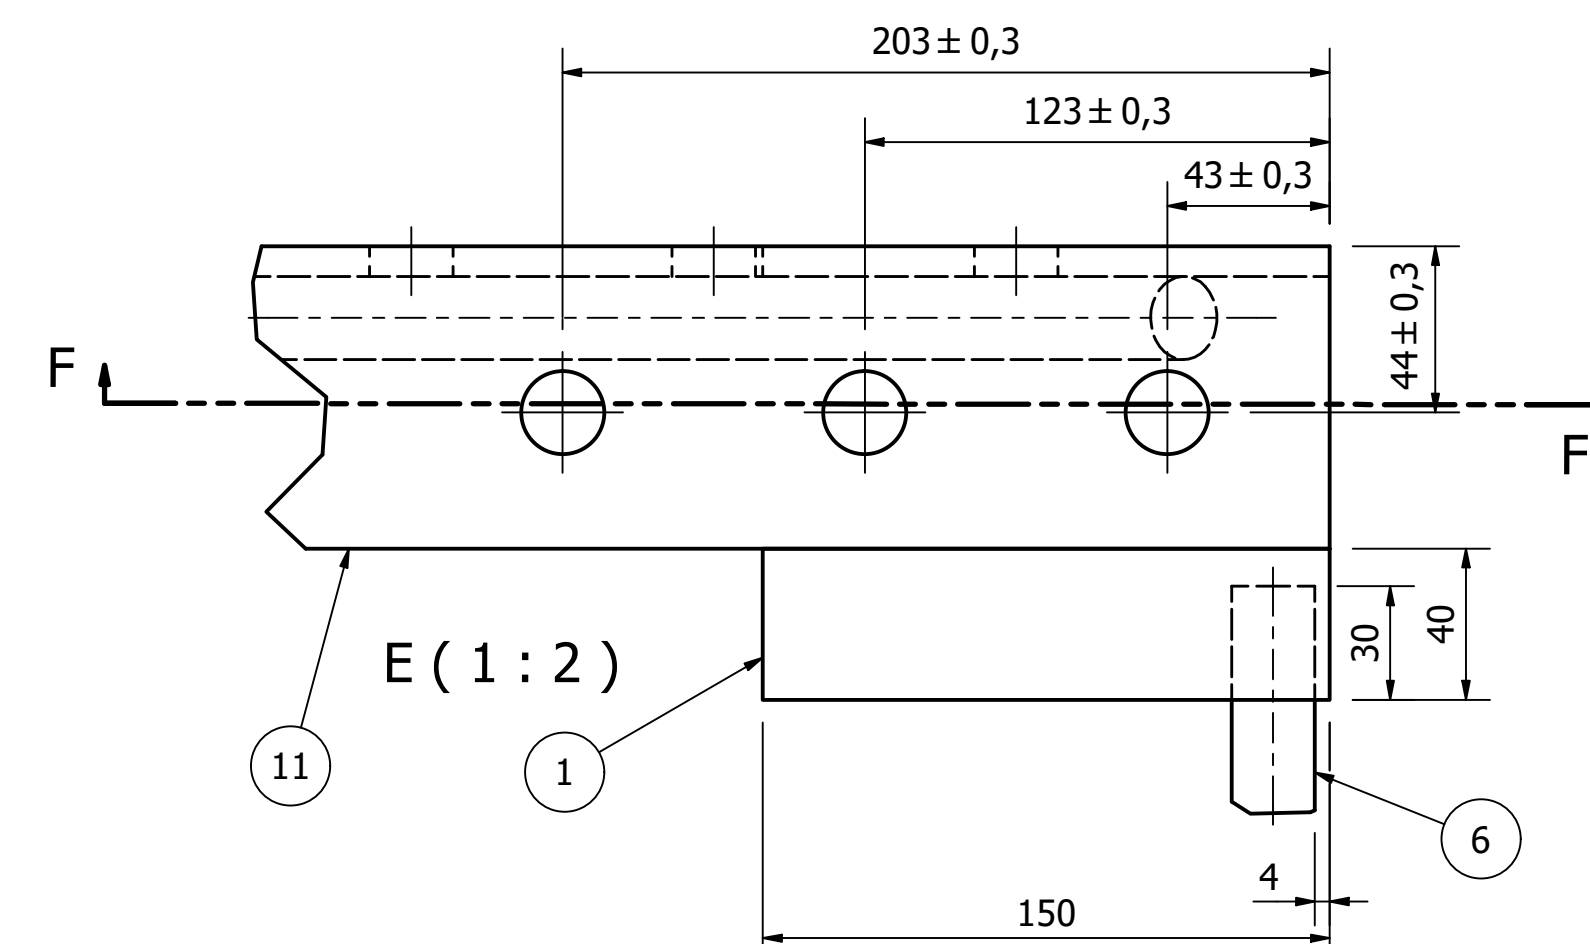


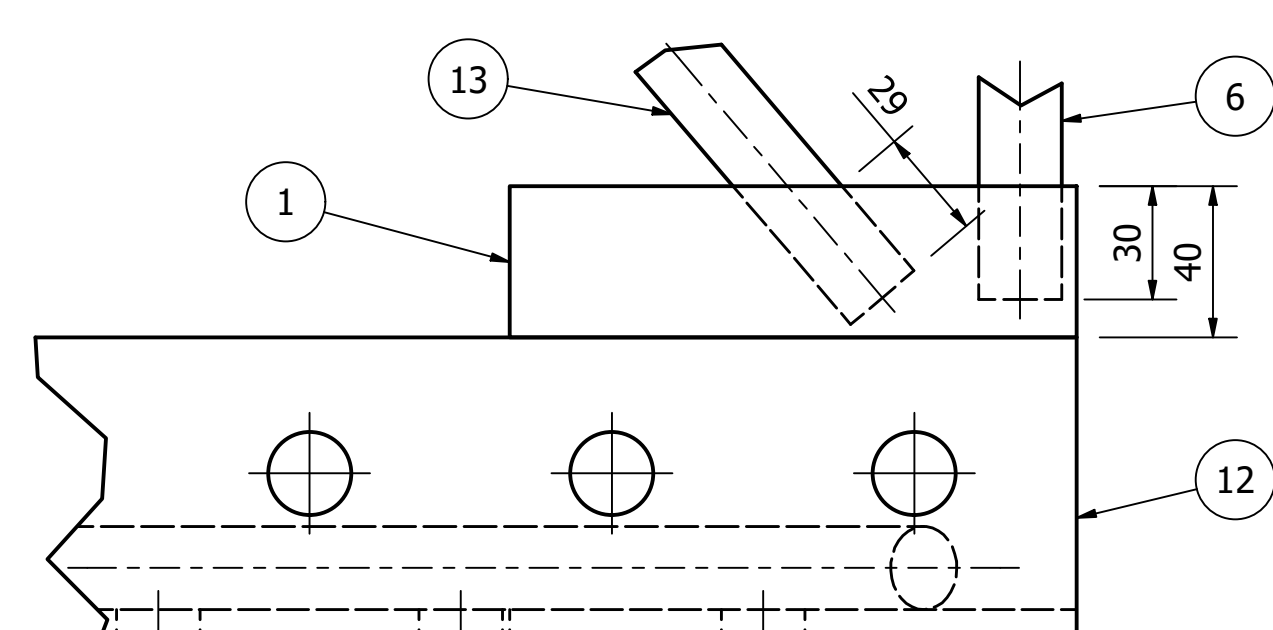


SNITT D-D
(1:10)

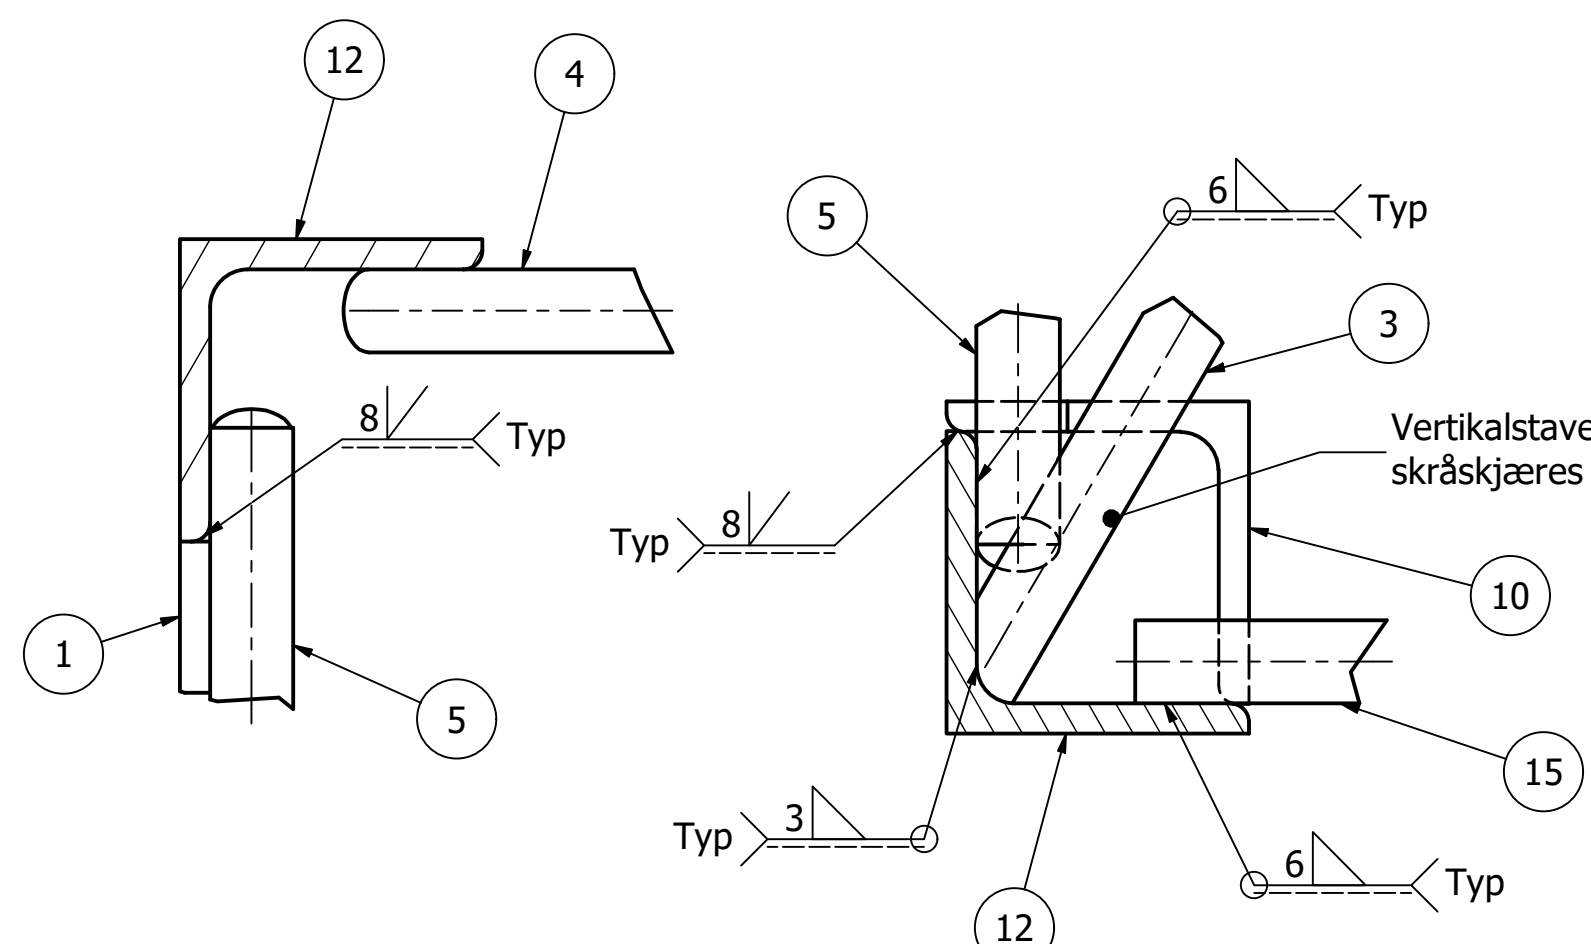


F-F (1 : 2)


$$E(1:2)$$

$$G(1:2)$$

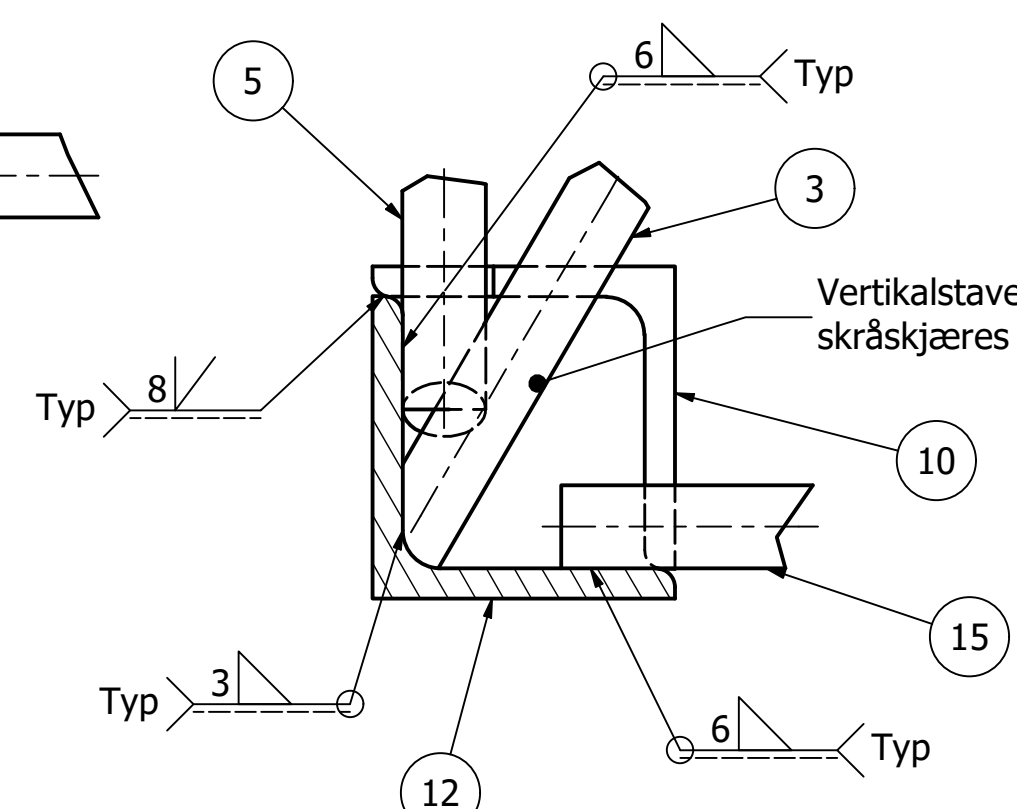
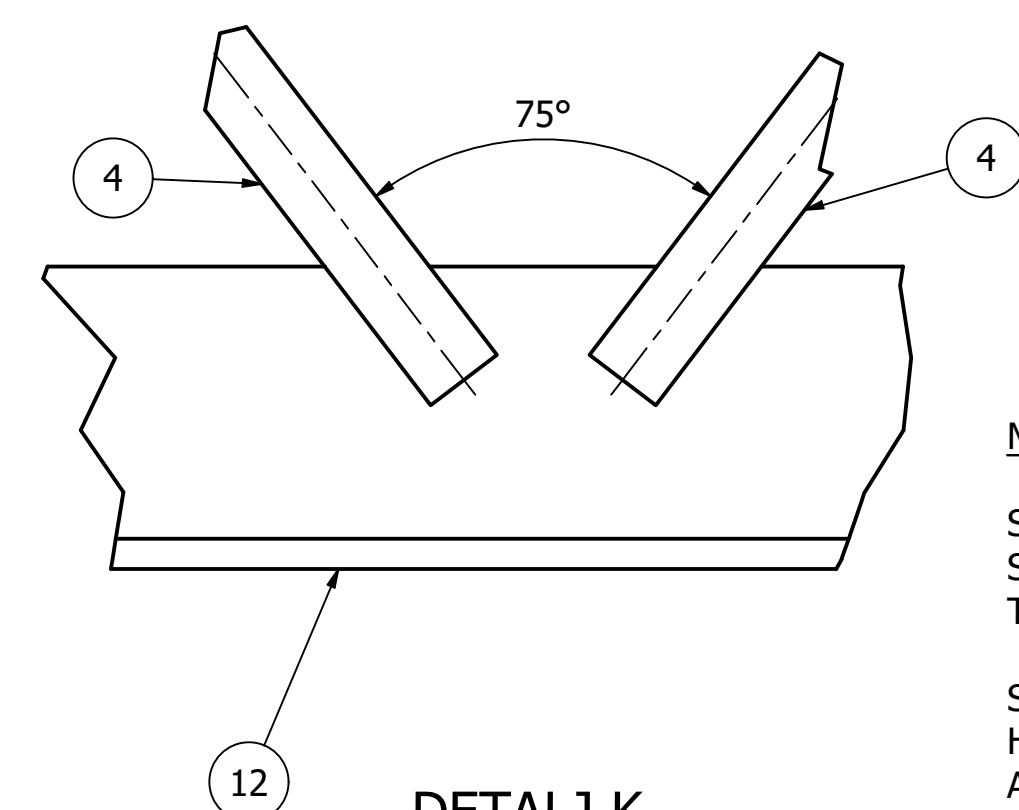
DETALJ H
(1 : 2)

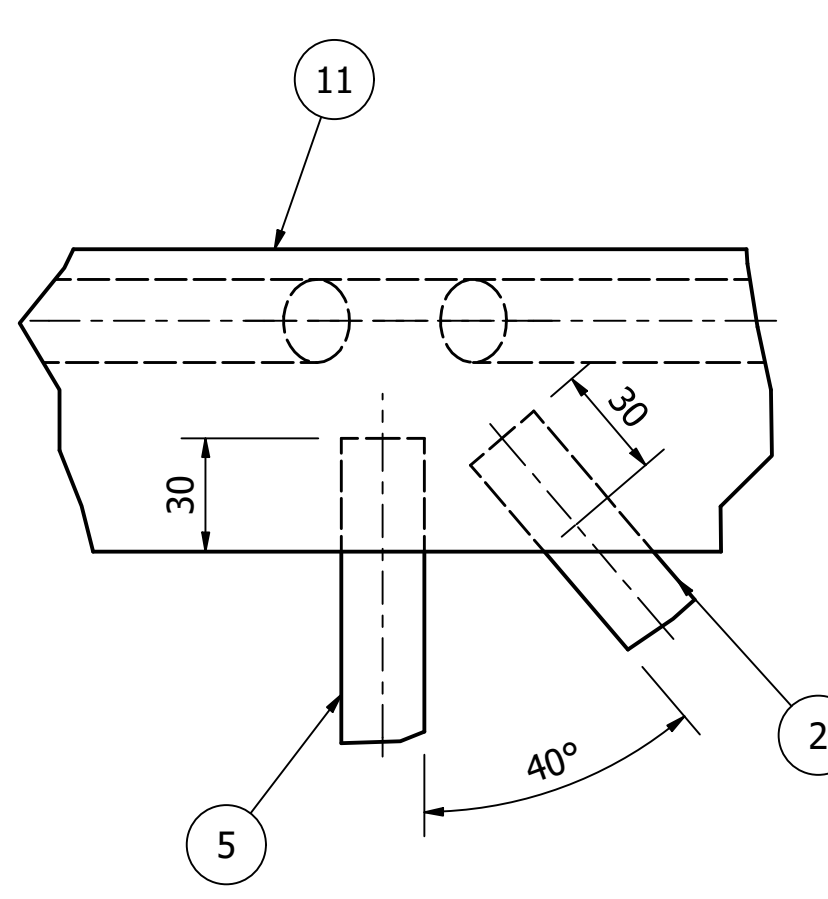


DETALJ I
(1 : 2)



DETALJ J
(1 : 2)



DETALJ K
(1 : 2)

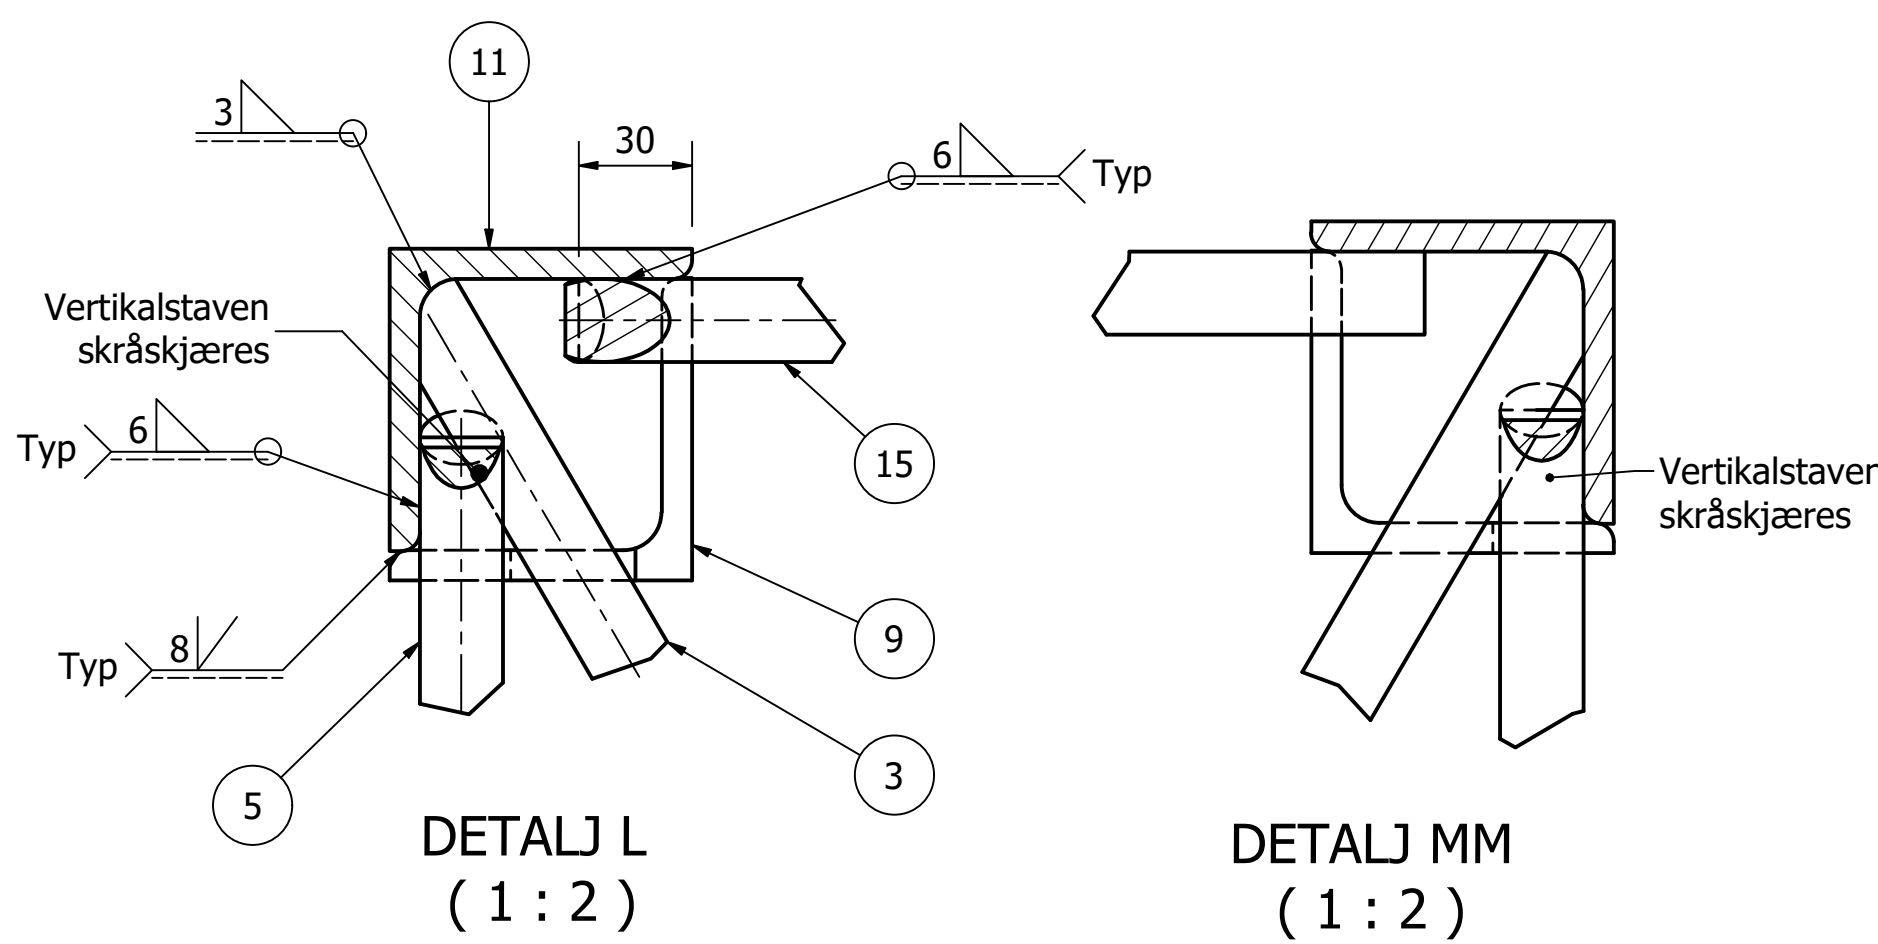

DETALJ L
(1 : 2)

DETALJ MM
(1 : 2)

Stålkvalitet: NS-EN 10025
Stålet skal inneholde 0,15-0,25 % Si
Toleranser: NS-ISO 2768-1-MIDDELS for boring av hull
NS-ISO 2768-1-GROV for øvrige mål
Sveising: NS 470 KLASSE B, NS-EN ISO 15609-1 og NS-EN 287
Hjørner og kanter avrundes/slipes.
Alt stål skal varmformsinkes: Fe/Zn NS-EN ISO 1461,
belegtykkelse min 115 µm.
Alle mål oppgitt i mm dersom ikke annet er angitt.

Artikelnummer = 112319

Antall	Pos. Nr.	Navn, type, dimensjon	Tegn. nr. / Standard		Materiale	F Nr. / Anmerkning	
000		Utgitt / Forsterket versjon av åk type14.		27.01.2022	PORMIR	HMH/BIOL.	
Rev.:		Revisjonen gjelder	Dato	Tegnet av	Kontroll. av	Godkjent	
Tegn.		Høyspenning, Kontaktledningsanlegg	Format:	Målestokk:	Fritekst 1		
		Åk type 14	A1	1:20	Fritekst 2		
		Enderamme V	Pro. Metode	Produsent	Fritekst 3		
		Produksjonstegning		Prod.tegn.nr			
			Blad	Erstaining for			
			1 / 1	Erstattet av			

Erstatter av	
Tegningsnummer:	EH-024536-000

Rev.