


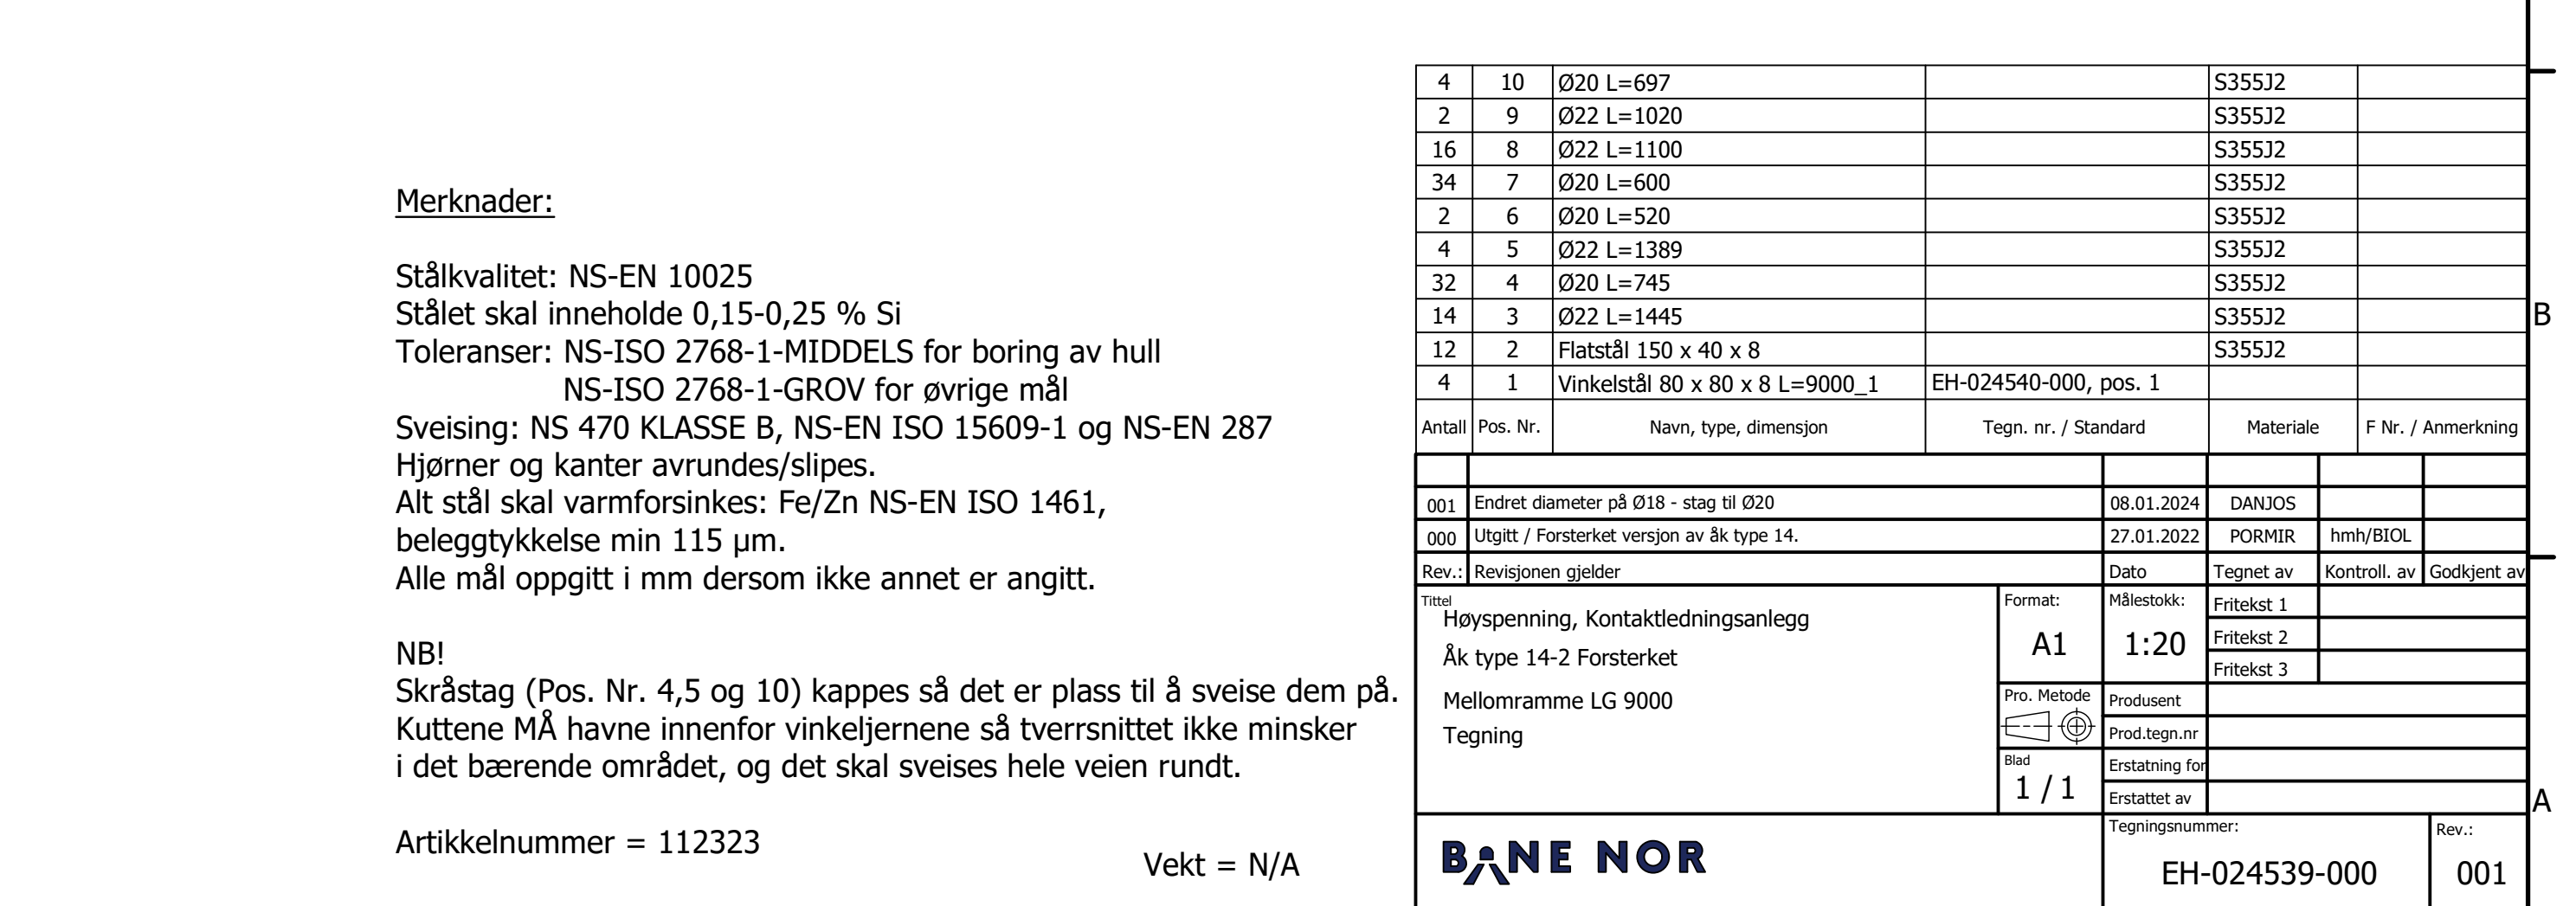

4	10	Ø20 L=697			S355J2	4	
2	9	Ø22 L=1020			S355J2		
16	8	Ø22 L=1100			S355J2		
34	7	Ø20 L=600			S355J2		
2	6	Ø20 L=520			S355J2		
4	5	Ø22 L=1389			S355J2		
32	4	Ø20 L=745			S355J2		
14	3	Ø22 L=1445			S355J2		
12	2	Flatstål 150 x 40 x 8			S355J2		
4	1	Vinkelstål 80 x 80 x 8 L=9000_1	EH-024540-000, pos. 1				
Antal		Pos. Nr.	Navn, type, dimensjon	Tegn. nr. / Standard	Materiale	F Nr. / Anmerkning	
001	Endret diameter på Ø18 - stag til Ø20			08.01.2024	DANJOS		
000	Utgitt / Forsterket versjon av åk type 14.			27.01.2022	PORMIR	hmh/BIL	
Rev.:	Revisjonen gjelder			Dato	Tegnet av	Kontroll. av	Godkjent av
1	Høyspenning, Kontaktledningsanlegg			Målestokk:	Fritekst 1		
	Åk type 14-2 Forsterket			A1	1:20	Fritekst 2	
	Mellomramme LG 9000					Fritekst 3	
	Tegning			Pro. Metode	Produsent		
					Prod.tegn.nr		
				Blad	Erstating for		
				1 / 1	Erstattet av		
BANE NOR				Tegningsnummer:			Rev.:
				EH-024539-000			001