



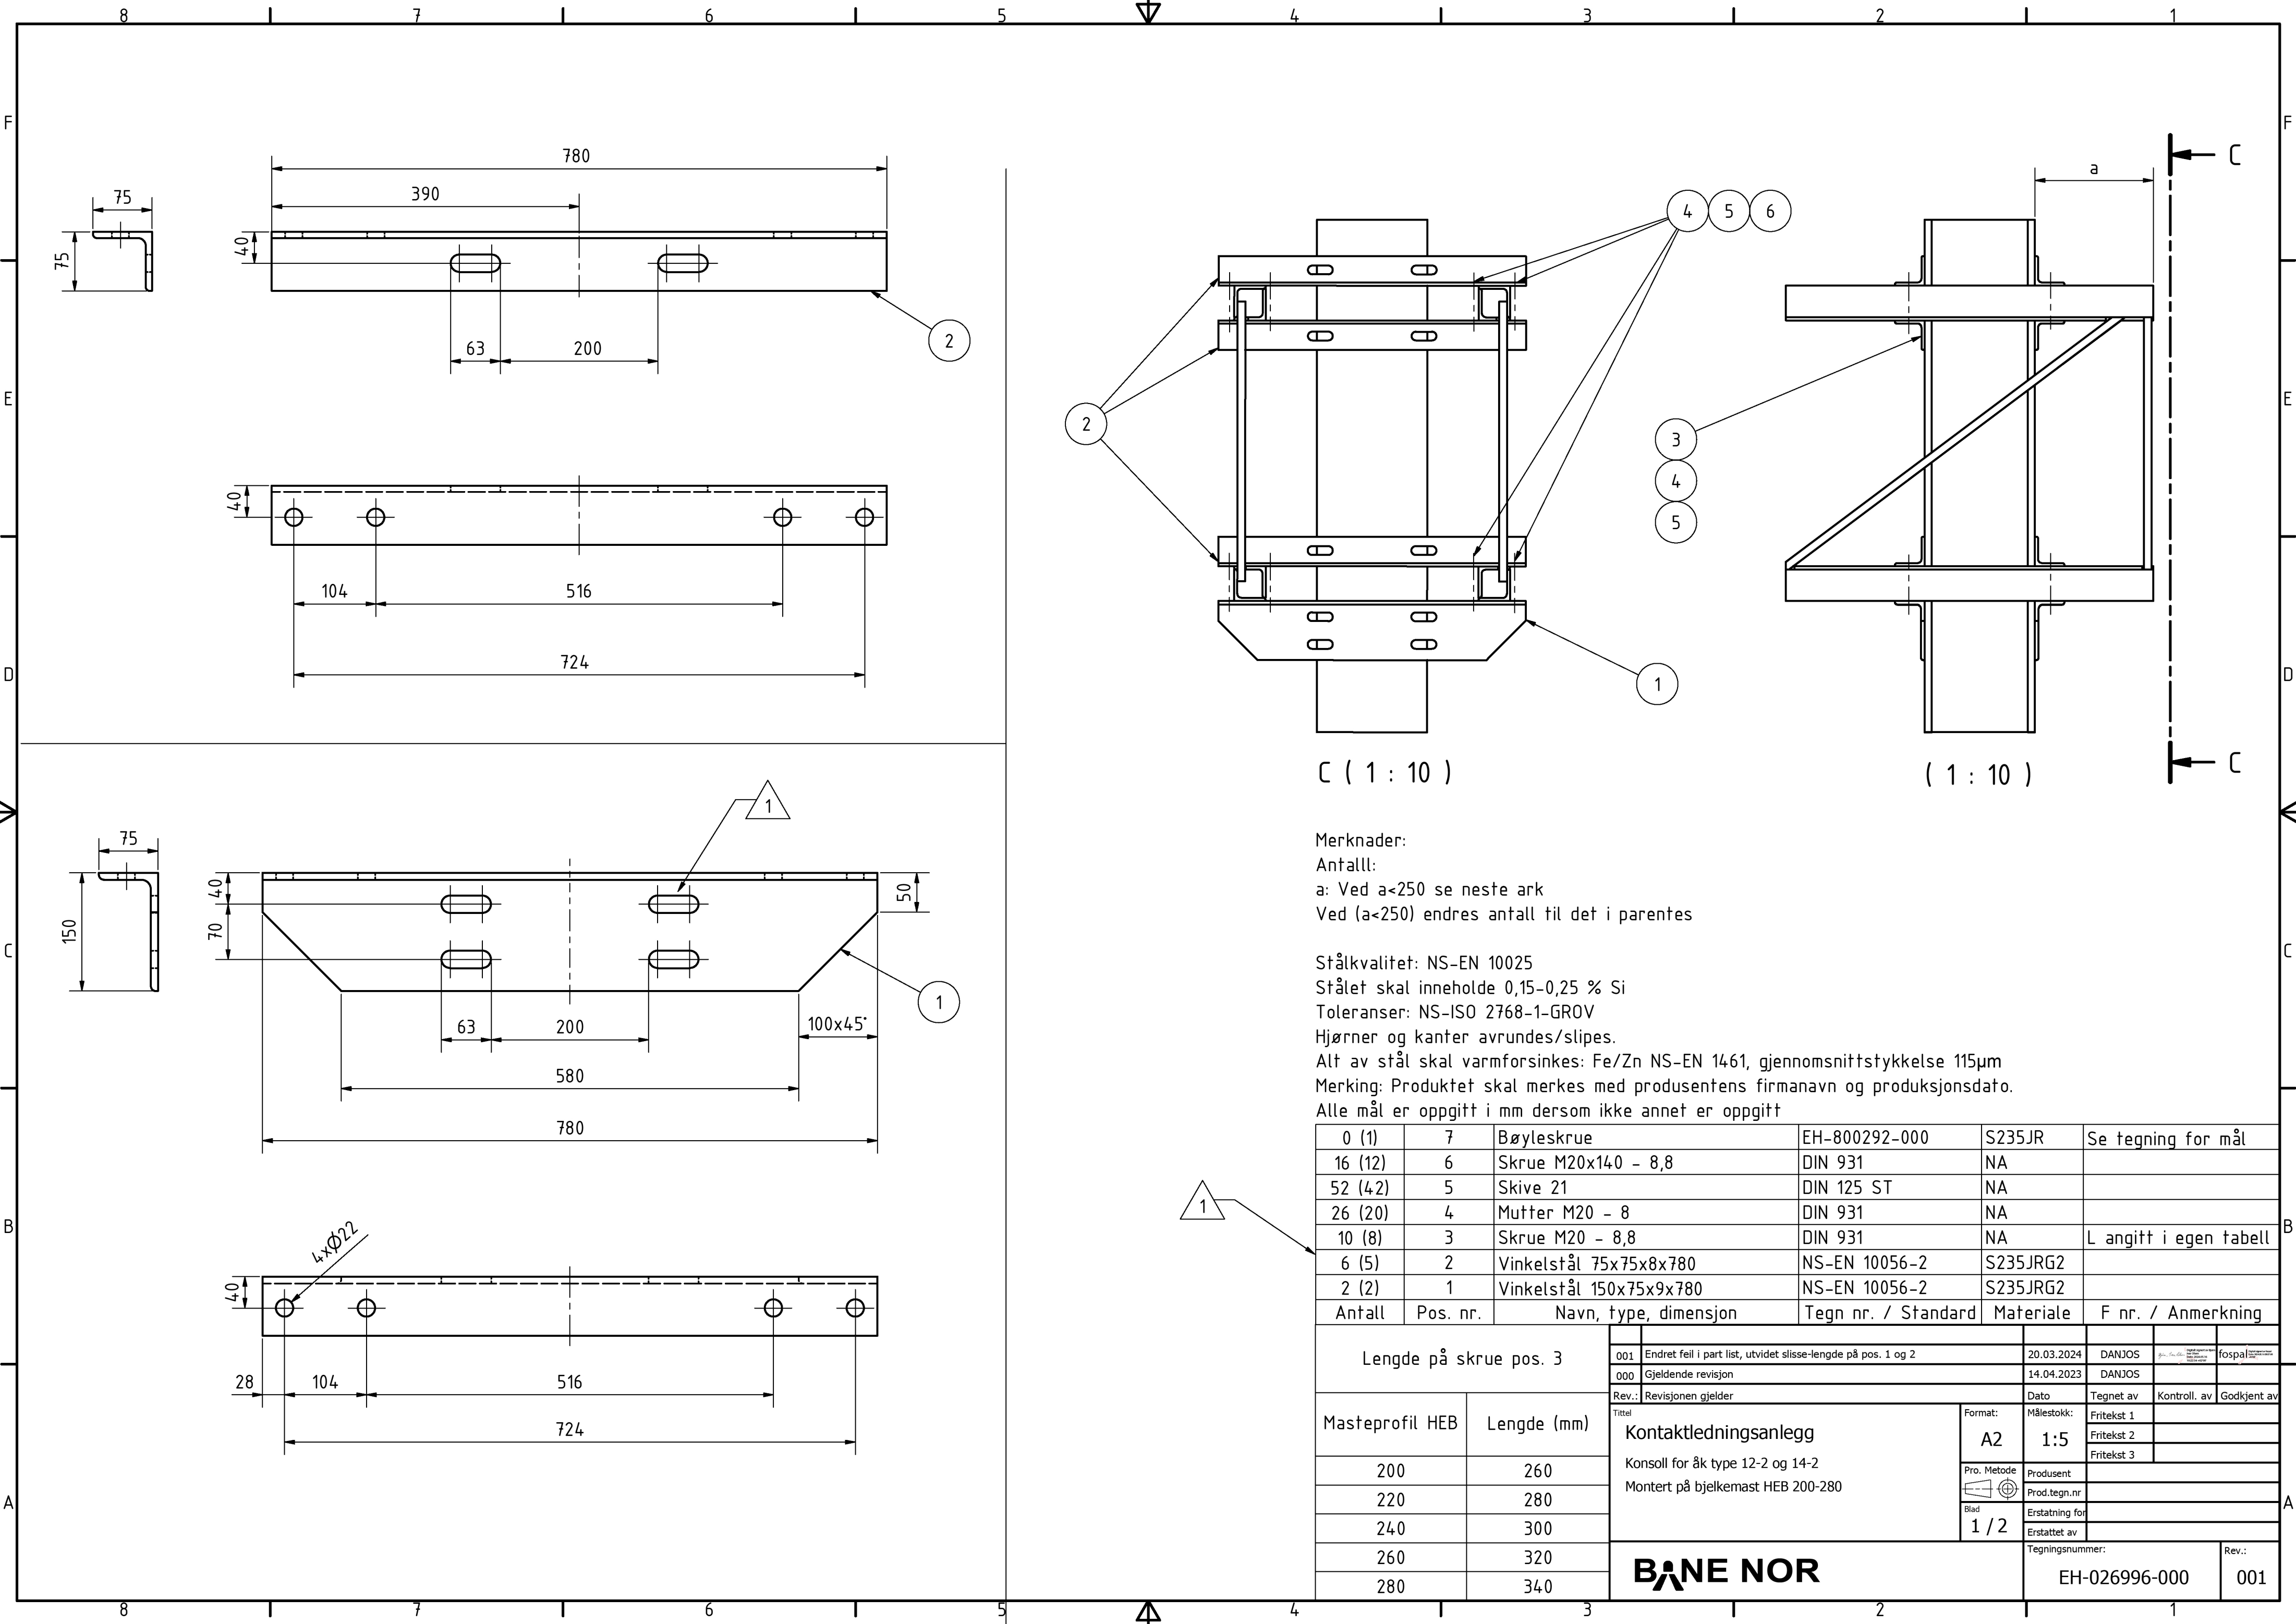

Merknader:
Antall:
a: Ved a<250 se neste ark
Ved (a<250) endres antall til det i parentes

Stålkvalitet: NS-EN 10025
Stålet skal inneholde 0,15-0,25 % Si
Toleranser: NS-ISO 2768-1-GROV
Hjørner og kanter avrundes/slipes.
Alt av stål skal varmforsinkes: Fe/Zn NS-EN 1461, gjennomsnittstykkelse 115µm
Merking: Produktet skal merkes med produsentens firmanavn og produksjonsdato.
Alle mål er oppgitt i mm dersom ikke annet er oppgitt


0 (1)	7	Bøyleskrue	EH-800292-000	S235JR	Se tegning for mål
16 (12)	6	Skrue M20x140 - 8,8	DIN 931	NA	
52 (42)	5	Skive 21	DIN 125 ST	NA	
26 (20)	4	Mutter M20 - 8	DIN 931	NA	
10 (8)	3	Skrue M20 - 8,8	DIN 931	NA	L angitt i egen tabell
6 (5)	2	Vinkelstål 75x75x8x780	NS-EN 10056-2	S235JRG2	
2 (2)	1	Vinkelstål 150x75x9x780	NS-EN 10056-2	S235JRG2	
Antall	Pos. nr.	Navn, type, dimensjon	Tegn nr. / Standard	Materiale	F nr. / Anmerkning
Lengde på skrue pos. 3					
Masteprofil HEB		Lengde (mm)			
200		260			
220		280			
240		300			
260		320			
280		340			
Kontaktledningsanlegg			Format: A2	Målestokk: 1:5	
Konsoll for åk type 12-2 og 14-2			Pro. Metode	Produsent	
Montert på bjelkemast HEB 200-280			Prod.tegn.nr		
			Blad 1 / 2	Erstatning for	
			Erstattet av		
Tegningsnummer:				EH-026996-000	Rev.: 001

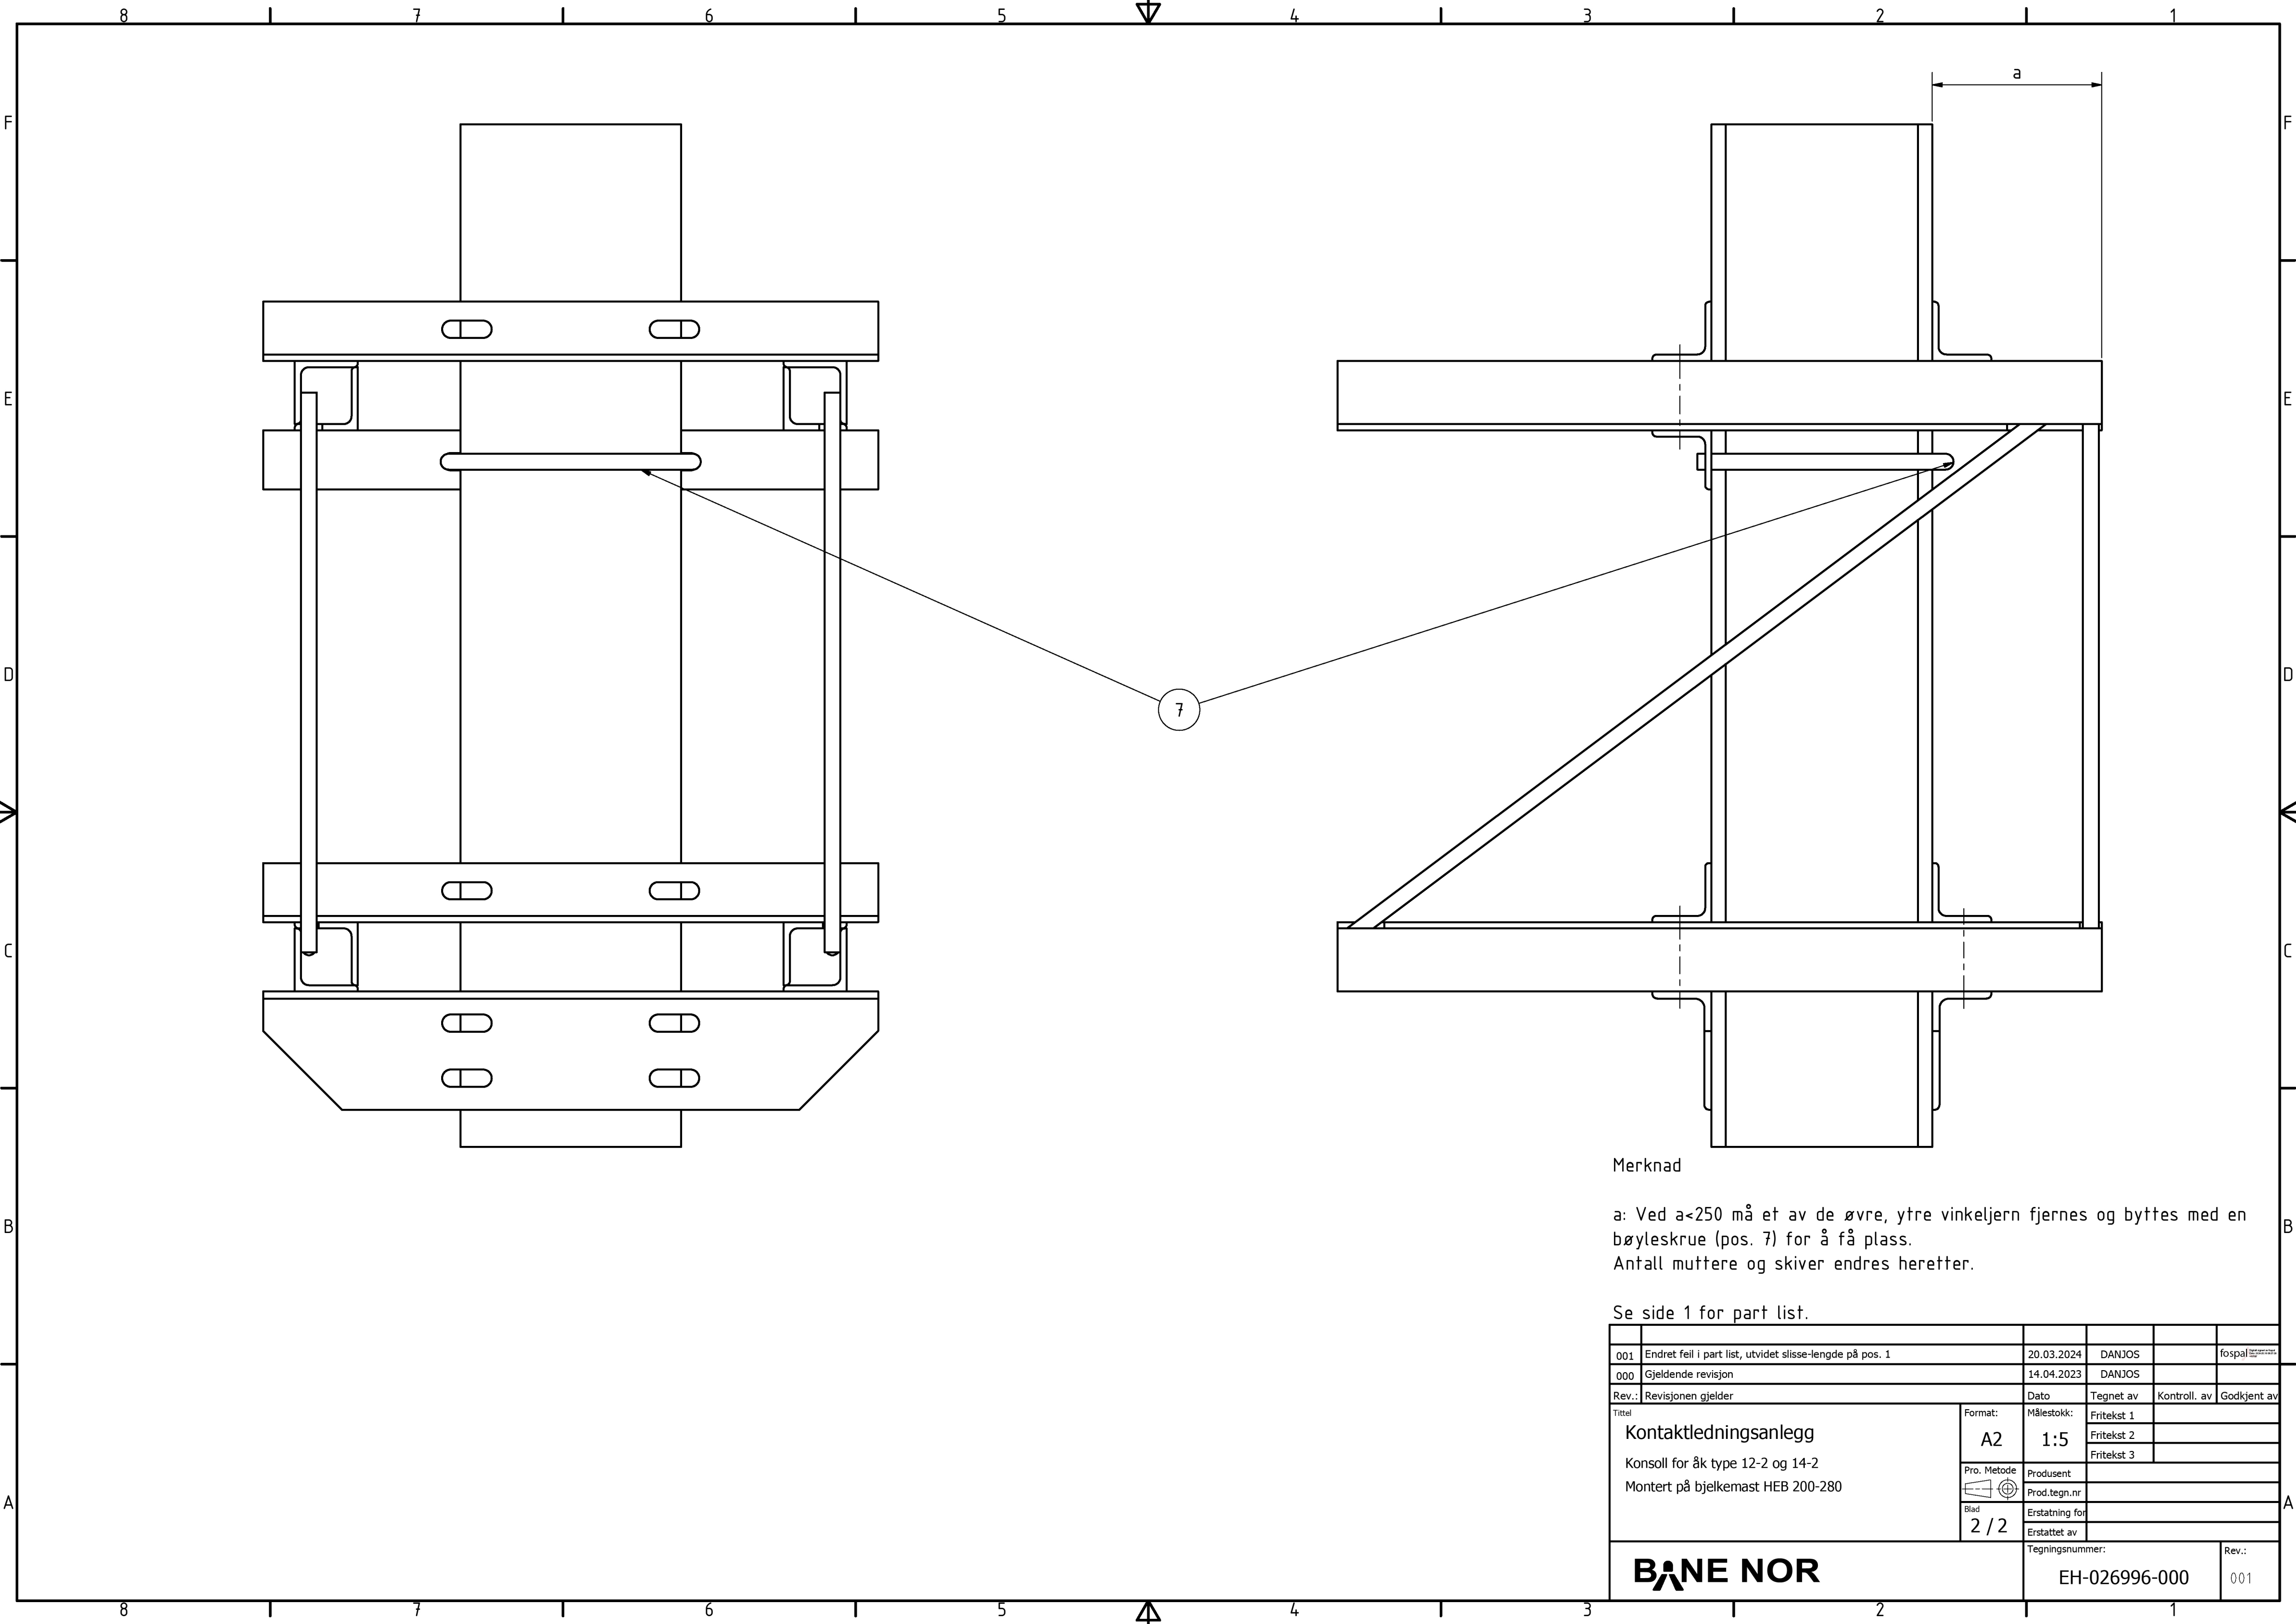

Merknad

a: Ved a<250 må et av de øvre, ytre vinkeljern fjernes og byttes med en bøyleskrue (pos. 7) for å få plass.
Antall muttere og skiver endres heretter.

Se side 1 for part list.

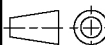001	Endret feil i part list, utvidet slisse-lengde på pos. 1	20.03.2024	DANJOS		fospal
000	Gjeldende revisjon	14.04.2023	DANJOS		
Rev.:	Revisjonen gjelder	Dato	Tegnet av	Kontroll. av	Godkjent av
Tittel Kontaktledningsanlegg Konsoll for åk type 12-2 og 14-2 Montert på bjelkemast HEB 200-280		Format:	Målestokk:	Fritekst 1	
		A2	1:5	Fritekst 2	
				Fritekst 3	
		Pro. Metode	Produsent		
			Prod.tegn.nr		
		Blad	Erstatning for		
		2 / 2	Erstattet av		
		Tegningsnummer:			Rev.:
		EH-026996-000			001