


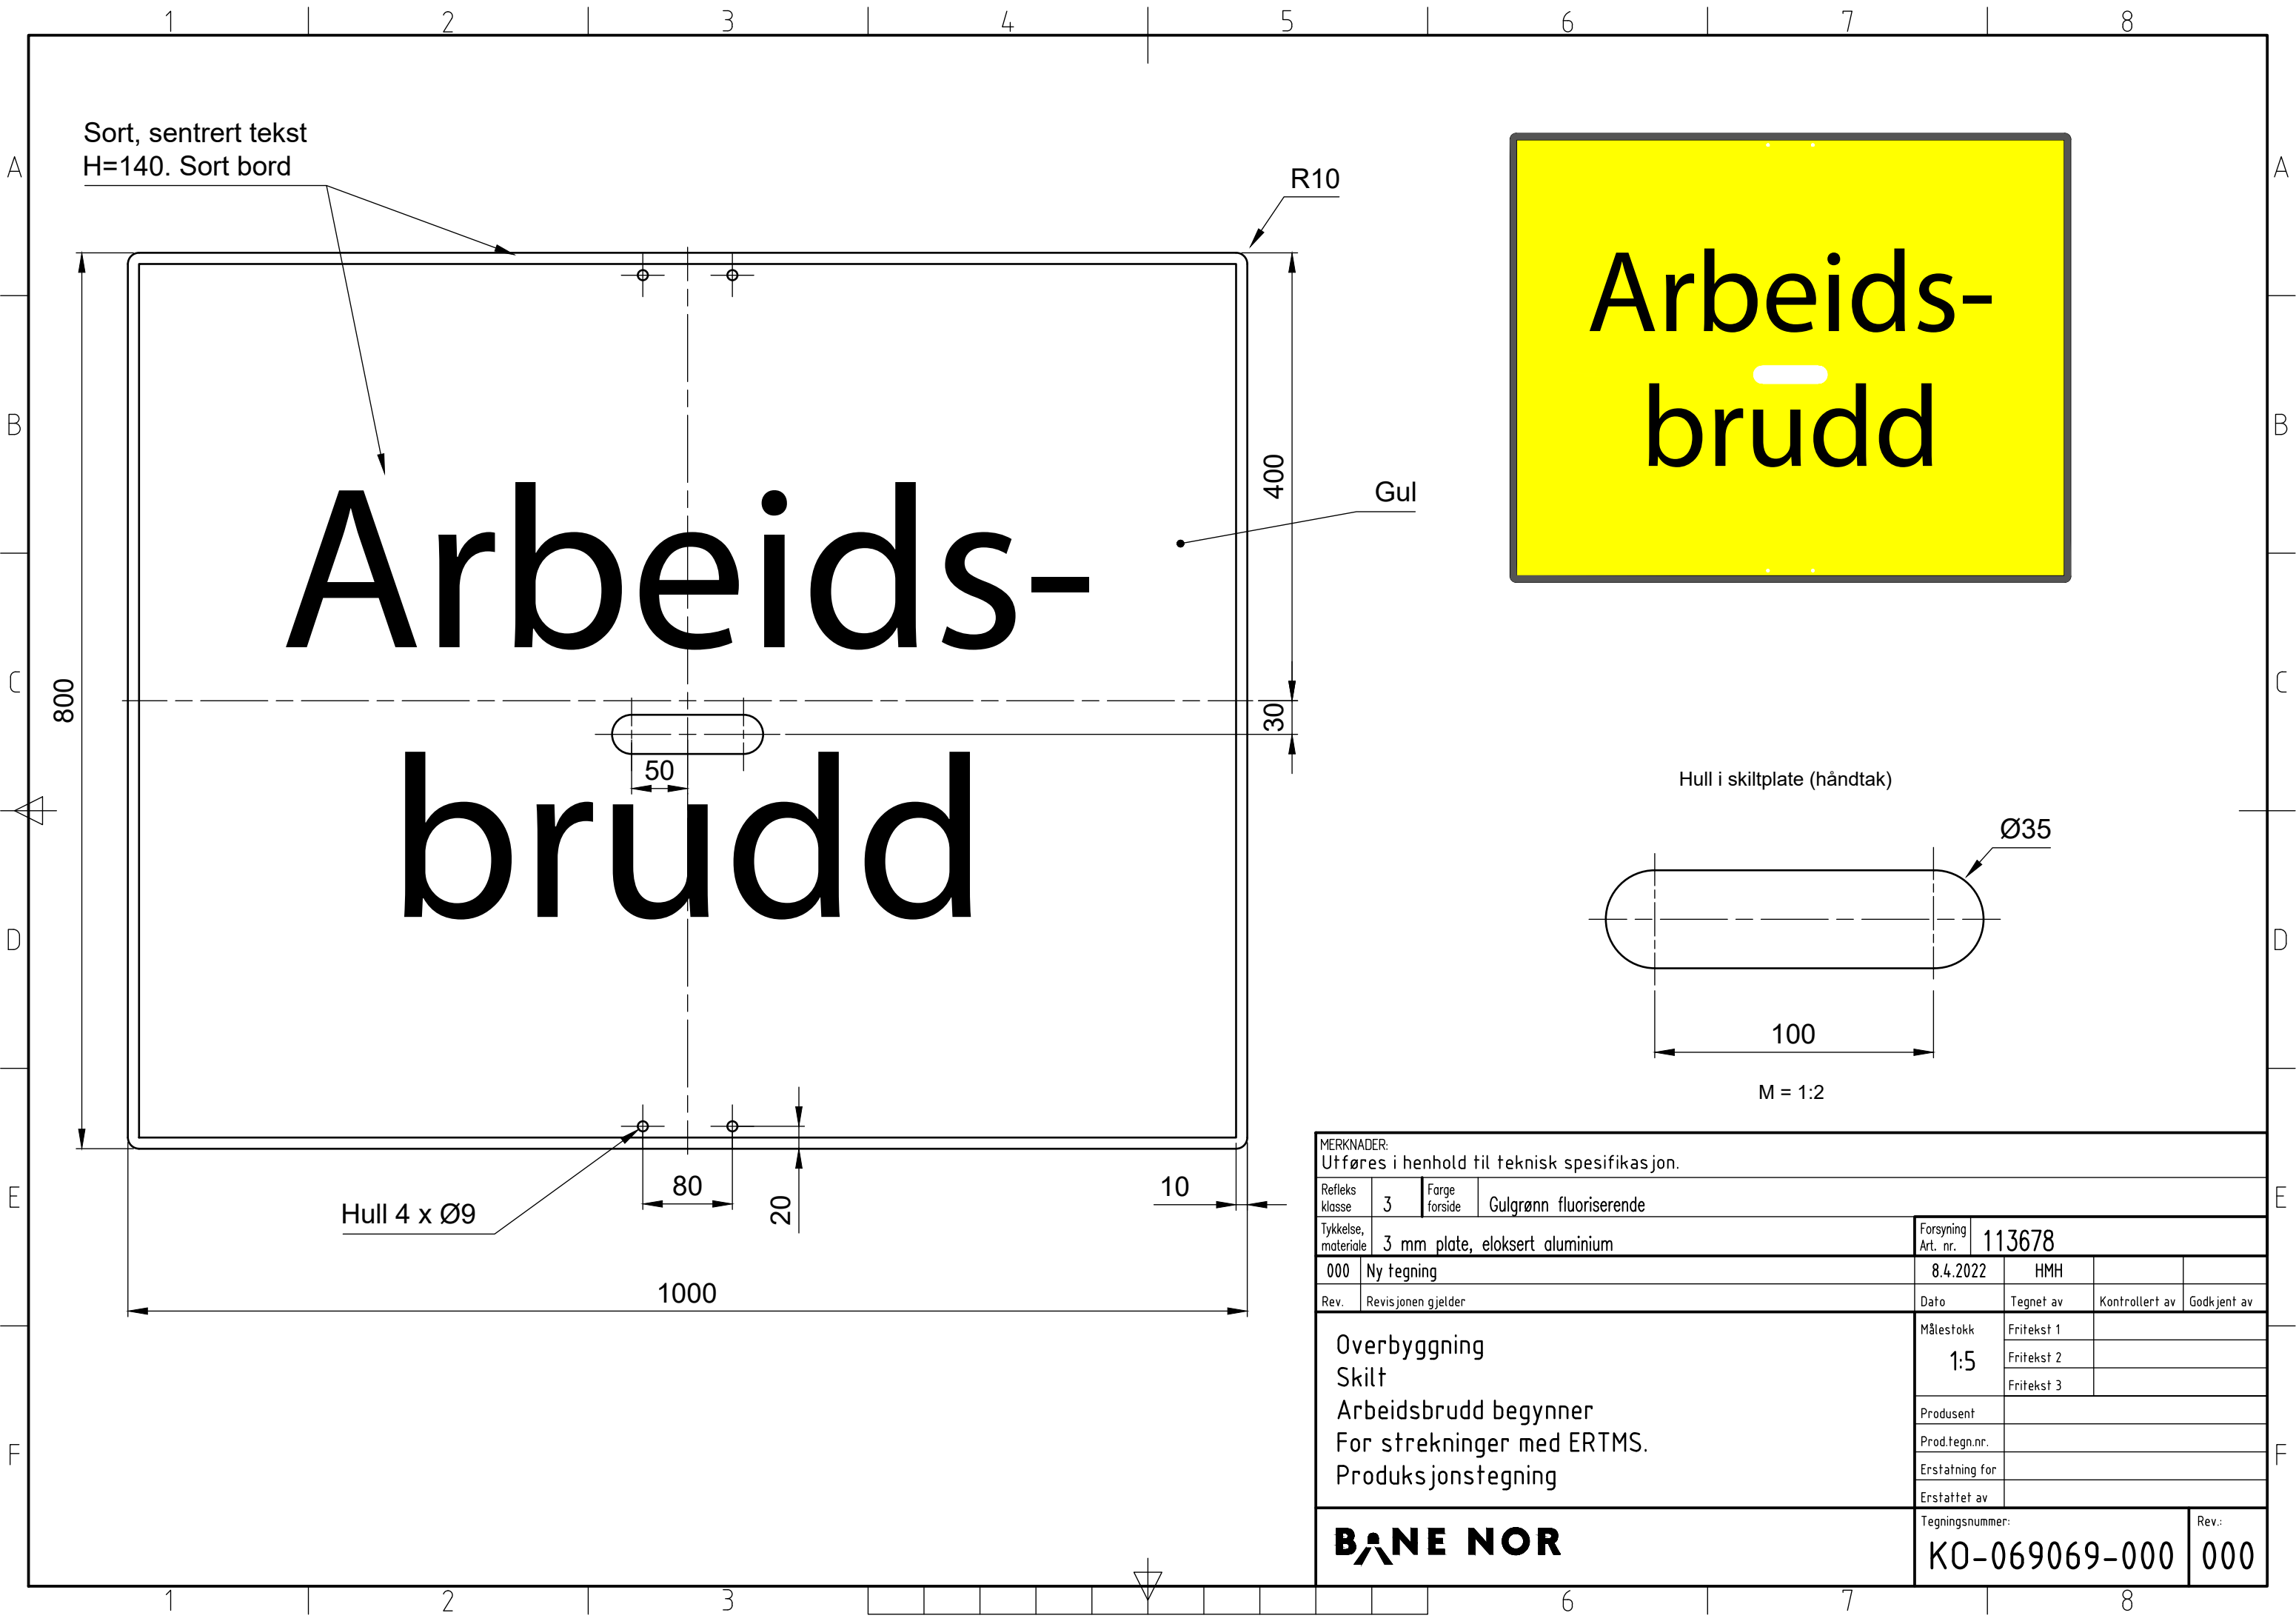

Sort, sentrert tekst
H=140. Sort bord

R10

Gul

Arbeids-
brudd

Hull i skiltplate (håndtak)

Ø35

100

M = 1:2

Hull 4 x Ø9

80

20

10

1000

MERKNADER:
Utføres i henhold til teknisk spesifikasjon.

Refleks klasse	3	Farge forside	Gulgrønn fluoriserende									
Tykkelse, materiale	3 mm plate, eloksert aluminium						Forsyning Art. nr.	113678				
000	Ny tegning						8.4.2022	HMH				
Rev.	Revisjonen gjelder						Dato	Tegnet av	Kontrollert av	Godkjent av		
Overbygging Skilt Arbeidsbrudd begynner For strekninger med ERTMS. Produksjonstegning							Målestokk	Fritekst 1				
							1:5	Fritekst 2				
								Fritekst 3				
							Produsent					
							Prod.tegn.nr.					
							Erstatning for					
							Erstattet av					
BANE NOR							Tegningsnummer:			Rev.:		
							KO-069069-000			000		